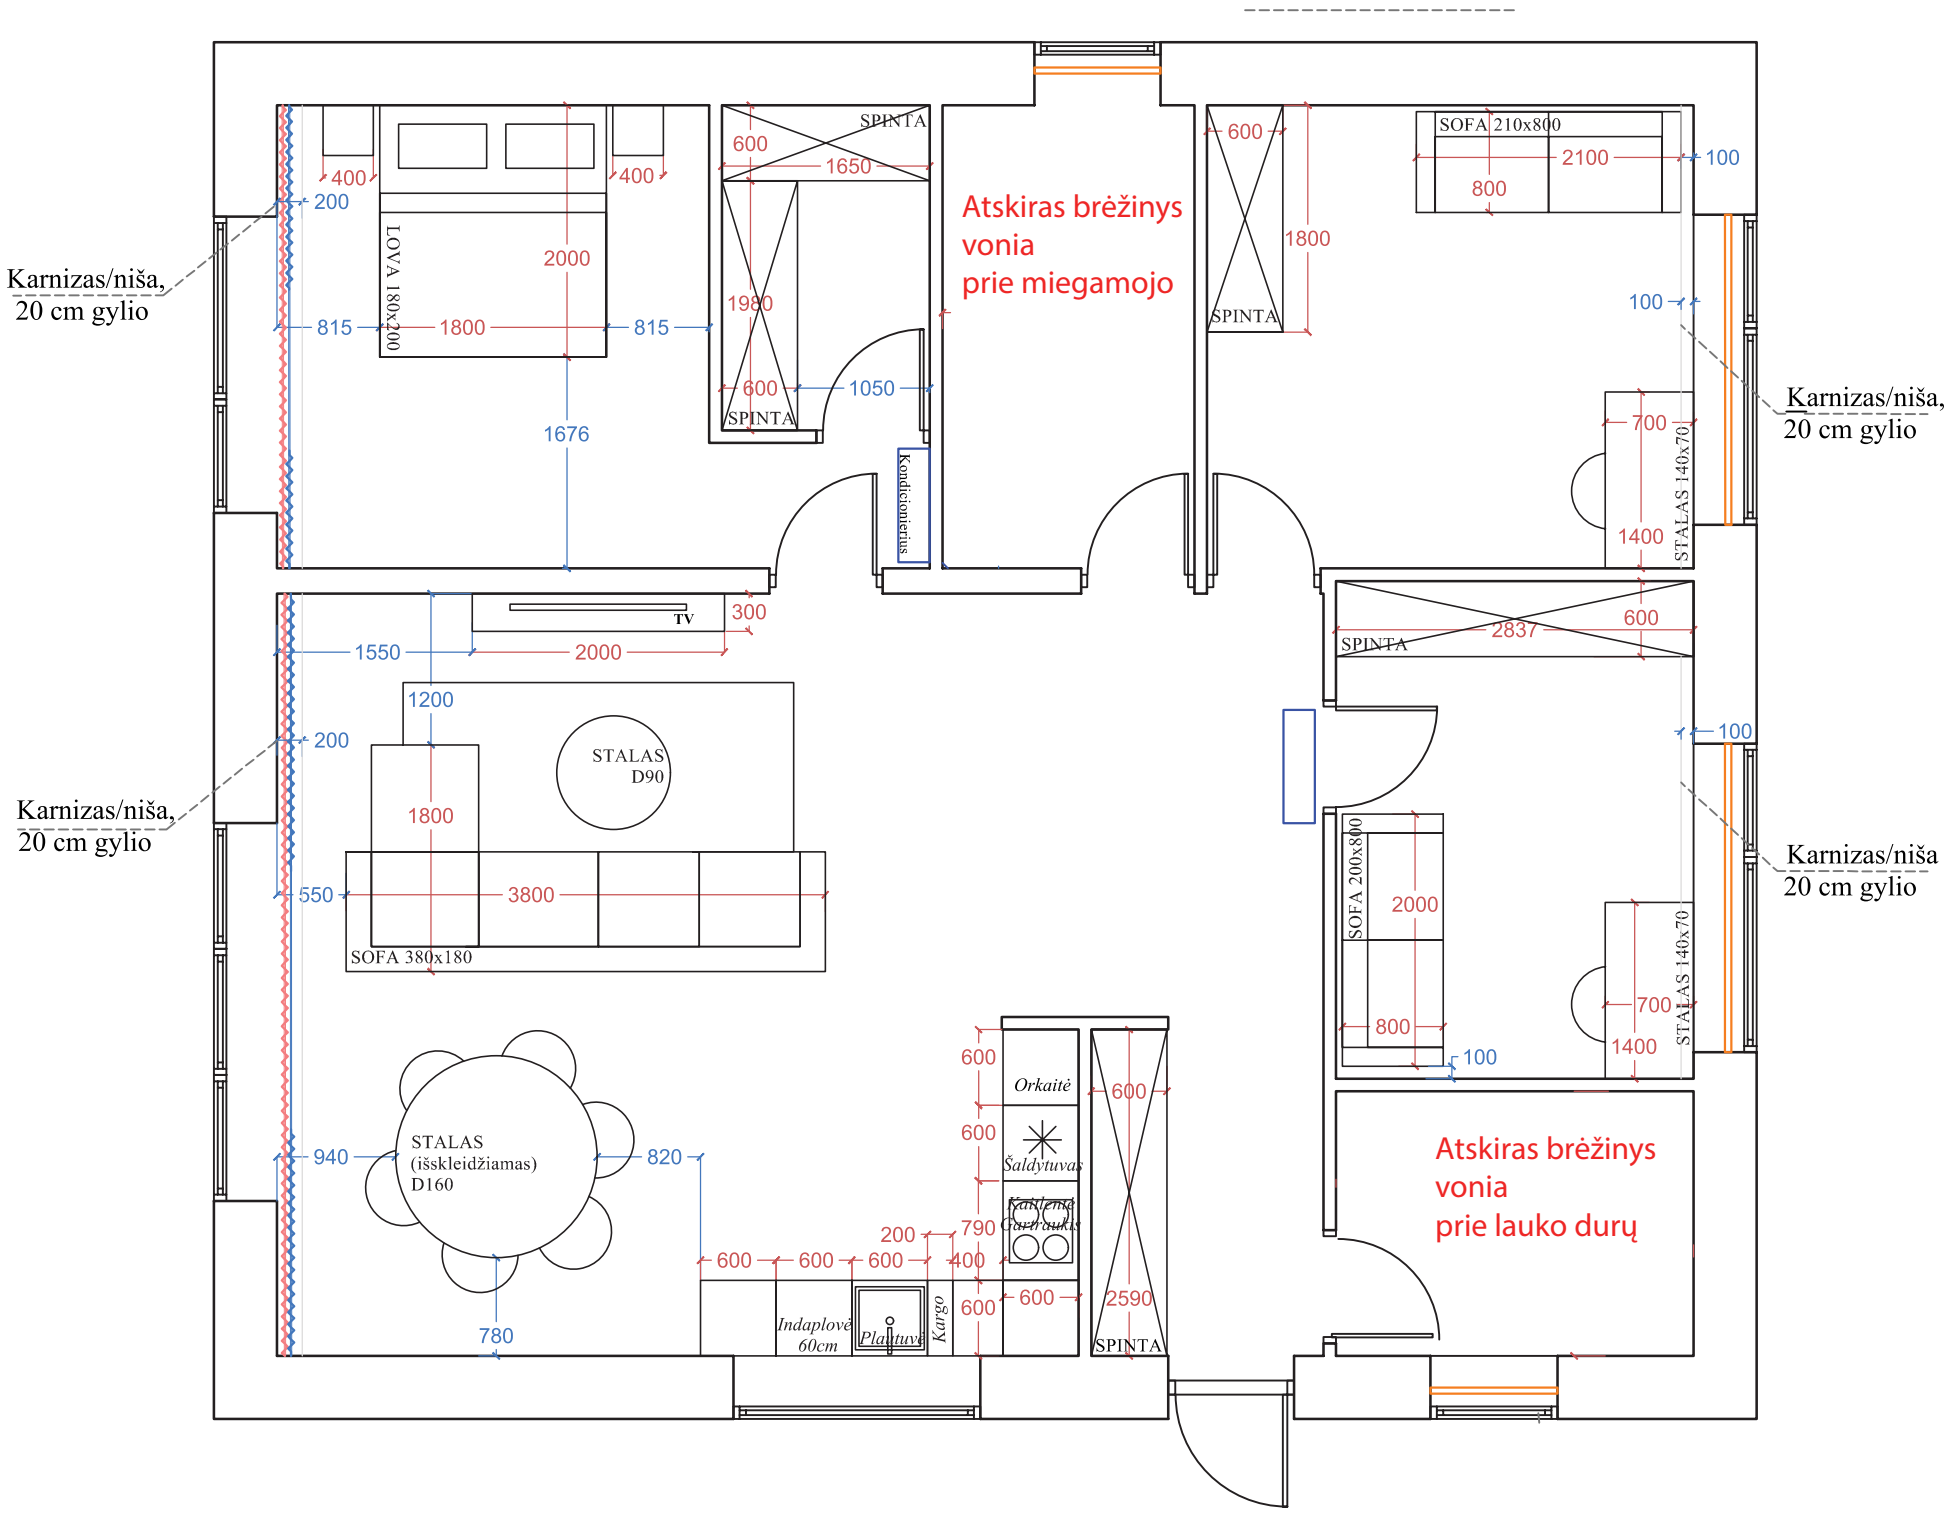


Medinės žaliuzės

Dieninės užuolaidos

Naktinės užuolaidos

Santechnikos slėpimui gipsinė sienutė

PASTABOS:

1. Matmenys pateikti milimetrais, atstumus tikslintis pagal faktą.
2. Altitudės nurodytos metrais, nuo grindų su danga.
3. Matmenis, altitudes ir kiekius tikslinti statybos darbų metu.
4. El. prietaisų ir šviestuvų padėtys gali koreguotis parinkus šviestuvus.
5. Visus plano ir situacijos nesutapimus derinti su užsakovu ir/ar interjero dizaineriu.


A3 formatas


APIE NAMŲ INTERJERĄ
tel. nr. +37067573530 el. paštas: interjeras@apienamus.com

Dizainerė	Ieva Juozapaitė	+370 675 73 530	Dokumento žymuo
Tech. dalis	Miglė Bobinaitė		P042_2025/adresas
Užsakovas	SIGITA		

BALDŲ PLANAS M 1:50

P042_1

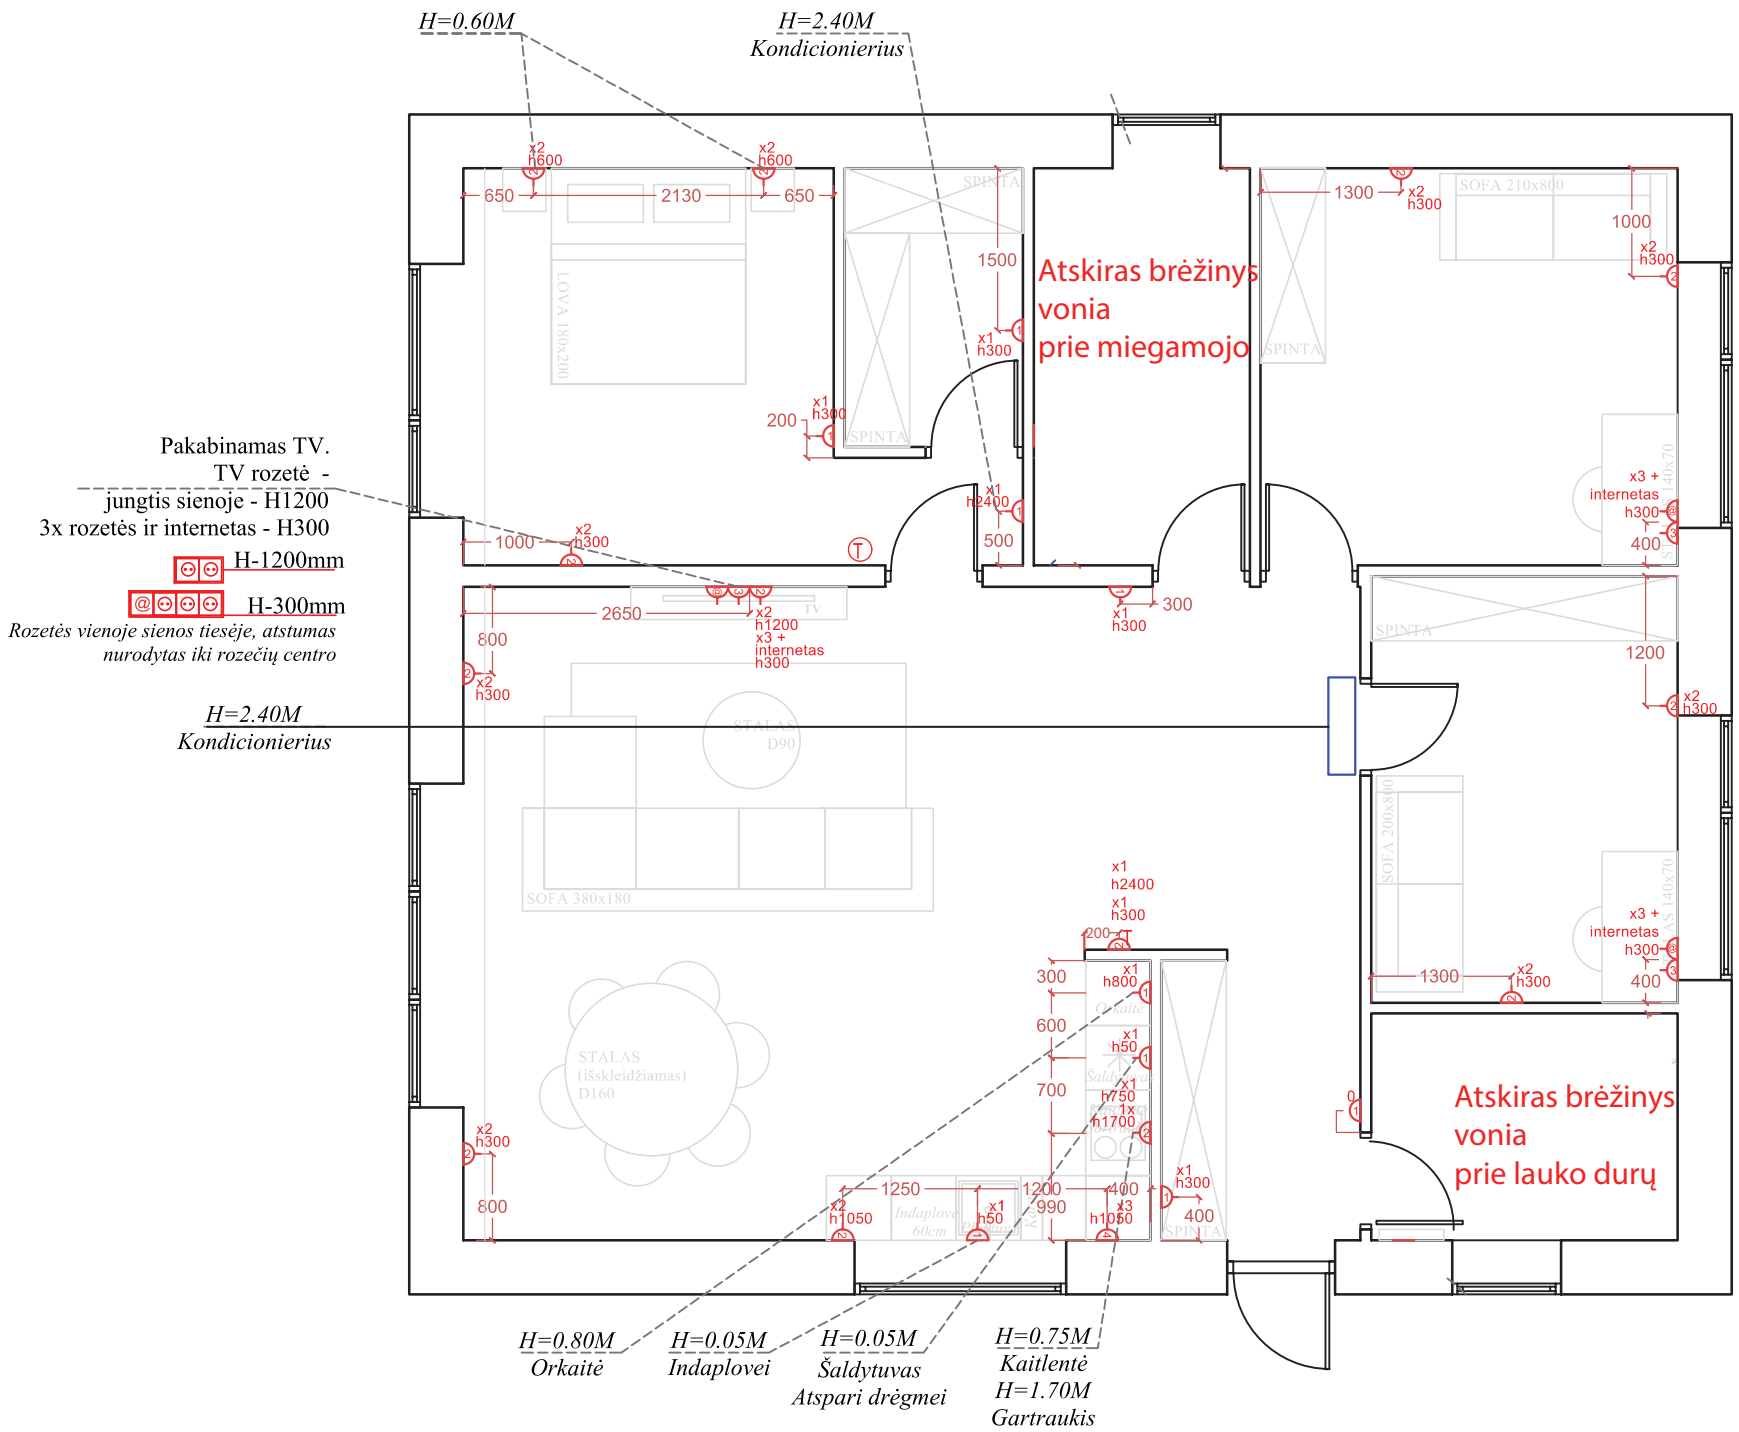

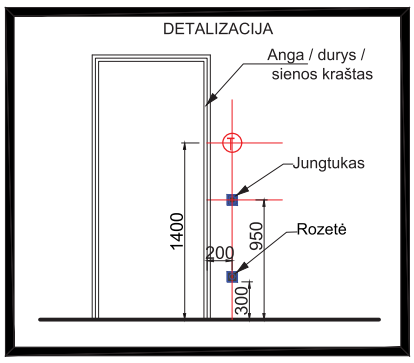

4 2 1 Elektros rozetė ir jų skaičius

@ Interneto lizdas


T Termostatas


PASTABOS:

1. Matmenys pateikti milimetrais, atstumus tikslintis pagal faktą.
2. Altitudės nurodytos metrais, nuo grindų su danga.
3. Matmenis, altitudes ir kiekius tikslinti statybos darbų metu.
4. El. prietaisų ir šviestuvų padėtys gali koreguotis parinkus šviestuvus.
5. Visus plano ir situacijos nesutapimus derinti su užsakovu ir/ar interjero dizaineriu.
6. Rozečių aukštis skaičiuojamas nuo grindų ±0,00 altitudės.

A3 formatas

APIE NAMŲ INTERJERĄ tel. nr. +37067573530 el. paštas: interjeras@apienamus.com				P042_2
Dizainerė	Ieva Juozapaitė	+370 675 73 530	Dokumento žymuo	
Tech. dalis	Miglė Bobinaitė		P042_2025/adresas	
Užsakovas	SIGITA			
ELEKTROS PLANAS Elektros taškų išdėstymo schema			M 1:50	

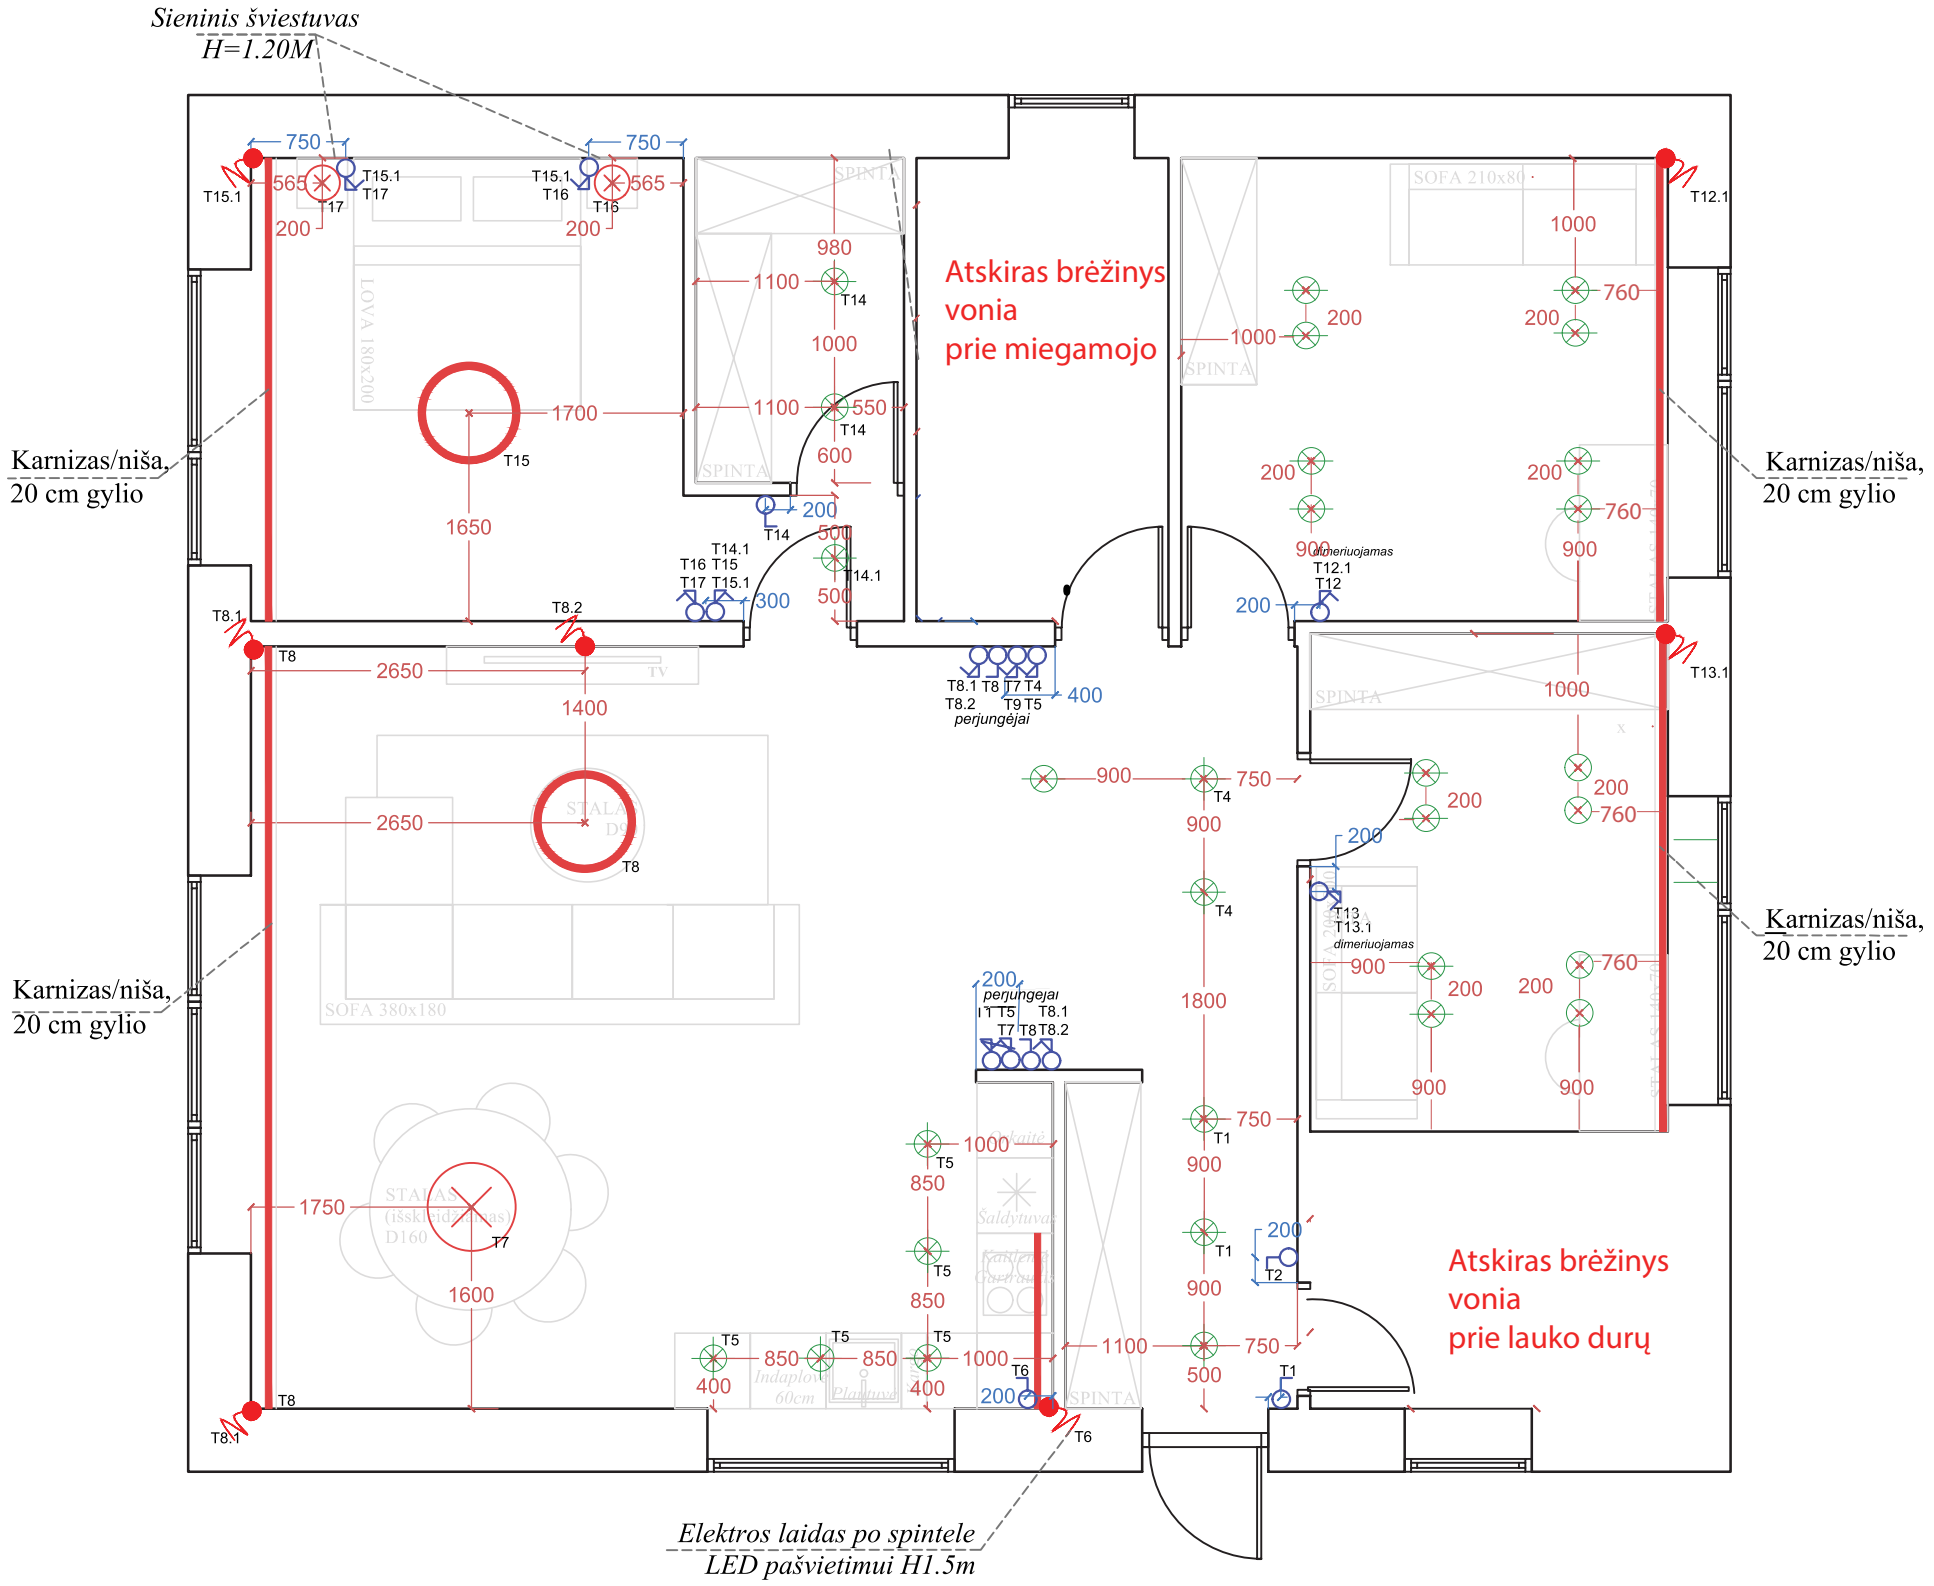

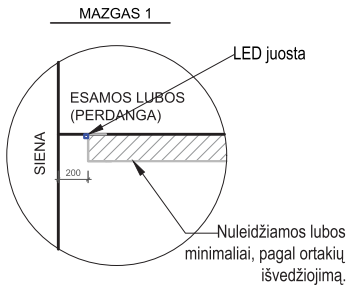

PASTABOS:

1. Matmenys pateikti milimetrais, atstumus tikslintis pagal faktą.
2. Altitudės nurodytos metrais, nuo grindų su danga.
3. Matmenis, altitudes ir kiekius tikslinti statybos darbų metu.
4. El. prietaisų ir šviestuvų padėtys gali koreguotis parinkus šviestuvus.
5. Visus plano ir situacijos nesutapimus derinti su užsakovu ir/ar interjero dizaineriu.
6. Jungiklių aukštis skaičiuojamas nuo grindų ±0,00 altitudės.

	Lubinis šviestuvas
	Sieniniai šviestuvai
	Pakabinamas šviestuvas
	Įmontuojami į lubas viengubi/dvigubi LED lubiniai šviestuvai
	LED juostos
	Dvipolis jungtukas, H=0.95 M, jei nepažymėta kitaip
	Viengubas jungtukas, H=0.95 M, jei nepažymėta kitaip

A3 formatas

APIE NAMŲ INTERJERĄ tel. nr. +37067573530 el. paštas: interjeras@apienamus.com			
Dizainerė	Ieva Juozapaitė	+370 675 73 530	Dokumento žymuo
Tech. dalis	Miglė Bobinaitė		P042_2025/adresas
Užsakovas	SIGITA		
APŠVIETIMO PLANAS Apšvietimo ir jungiklių taškų išdėstymo schema		M 1:50	P042_3