
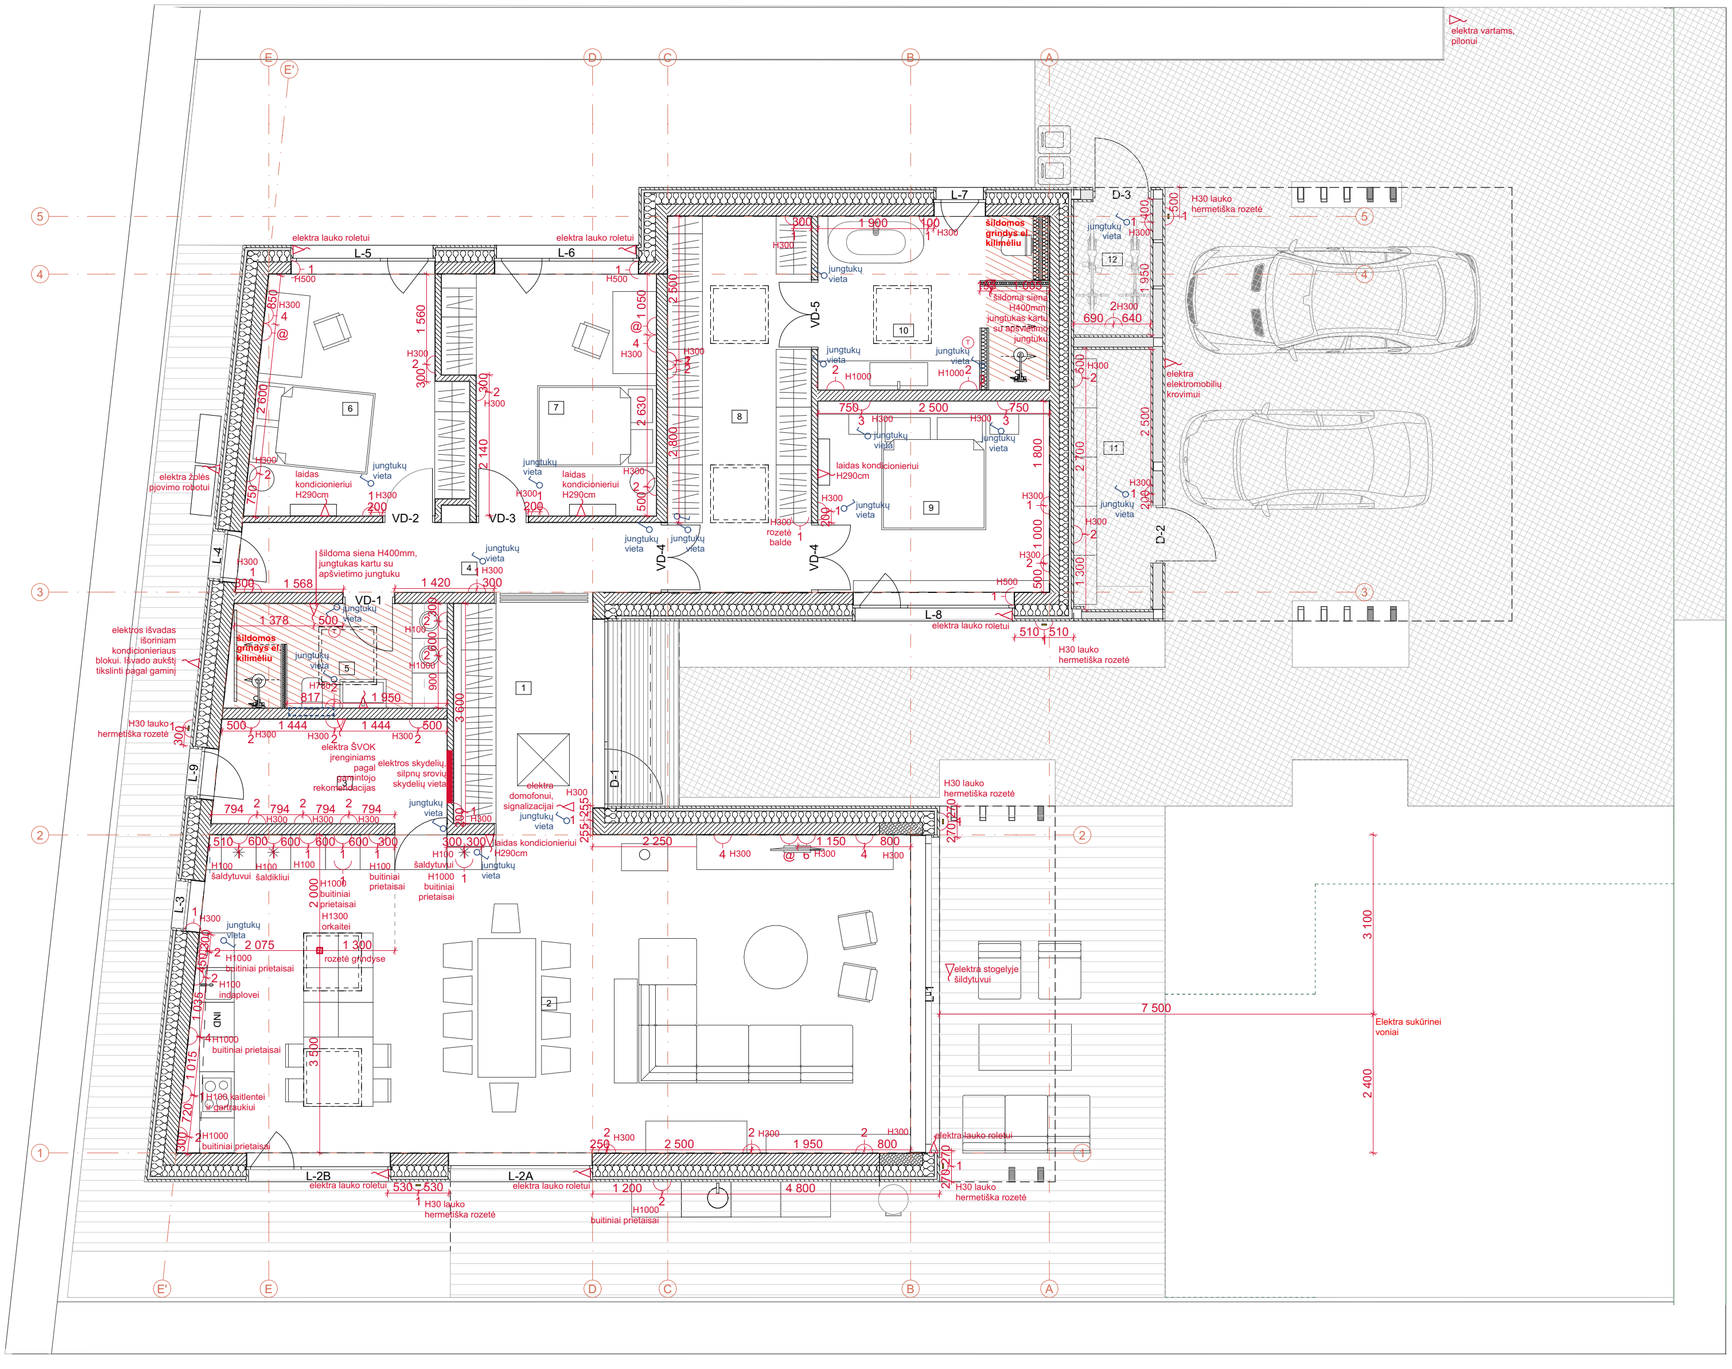


PASTABOS:

1. Prieš gaminių gamybą gamintojas privalo atlikti darbo brėžinius bei juos suderinti su projekto autoriais.
2. Visos naudojamos arba siūlomos naudoti medžiagos turi turėti atitikties sertifikatus ir būti naudojamos pagal tikslinę savo paskirtį.
3. Visos naudojamos medžiagos ir gaminiai turi būti montuojami pagal gamintojo nurodytas instrukcijas, taisykles ir technologiją.
4. 0.00 altitudė duota nuo grindų apdailos paviršiaus
5. Konstrukcijų sprendinius žiūrėti konstrukcijų techniniame darbo projekte.
6. Kad būtų pasiektas skaičiuojamasis garso izoliacijos lygis pertvaros turi dalinti patalpas nuo perdangos iki perdangos, plokštės ir profiliai turi remtis į konstrukcijas taip, kaip nurodo gamintojas, komunikacijų praėjimo vietos turi būti užsandarintos, vadovaujantis gamintojo rekomendacijomis ir normatyviniais dokumentais.
7. Statybos eigoje atsiradus neatitikimams brėžinyje nurodytiems sprendiniams, būtina vykdymo priežiūros metu kreiptis į projekto projektuotoją.
8. Matmenis prieš gaminių gamybą būtina tikslinti vietoje pagal faktą.
9. Visos apdailos medžiagos ir gaminiai prieš užsakant derinamos su projekto autoriais.
10. Brėžinys neskirtas matuoti.

1. Visas rozetes daryti h=20 cm nuo švarių grindų, jei nenurodyta kitaip brėžinyje
2. Visus jungtukus daryti h=100 cm nuo švarių grindų, jei nenurodyta kitaip brėžinyje
3. Visus termostatus h=150 cm nuo švarių grindų, jei nenurodyta kitaip brėžinyje
4. Visi aukščiai duoti nuo švarių grindų alt. 0.00 (įsivertinti grindų dangos storį)
5. Matmenys duoti nuo jungtukų/rozečių/šviestuvų centro
6. Ten, kur sutampa rozečių ir jungtukų vietos, juos lygiuoti vienoje linijoje

Kval. dok. Nr.	aketuri UAB "AKETURI ARCHITEKTAI" RAUDVYKLOS G. 3-1, LT-01140 VILNIUS www.aketuri.lt			Objektas: Vienbutis gyvenamasis namas Šernų g. 18A, Kaunas
	PDV	M. REKEVIČIENĖ	2025-04-10	Dokumento pavadinimas: INTERJERAS
	ARCH	I. MARCINONYTĖ	2025-04-10	
				Brėžinio pavadinimas: LAIDA
				Elektros planas 1
				M 1:75
Kalbos. trump. LT	Statytojas: P.D.			Dokumento žymuo: I109_DP_SA-A.01.4 LAPŲ 1 LAPAI 1

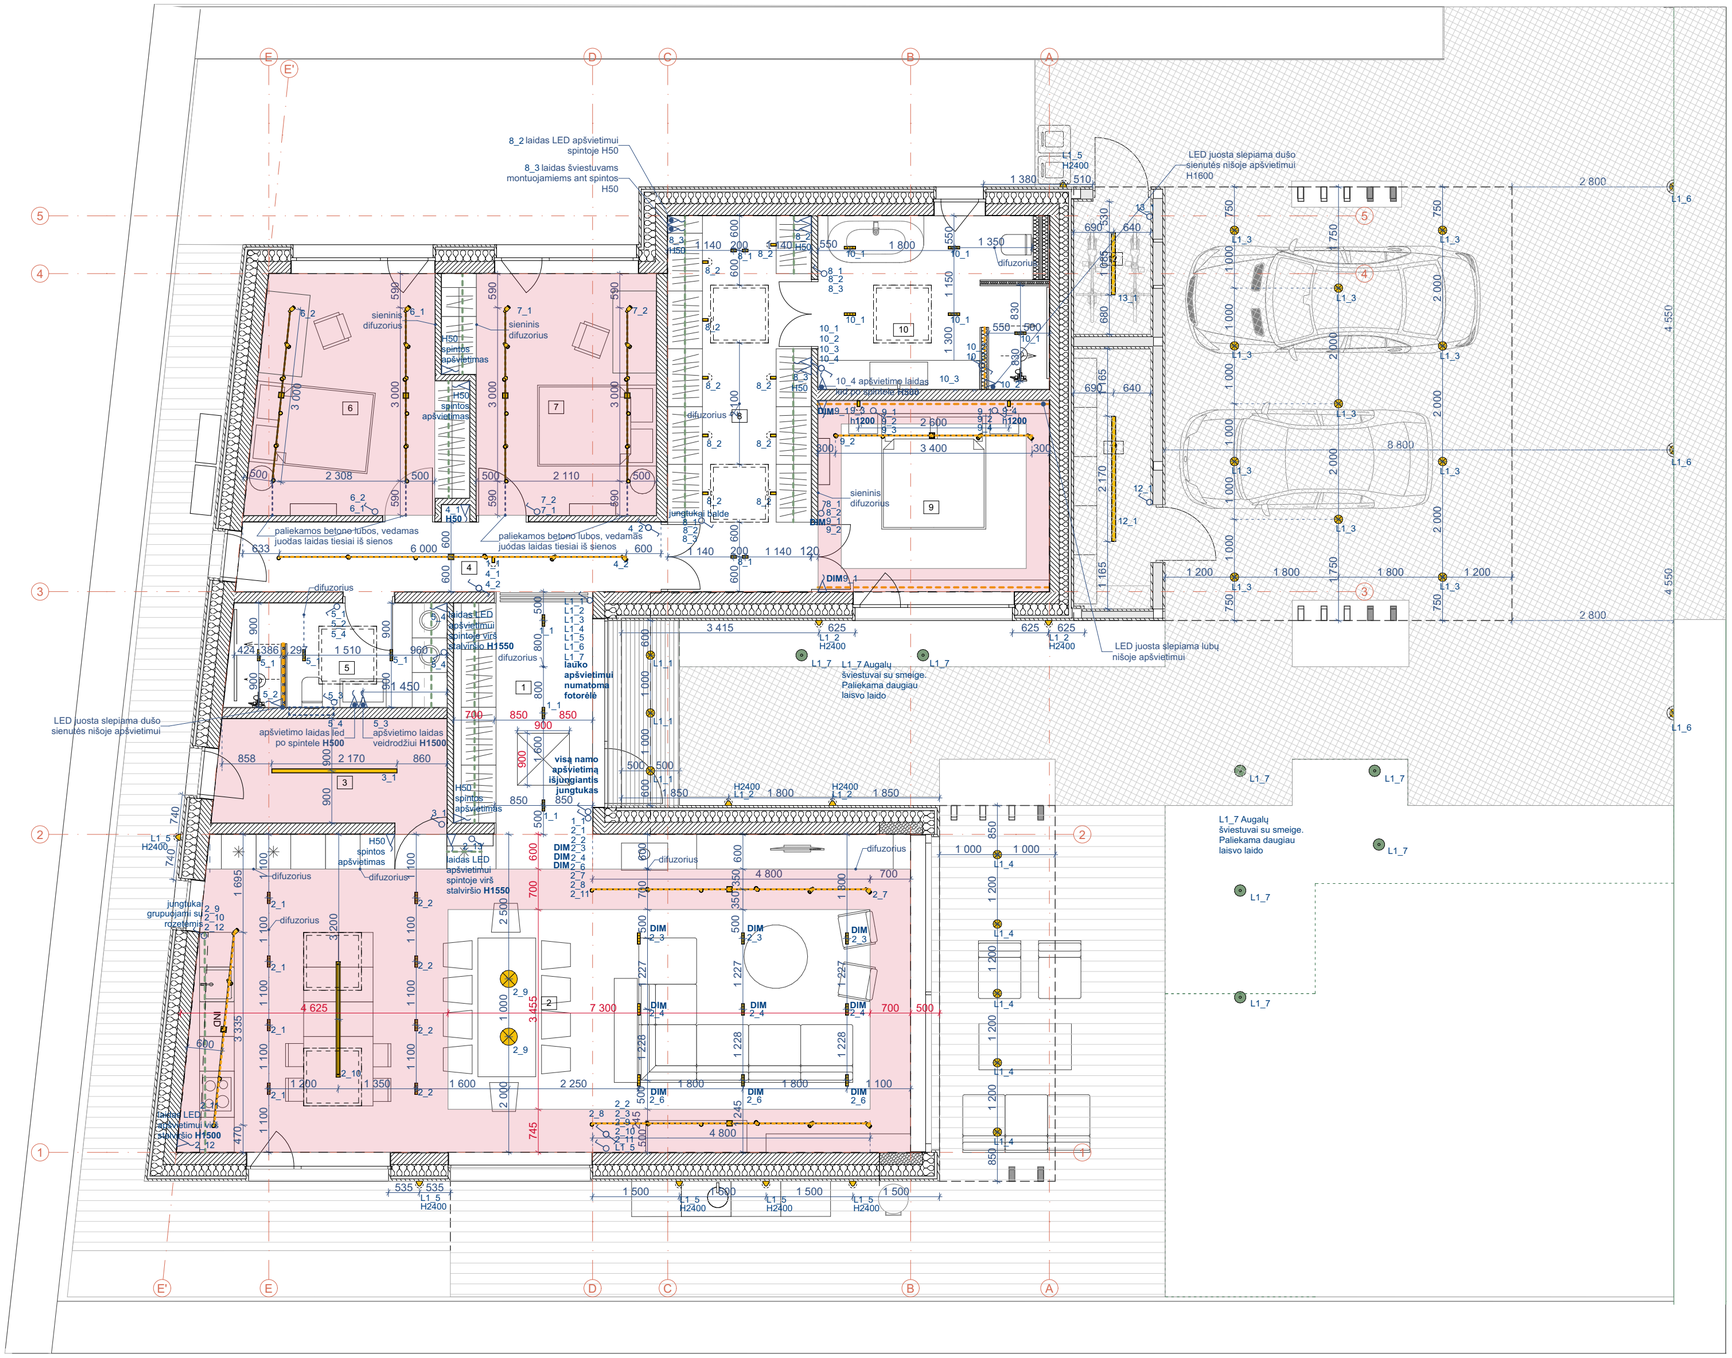

- lauko sieninis šviestuvas
- lauko įleidžiamas šviestuvas
- lubinis šviestuvas pagalbinėse patalpose
- įleidžiamas šviestuvas su integruotu LED
- prožektorius
- įleidžiamas šviestuvas su integruotu LED
- ant drabužinės spintų montuojamas šviestuvas
- bėgelis su prožektoriais
- difuzorius
- jungtukas
- perjungėjas
- šviestuvas, laido vieta lubose
- elektros laido vieta sienoje/ lubose
- termostatas

1. Visas rozetes daryti h=30 cm nuo švarių grindų, jei nenurodyta kitaip brėžinyje
2. Visus jungtukus daryti h=100 cm nuo švarių grindų, jei nenurodyta kitaip brėžinyje
3. Visus termostatus h=150 cm nuo švarių grindų, jei nenurodyta kitaip brėžinyje
4. Visi aukščiai duoti nuo švarių grindų alt. 0.00 (įsivertinti grindų dangos storį)
5. Matmenys duoti nuo jungtukų/rozečių/šviestuvų centro
6. Ten, kur sutampa rozečių, termostatų, jungtukų vietos - juos lygiuoti vienoje linijoje

PASTABOS:

1. Prieš gaminių gamybą gamintojas privalo atlikti darbo brėžinius bei juos suderinti su projekto autoriais.
2. Visos naudojamos arba siūlomos naudoti medžiagos turi turėti atitikties sertifikatus ir būti naudojamos pagal tikslinę savo paskirtį.
3. Visos naudojamos medžiagos ir gaminiai turi būti montuojami pagal gamintojo nurodytas instrukcijas, taisykles ir technologiją.
4. 0.00 altitudė duota nuo grindų apdailos paviršiaus
5. Konstrukcijų sprendinius žiūrėti konstrukcijų techniniame darbo projekte.
6. Kad būtų pasiektas skaičiuojamasis garso izoliacijos lygis pertvaros turi dalinti patalpas nuo perdangos iki perdangos, plokštės ir profiliai turi remtis į konstrukcijas taip, kaip nurodo gamintojas, komunikacijų praėjimo vietos turi būti užsandarintos, vadovaujantis gamintojo rekomendacijomis ir normatyviniais dokumentais.
7. Statybos eigoje atsiradus neatitikimams brėžinyje nurodytiems sprendiniams, būtina vykdymo priežiūros metu kreiptis į projekto projektuotoją.
8. Matmenis prieš gaminių gamybą būtina tikslinti vietoje pagal faktą.
9. Visos apdailos medžiagos ir gaminiai prieš užsakant derinamos su projekto autoriais.
10. Brėžinys neskirtas matuoti.

Kval. dok. Nr.	aketuri UAB "AKETURI ARCHITEKTAI" RAUGYKLOS G. 3-1, LT-01140 VILNIUS www.aketuri.lt				Objektas: Vienbutis gyvenamasis namas Šernų g. 18A, Kaunas
	PDV	M. REKEVIČIENĖ		2025-04-10	Dokumento pavadinimas: INTERJERAS
	ARCH	I. MARCINONYTĖ		2025-04-10	
					Brėžinio pavadinimas: **Apšvietimo planas su ŠVOK įrenginių vietomis** **M 1:75**
					LAIDA: 1
Kalbos. trump. LT	Statytojas: P.D.				Dokumento žymuo: I109_DP_SA-A.01.6
					LAPŲ: 1 / LAPAI: 1