



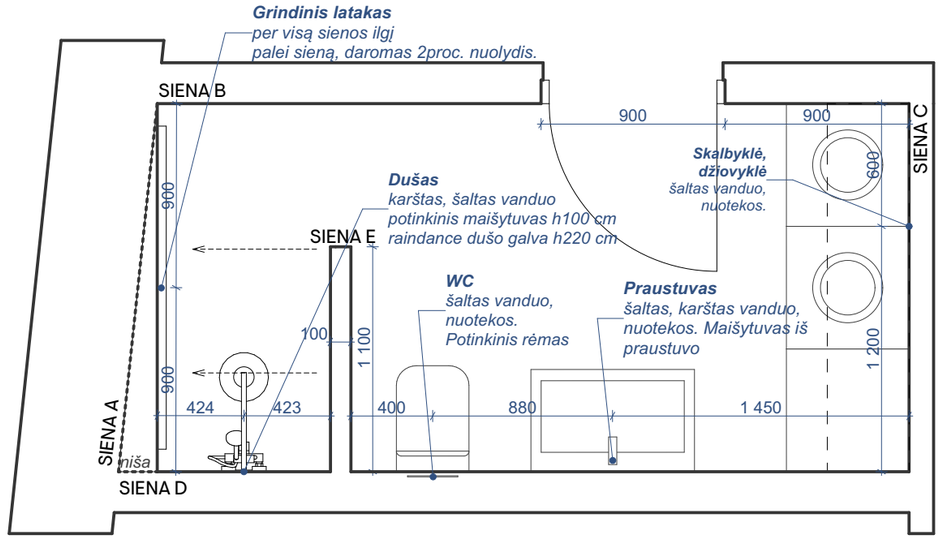


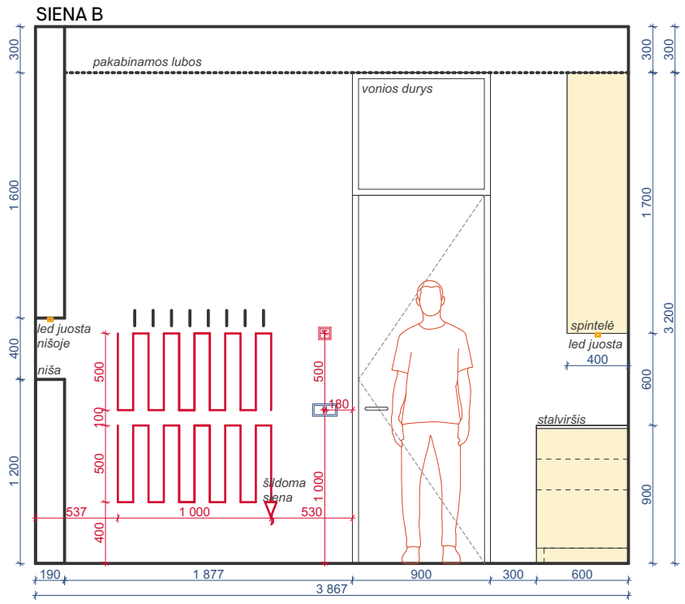

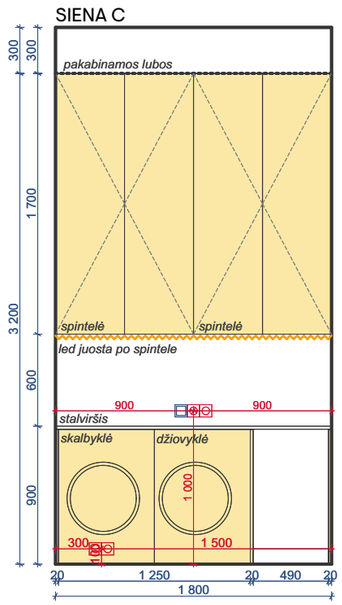


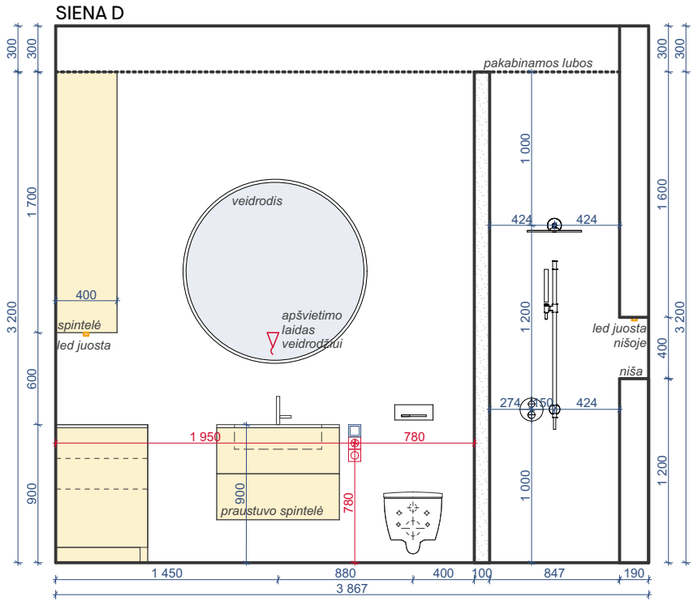

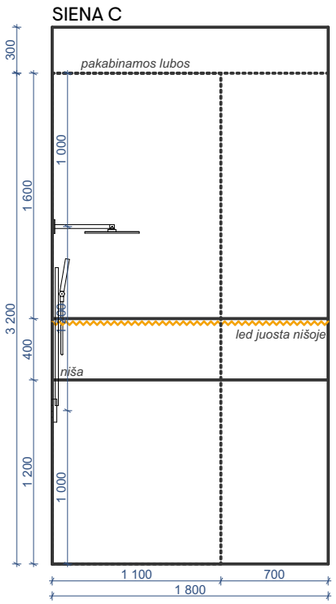


Kval. dok. Nr.	aketuri UAB "AKETURI ARCHITEKTAI" RAUGYKLOS G. 3-1, LT-01140 VILNIUS, LIETUVA +370 612 16112 info@aketuriarchitektai.lt www.aketuriarchitektai.lt				Objektas: Vienbutis gyvenamasis namas Šernų g. 18A, Vilnius
	PDV	M. REKEVIČIENĖ		2025-04-02	Dokumento pavadinimas:
	ARCH	I. MARCINONYTĖ		2025-04-02	STATINIO ARCHITEKTŪROS DALIS
	ARCH	E. MAZGELYTĖ		2025-04-02	Brėžinio pavadinimas: **Vaikų san. mazgo išklotinės** **M 1:30, 1:40** — LAIDA: 1
Kalbos. trump. LT	Statytojas: P.D.				Dokumento žymuo: A129_DP_SA-A.01.11 — LAPŲ: 1 — LAPAI: 1


SIENA A

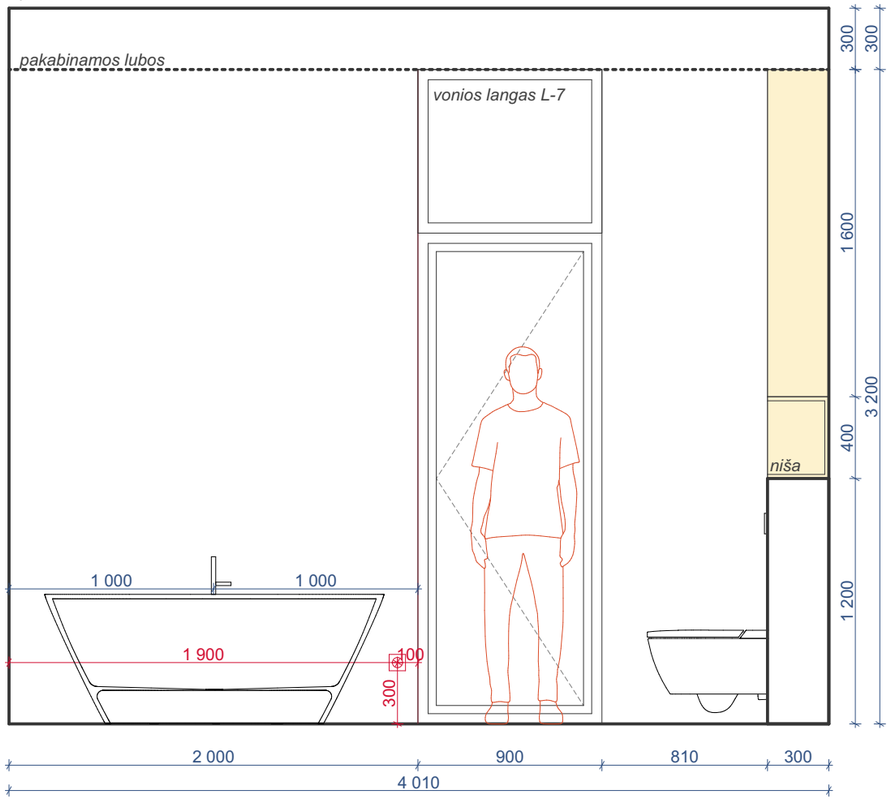


SIENA D

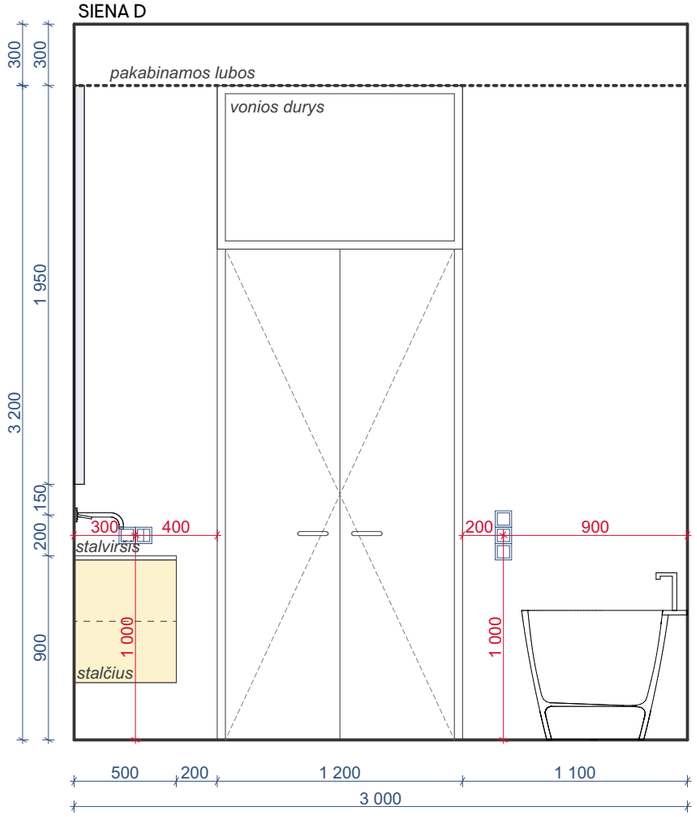


SIENA E

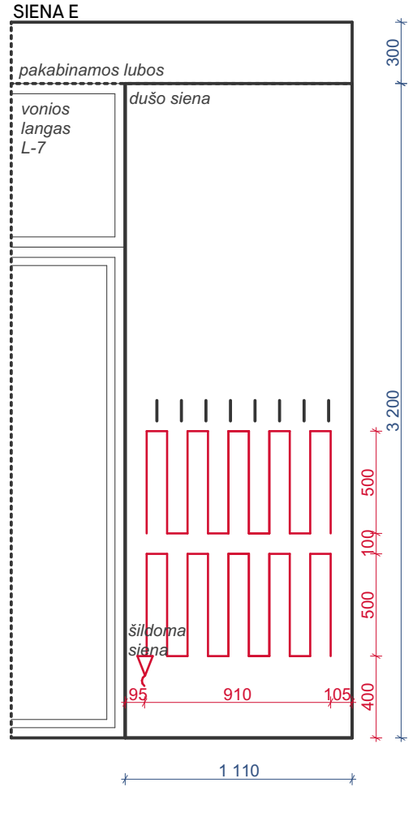

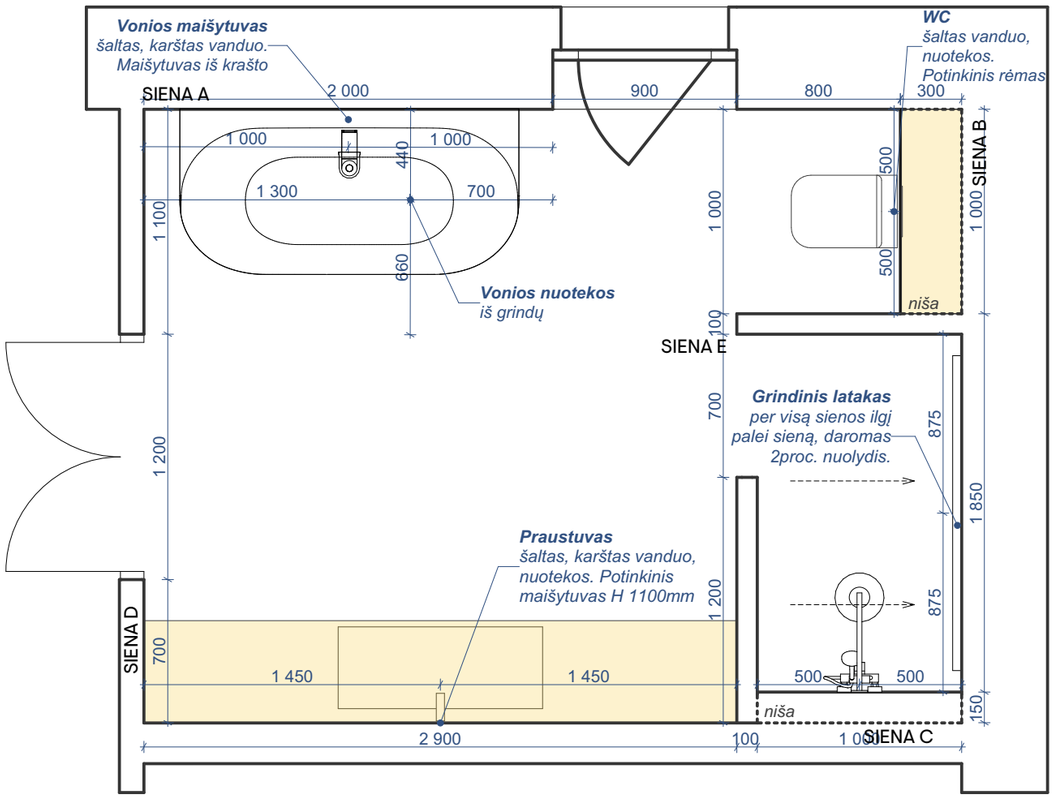


Kval. dok. Nr.	aketuri UAB "AKETURI ARCHITEKTAI" RAUGYKLOS G. 3-1, LT-01140 VILNIUS, LIETUVA +370 612 16112 info@aketuriarchitektai.lt www.aketuriarchitektai.lt				Objektas: Vienbutis gyvenamasis namas Šernų g. 18A, Vilnius
	PDV	M. REKEVIČIENĖ		2025-04-02	Dokumento pavadinimas: STATINIO ARCHITEKTŪROS DALIS
	ARCH	I. MARCINONYTĖ		2025-04-02	
	ARCH	E. MAZGELYTĖ		2025-04-02	Brėžinio pavadinimas: **Tėvų san. mazgo išklotinės** **M 1:30** — LAIDA: 1
Kalbos. trump. LT	Statytojas: P.D.				Dokumento žymuo: A129_DP_SA-A.01.12 — LAPŲ: 1 — LAPAI: 1


SIENA B

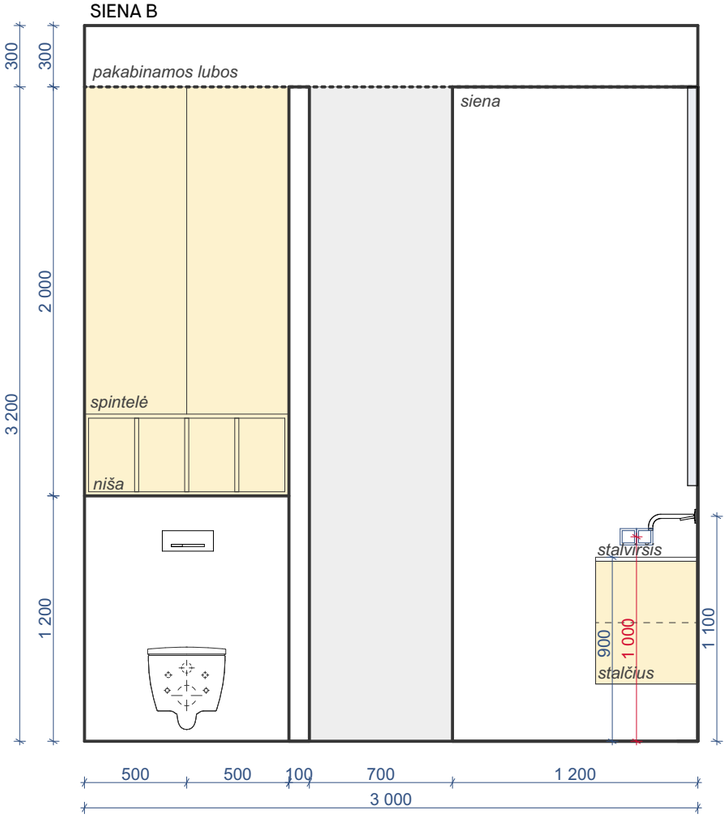

SIENA C

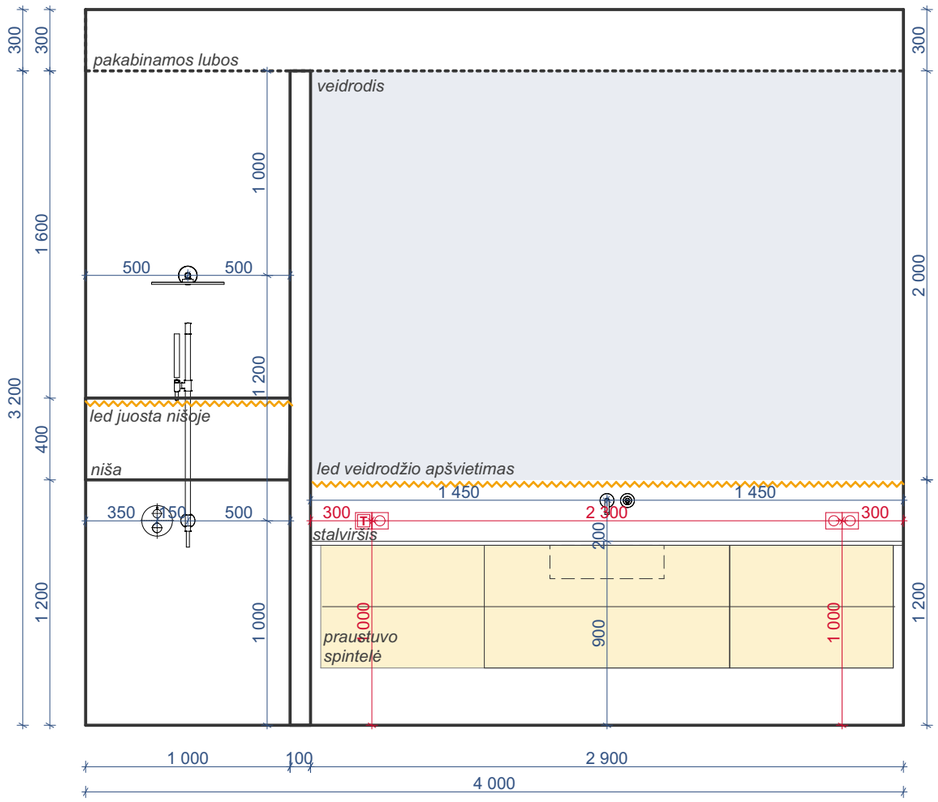

Kval. dok. Nr.	aketuri UAB "AKETURI ARCHITEKTAI" RAUGYKLOS G. 3-1, LT-01140 VILNIUS, LIETUVA +370 612 16112 info@aketuriarchitektai.lt www.aketuriarchitektai.lt				Objektas: Vienbutis gyvenamasis namas Šernų g. 18A, Vilnius
	PDV	M. REKEVIČIENĖ		2025-04-02	Dokumento pavadinimas: STATINIO ARCHITEKTŪROS DALIS
	ARCH	I. MARCINONYTĖ		2025-04-02	
	ARCH	E. MAZGELYTĖ		2025-04-02	Brėžinio pavadinimas: **Tėvų san. mazgo išklotinės** **M 1:30** — LAIDA: 1
Kalbos. trump. LT	Statytojas: P.D.				Dokumento žymuo: A129_DP_SA-A.01.13 — LAPŲ: 1 — LAPAI: 1

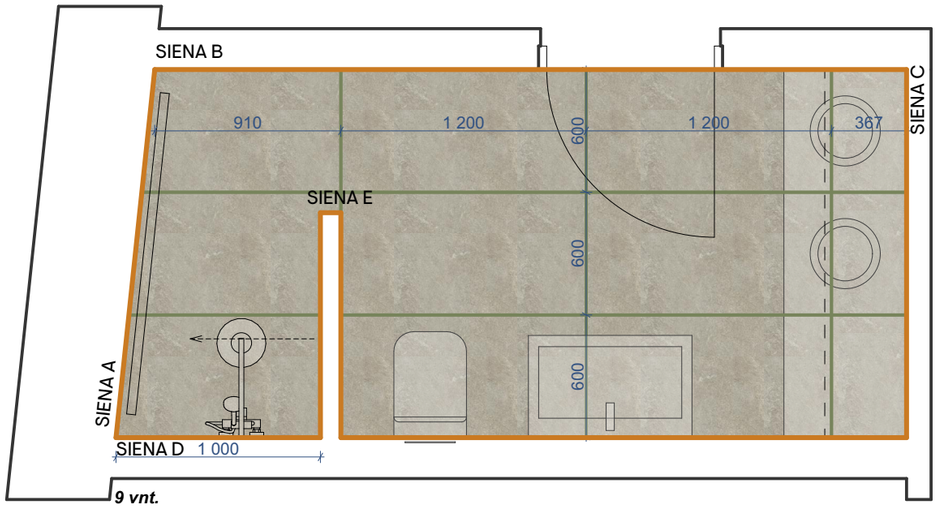

9 vnt.




GRINDŲ IR SIENŲ DANGA

Italgraniti Orgins Taupe 600x1200mm.


grindys 9 vnt.
sienos 58 vnt.

Kiekis: 67vnt.


Sienų danga- plytelės

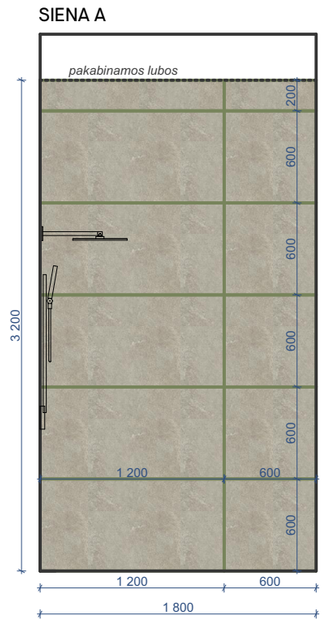


9 vnt.

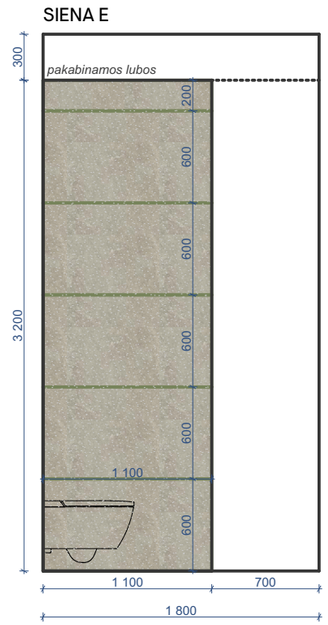


5 vnt.

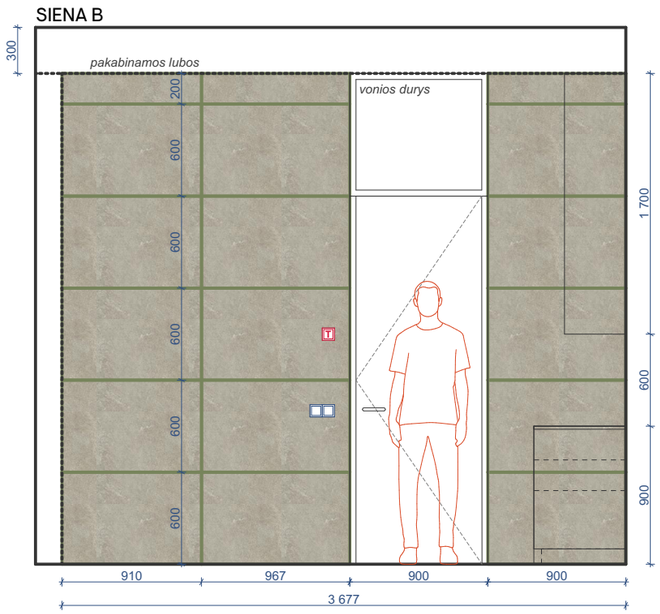


16 vnt.

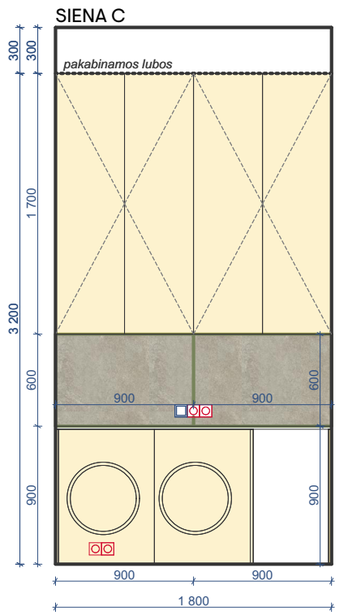

2 vnt.

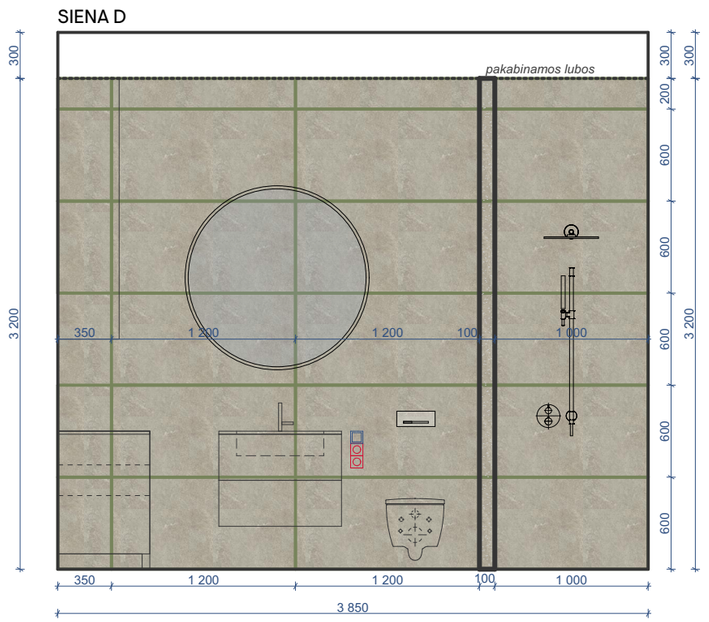


20 vnt.

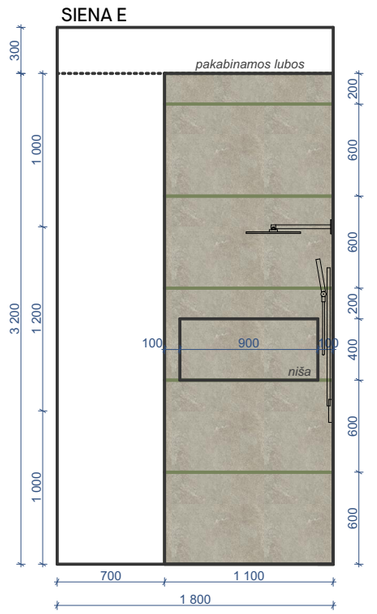

6 vnt.


Kval. dok. Nr.	aketuri UAB "AKETURI ARCHITEKTAI" RAUGYKLOS G. 3-1, LT-01140 VILNIUS, LIETUVA +370 612 16112 info@aketuriarchitektai.lt www.aketuriarchitektai.lt				Objektas: Vienbutis gyvenamasis namas Šernų g. 18A, Vilnius
	PDV	M. REKEVIČIENĖ		2025-04-02	Dokumento pavadinimas:
	ARCH	I. MARCINONYTĖ		2025-04-02	STATINIO ARCHITEKTŪROS DALIS
	ARCH	E. MAZGELYTĖ		2025-04-02	Brėžinio pavadinimas: **Vaikų san. mazgo išklotinės plytelės** **M 1:40, 1:30** — LAIDA: 1
Kalbos. trump. LT	Statytojas: P.D.				Dokumento žymuo: A129_DP_SA-A.01.14 — LAPŲ: 1 — LAPAI: 1

SIENA A

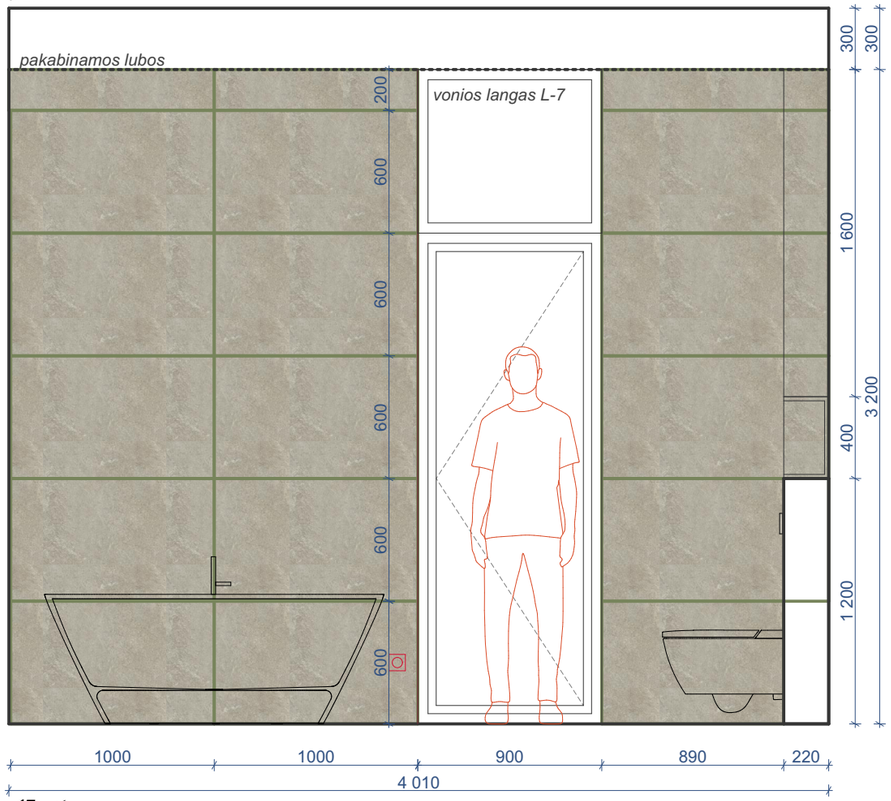


17 vnt.

SIENA D

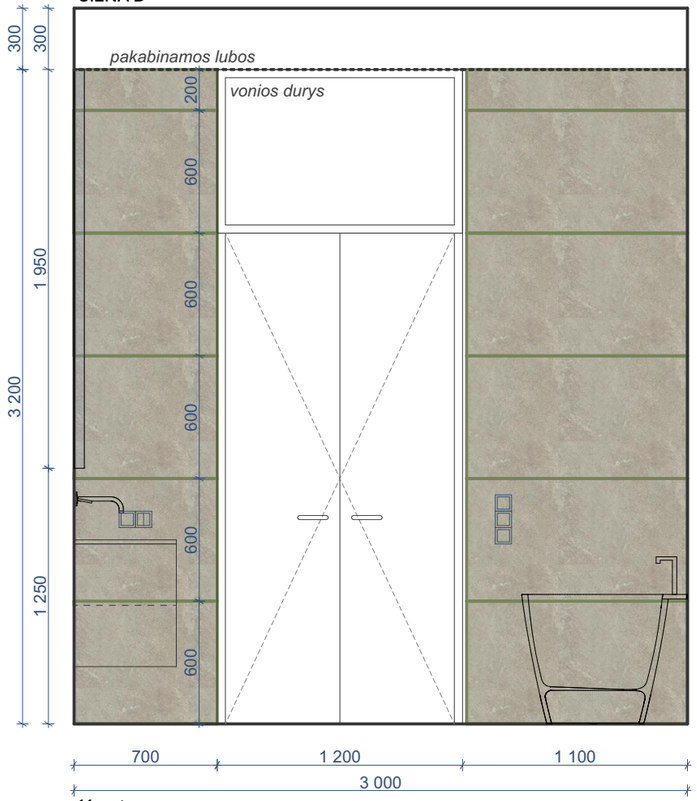


11 vnt.

SIENA E

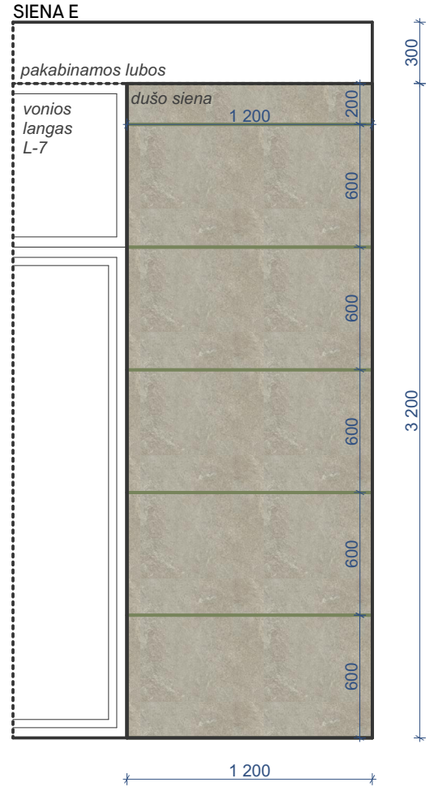

10 vnt.

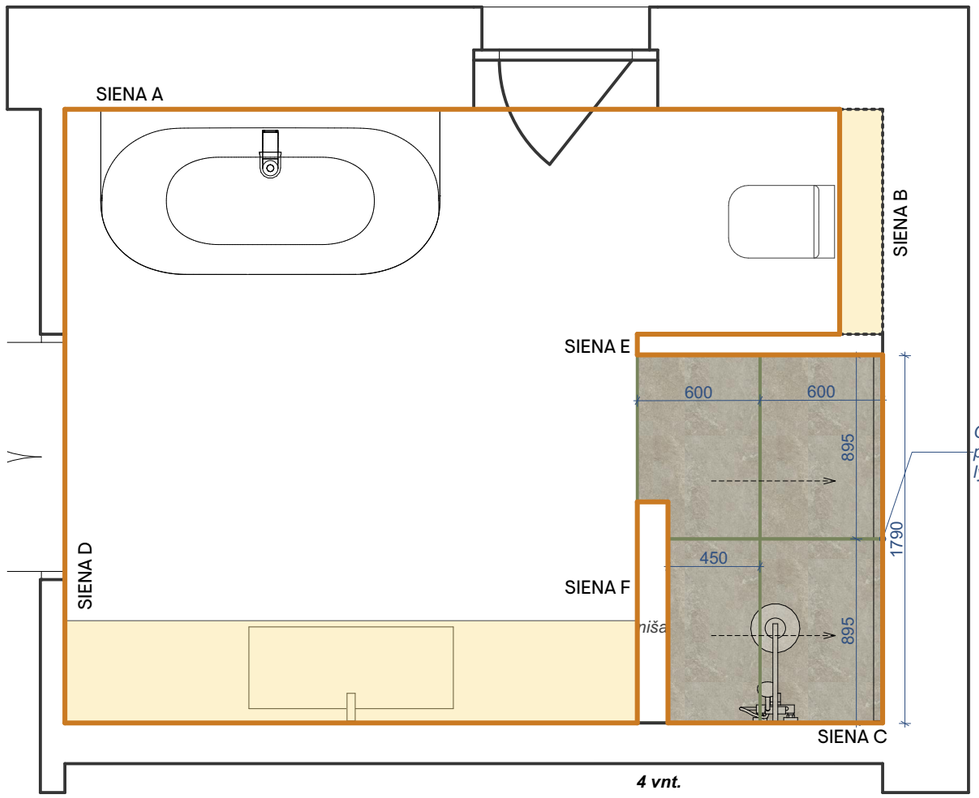

Grindų bei sienų plytelių siūlės yra lygiuojamos.



GRINDŲ IR SIENŲ DANGA

Italgraniti Orgins Taupe 600x1200mm.

grindys 4 vnt.
sienos 73 vnt.


Kiekis: 77 vnt.

Sienų danga- plytelės

Kval. dok. Nr.	aketuri UAB "AKETURI ARCHITEKTAI" RAUGYKLOS G. 3-1, LT-01140 VILNIUS, LIETUVA +370 612 16112 info@aketuriarchitektai.lt www.aketuriarchitektai.lt				Objektas: Vienbutis gyvenamasis namas Šernų g. 18A, Vilnius
	PDV	M. REKEVIČIENĖ		2025-04-02	Dokumento pavadinimas: STATINIO ARCHITEKTŪROS DALIS
	ARCH	I. MARCINONYTĖ		2025-04-02	
	ARCH	E. MAZGELYTĖ		2025-04-02	Brėžinio pavadinimas: **Tėvų san. mazgo išklotinės plytelės** **M 1:30, 1:40** — LAIDA: 1
Kalbos. trump. LT	Statytojas: P.D.				Dokumento žymuo: A129_DP_SA-A.01.15 — LAPŲ: 1 — LAPAI: 1


SIENA B

13 vnt.

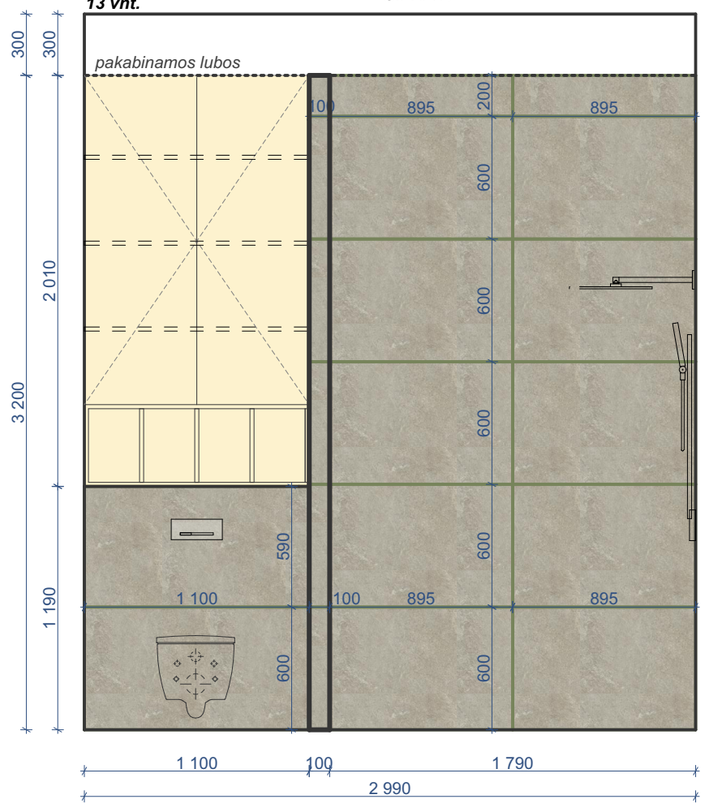


SIENA C

11 vnt.

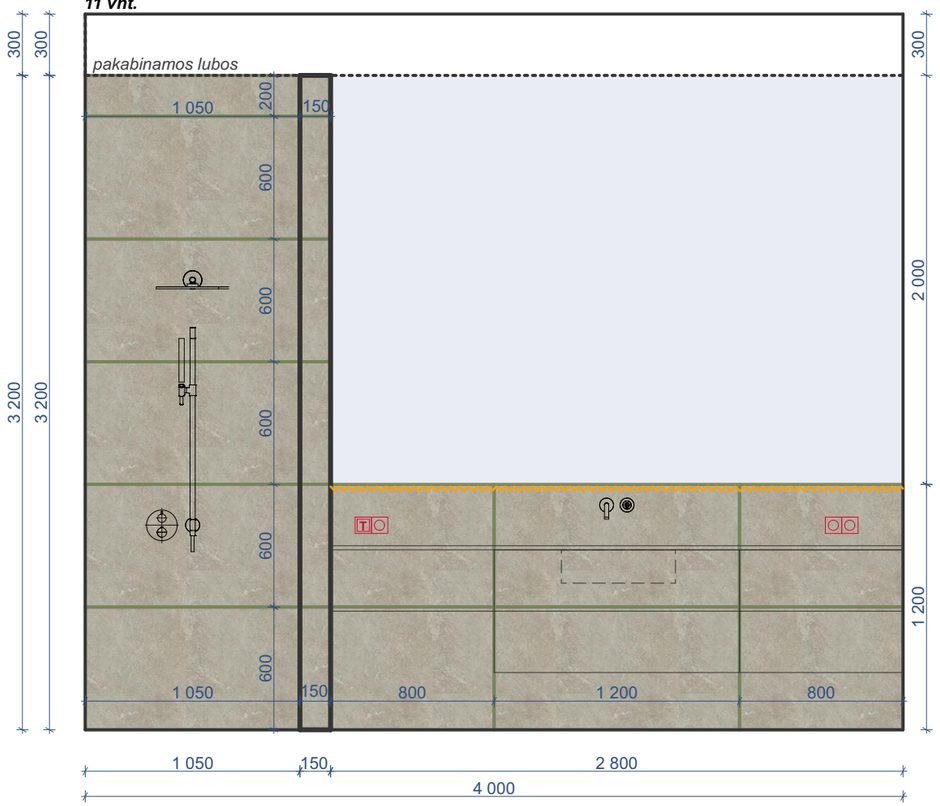


SIENA F

5 vnt.

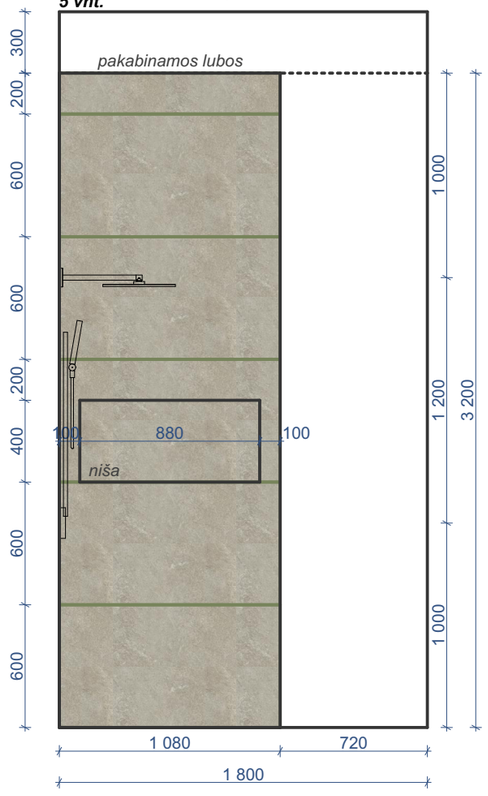

SIENA F

6 vnt.

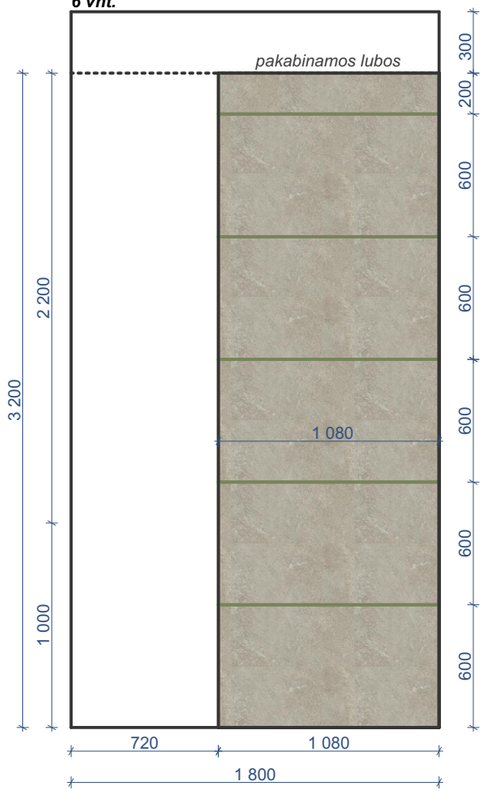



GRINDŲ IR SIENŲ DANGA


Italgraniti Orgins Taupe 600x1200mm.

grindys 4 vnt.
sienos 73 vnt.

Kiekis: 77 vnt.

Sienų danga- plytelės

Kval. dok. Nr.	aketuri UAB "AKETURI ARCHITEKTAI" RAUGYKLOS G. 3-1, LT-01140 VILNIUS, LIETUVA +370 612 16112 info@aketuriarchitektai.lt www.aketuriarchitektai.lt				Objektas: Vienbutis gyvenamasis namas Šernų g. 18A, Vilnius
	PDV	M. REKEVIČIENĖ		2025-04-02	Dokumento pavadinimas: STATINIO ARCHITEKTŪROS DALIS
	ARCH	I. MARCINONYTĖ		2025-04-02	
	ARCH	E. MAZGELYTĖ		2025-04-02	Brėžinio pavadinimas: **Tėvų san. mazgo išklotinės plytelės** **M 1:30, 1:40** — LAIDA: 1
Kalbos. trump. LT	Statytojas: P.D.				Dokumento žymuo: A129_DP_SA-A.01.16 — LAPŲ: 1 — LAPAI: 1

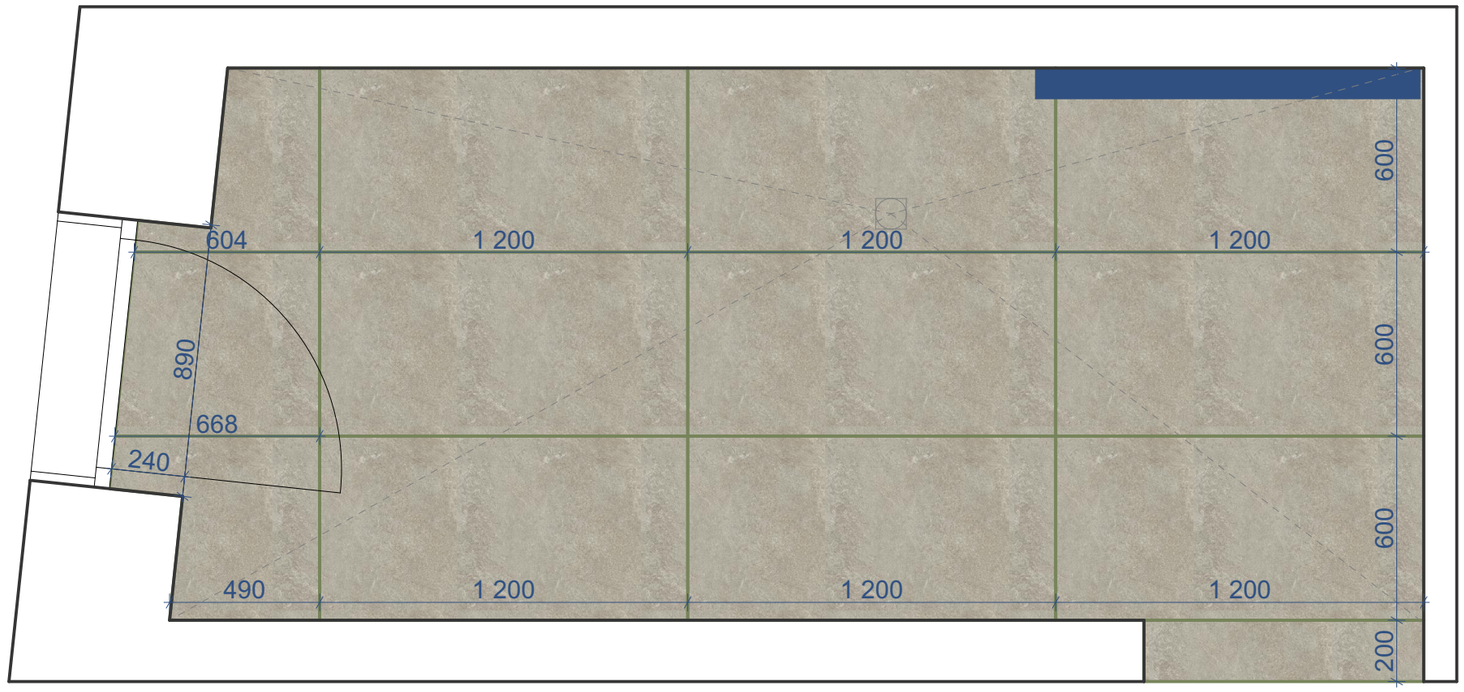



GRINDŲ DANGA

Italgraniti Orgins Taupe 600x1200mm.

Kiekis: 11 vnt.

Kval. dok. Nr.	aketuri UAB "AKETURI ARCHITEKTAI" RAUGYKLOS G. 3-1, LT-01140 VILNIUS, LIETUVA +370 612 16112 info@aketuriarchitektai.lt www.aketuriarchitektai.lt				Objektas: Vienbutis gyvenamasis namas Šernų g. 18A, Vilnius	
	PDV	M. REKEVIČIENĖ		2025-04-02	Dokumento pavadinimas: STATINIO ARCHITEKTŪROS DALIS	
	ARCH	I. MARCINONYTĖ		2025-04-02		
	ARCH	E. MAZGELYTĖ		2025-04-02	Brėžinio pavadinimas: **Techninės patalpos grindų dangos planas** **M 1:20**	LAIDA 1
Kalbos. trump. LT	Statytojas: P.D.				Dokumento žymuo: A129_DP_SA-A.01.17	LAPŲ 1 / LAPAI 1