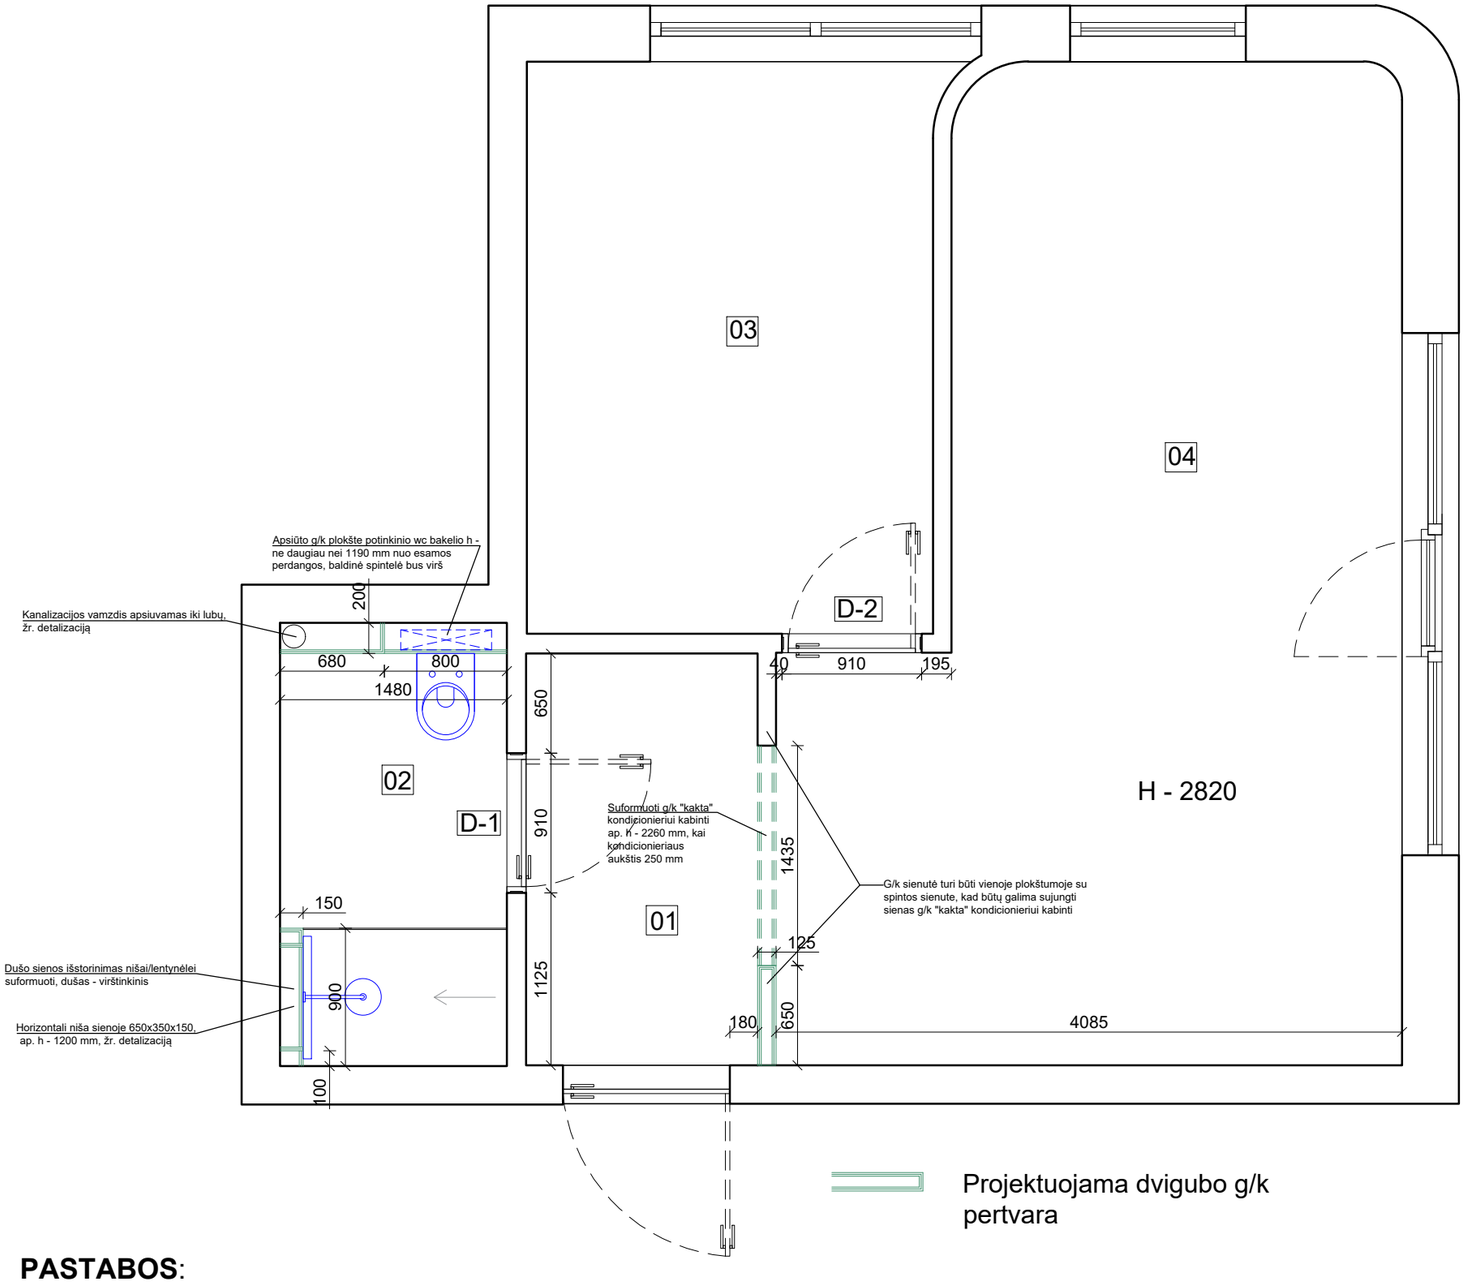


Patalpų eksplikacija	
01. Įėjimo koridorius	4.05 m²
02. San. mazgas	4.00 m²
03. Miegamasis	10.21 m²
04. Virtuvė/svetainė	23.02 m²
Bendras plotas:	41.28 m²

Vidinių angų (durų) žiniaraštis

Kodas	Angos plotis, mm	Angos aukštis, mm	Pertvaros plotis, mm	Durų atidarymo kryptis, tipas
D-1	910	2100	125+15*	Dešininės, beapvadinės
D-2	910	2100	125	Kairinės, beapvadinės, atvirkštinio varstymo

* Akmens masės plytelių apdaila (15 mm) iš san. mazgo vidinės pusės

PASTABOS:

1. Durų staktas ruošti beapvadinėms durims: lyginti, glaistyti, dažyti.

Naujai montuojamų g/k pertvarų planas. M 1:40

Interjero dizainerė Marija Orlovienė, +370 620 81230, marija@strix.studio