
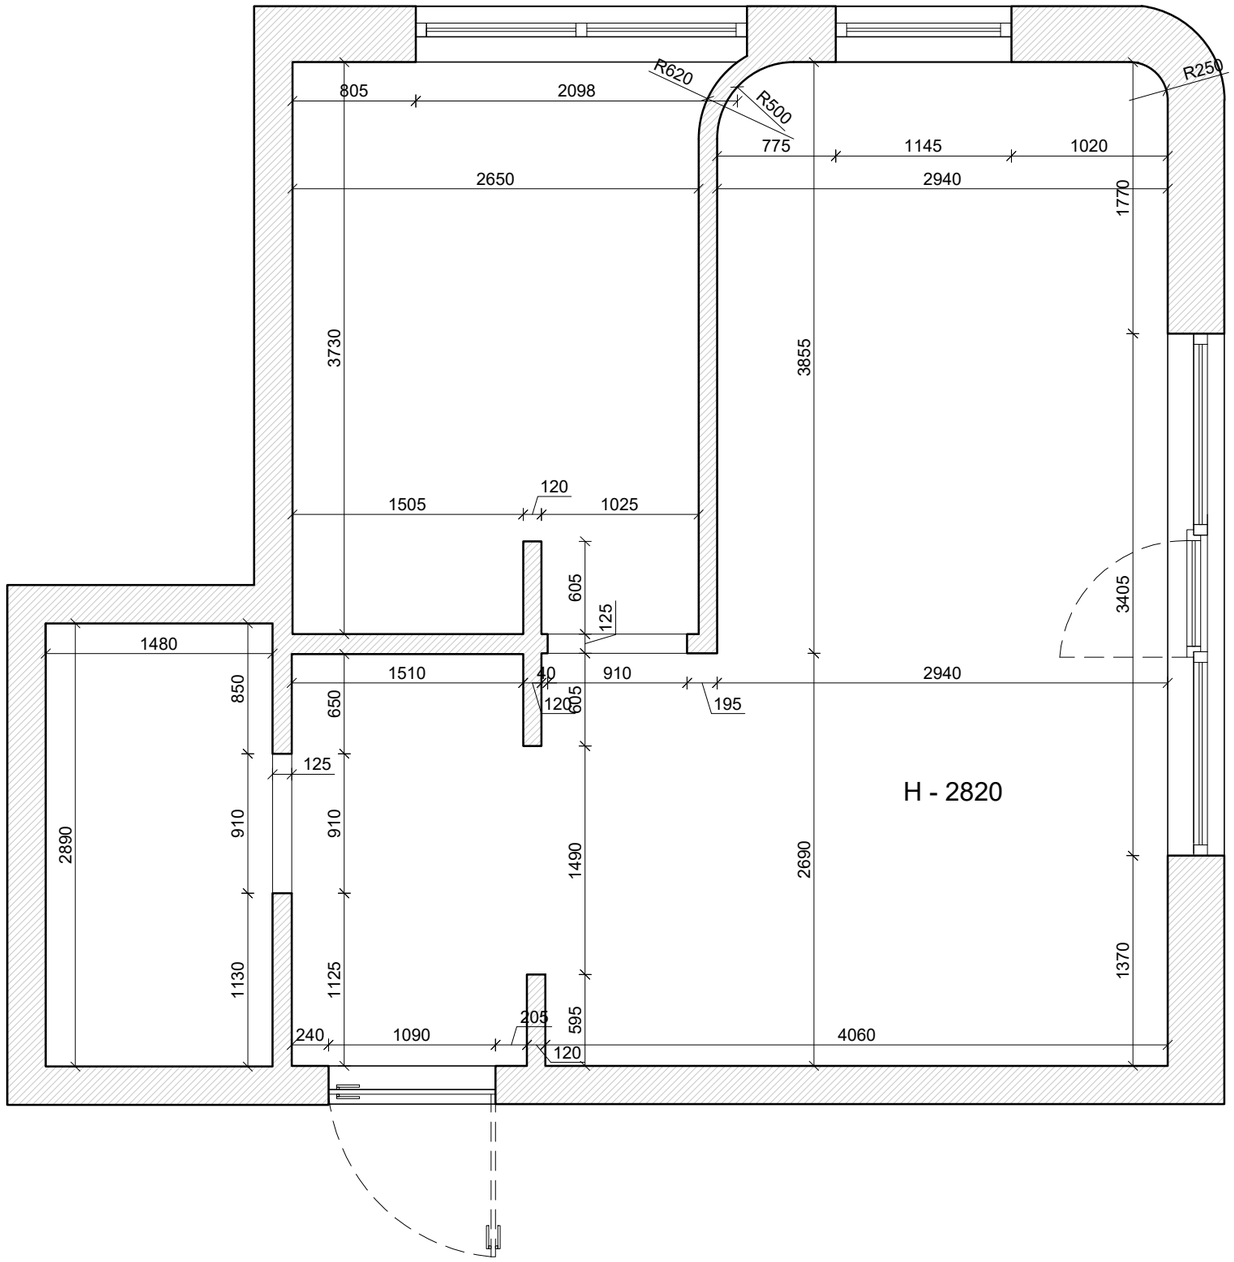


APMATAVIMAI. M 1:40

Interjero dizainerė Marija Orlovienė, +370 620 81230, marija@strix.studio

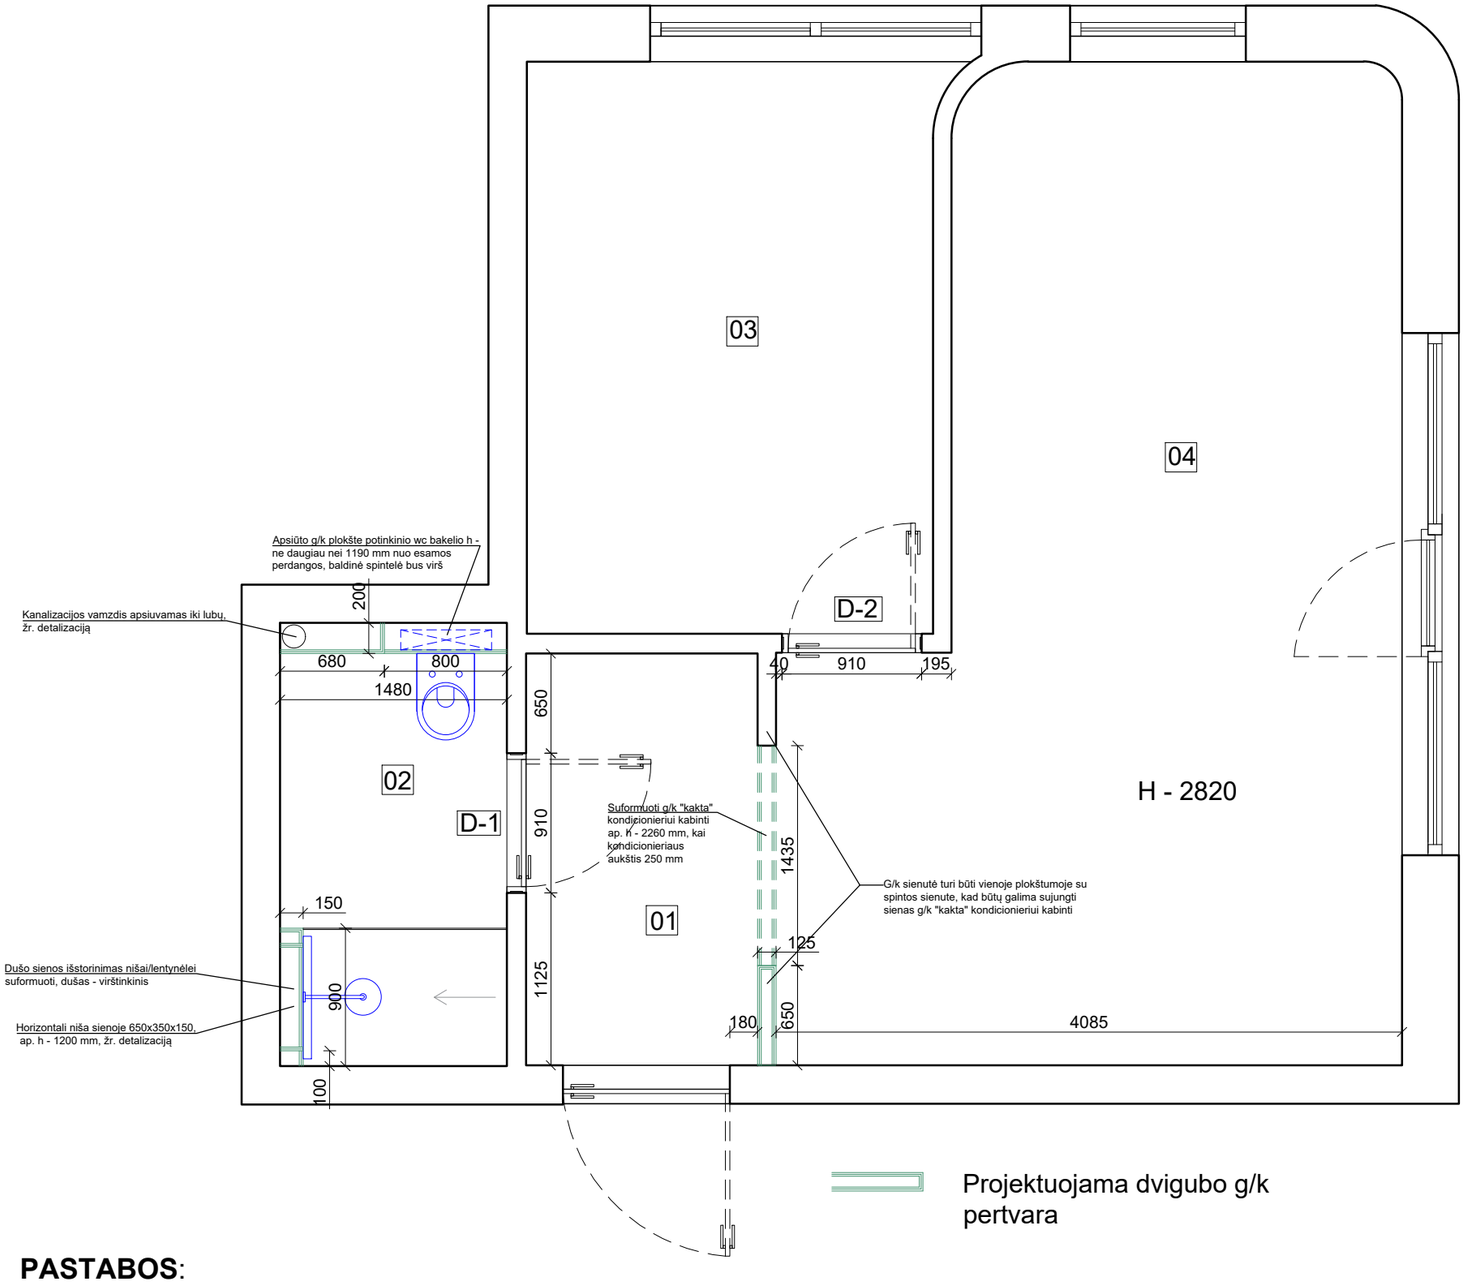

Patalpų eksplikacija	
01. Įėjimo koridorius	4.05 m²
02. San. mazgas	4.00 m²
03. Miegamasis	10.21 m²
04. Virtuvė/svetainė	23.02 m²
Bendras plotas:	41.28 m²

Vidinių angų (durų) žiniaraštis

Kodas	Angos plotis, mm	Angos aukštis, mm	Pertvaros plotis, mm	Durų atidarymo kryptis, tipas
D-1	910	2100	125+15*	Dešininės, beapvadinės
D-2	910	2100	125	Kairinės, beapvadinės, atvirkštinio varstymo


* Akmens masės plytelių apdaila (15 mm) iš san. mazgo vidinės pusės

PASTABOS:

1. Durų staktas ruošti beapvadinėms durims: lyginti, glaistyti, dažyti.

Naujai montuojamų g/k pertvarų planas. M 1:40

Interjero dizainerė Marija Orlovienė, +370 620 81230, marija@strix.studio

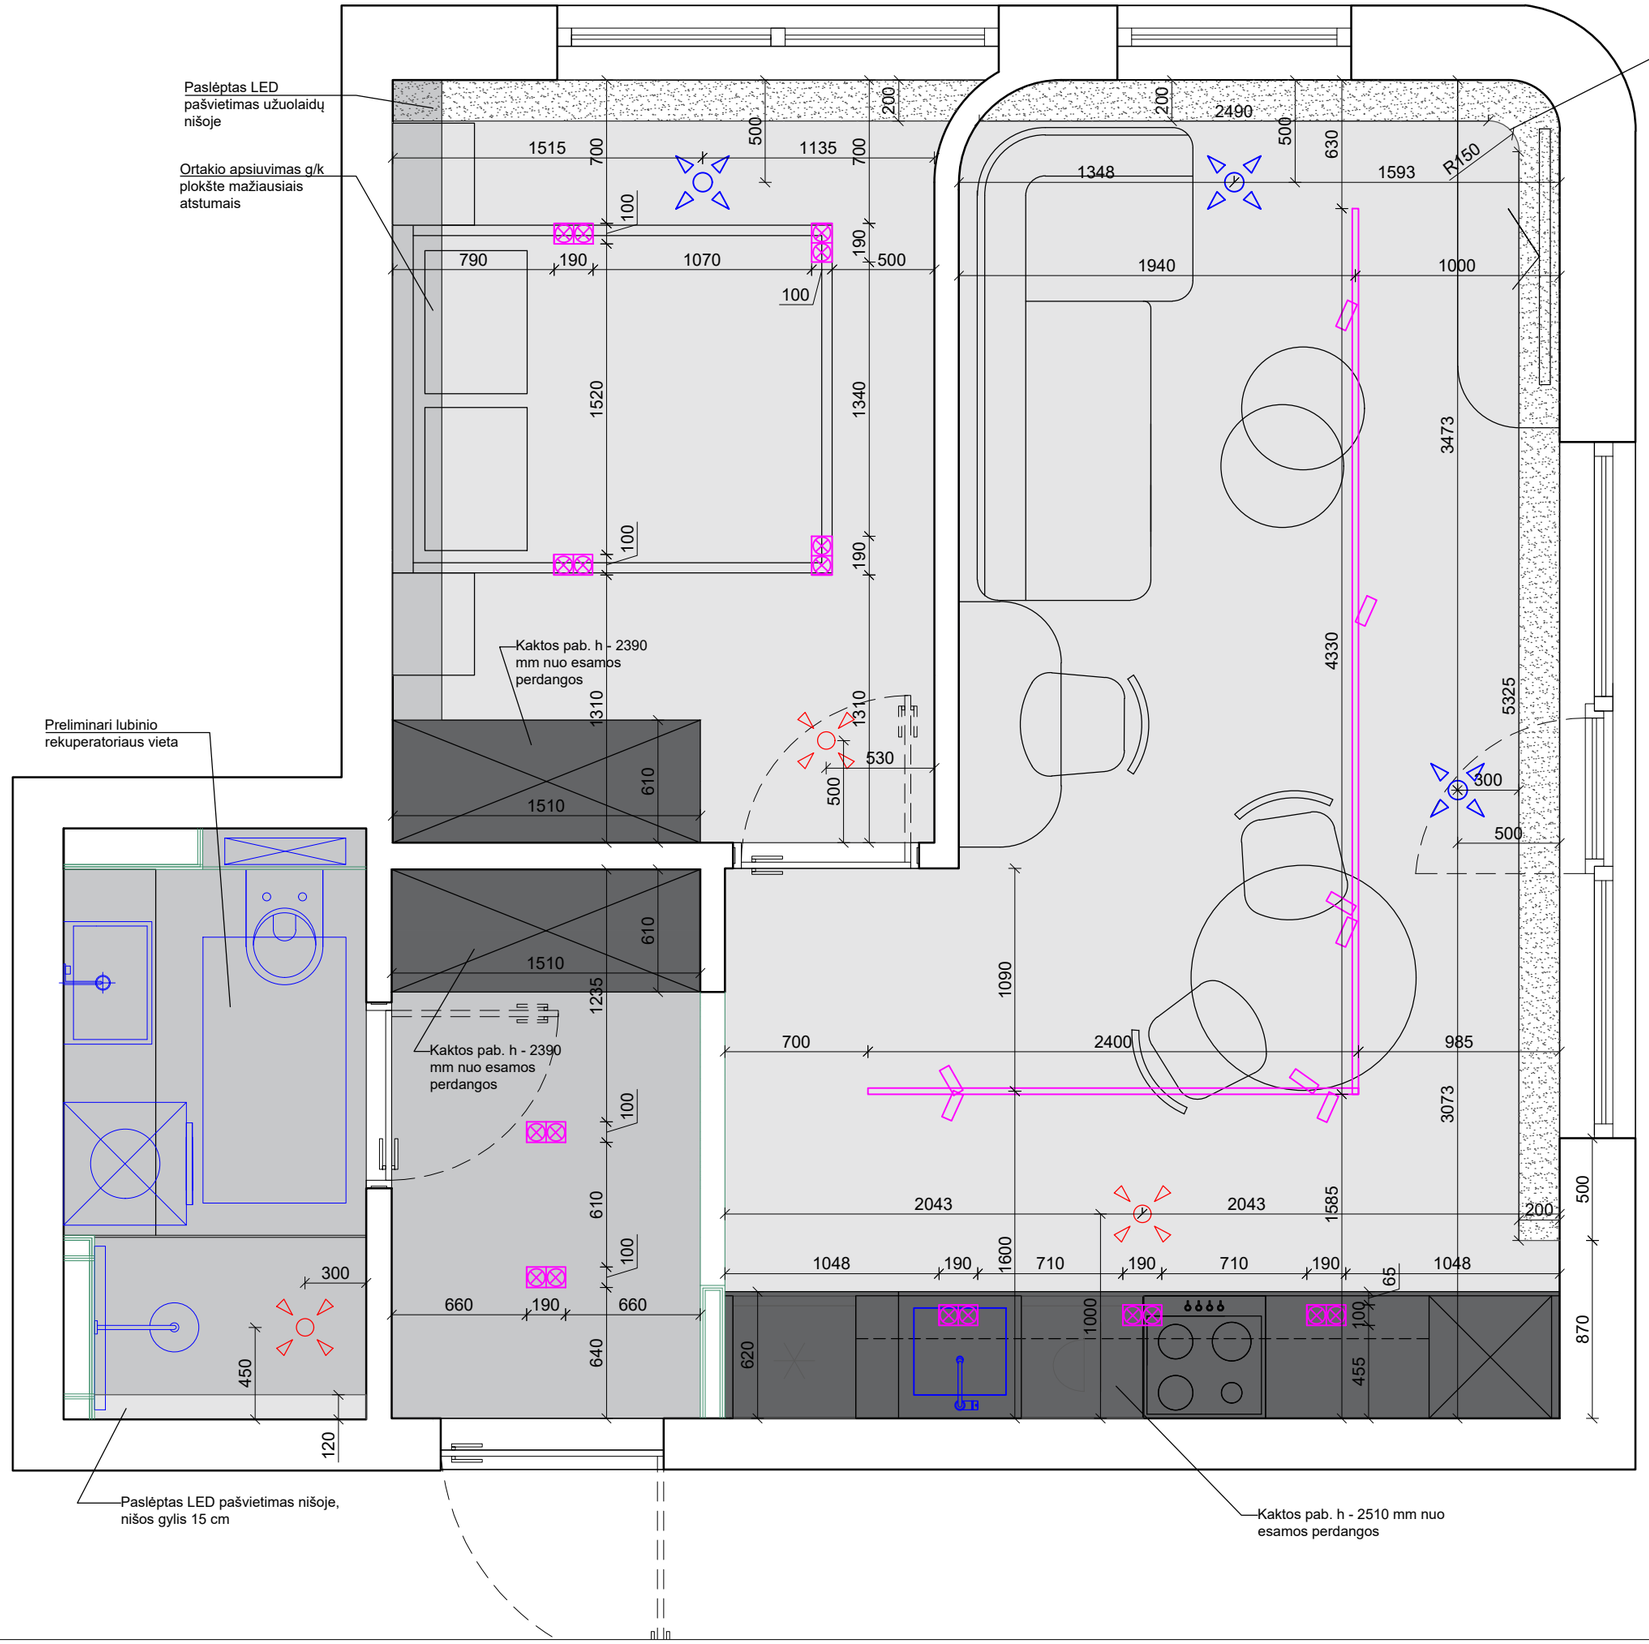

SUTARTINIS ŽYMĖJIMAS:


- Pakabinamos gipso kartono lubos, -160 mm
- Pakabinamos gipso kartono lubos, leisti kiek įmanoma mažiau
- Gipso kartono "kaktos" baldams, pagal nurodytą aukštį
- Niša užuolaidoms, klijuojamas gipso kartonas arba glaistoma esama perdanga
- Priglaistomi apvalūs difuzoriai gipso kartono lubose
- Priglaistomi dvigubi gipsiniai šviestuvai su LED lempute G10
- Priglaistomas magnetinis bėgellis, 54 mm gylio

PASTABOS:

1. Lubos dažomos bazine balta spalva.
2. Lubos montuojamos su šešėline siūle prie sienos 1-2 mm.

Pakabinamų g/k lubų planas. M 1:30

Interjero dizainerė Marija Orlovienė, +370 620 81230, marija@strix.studio

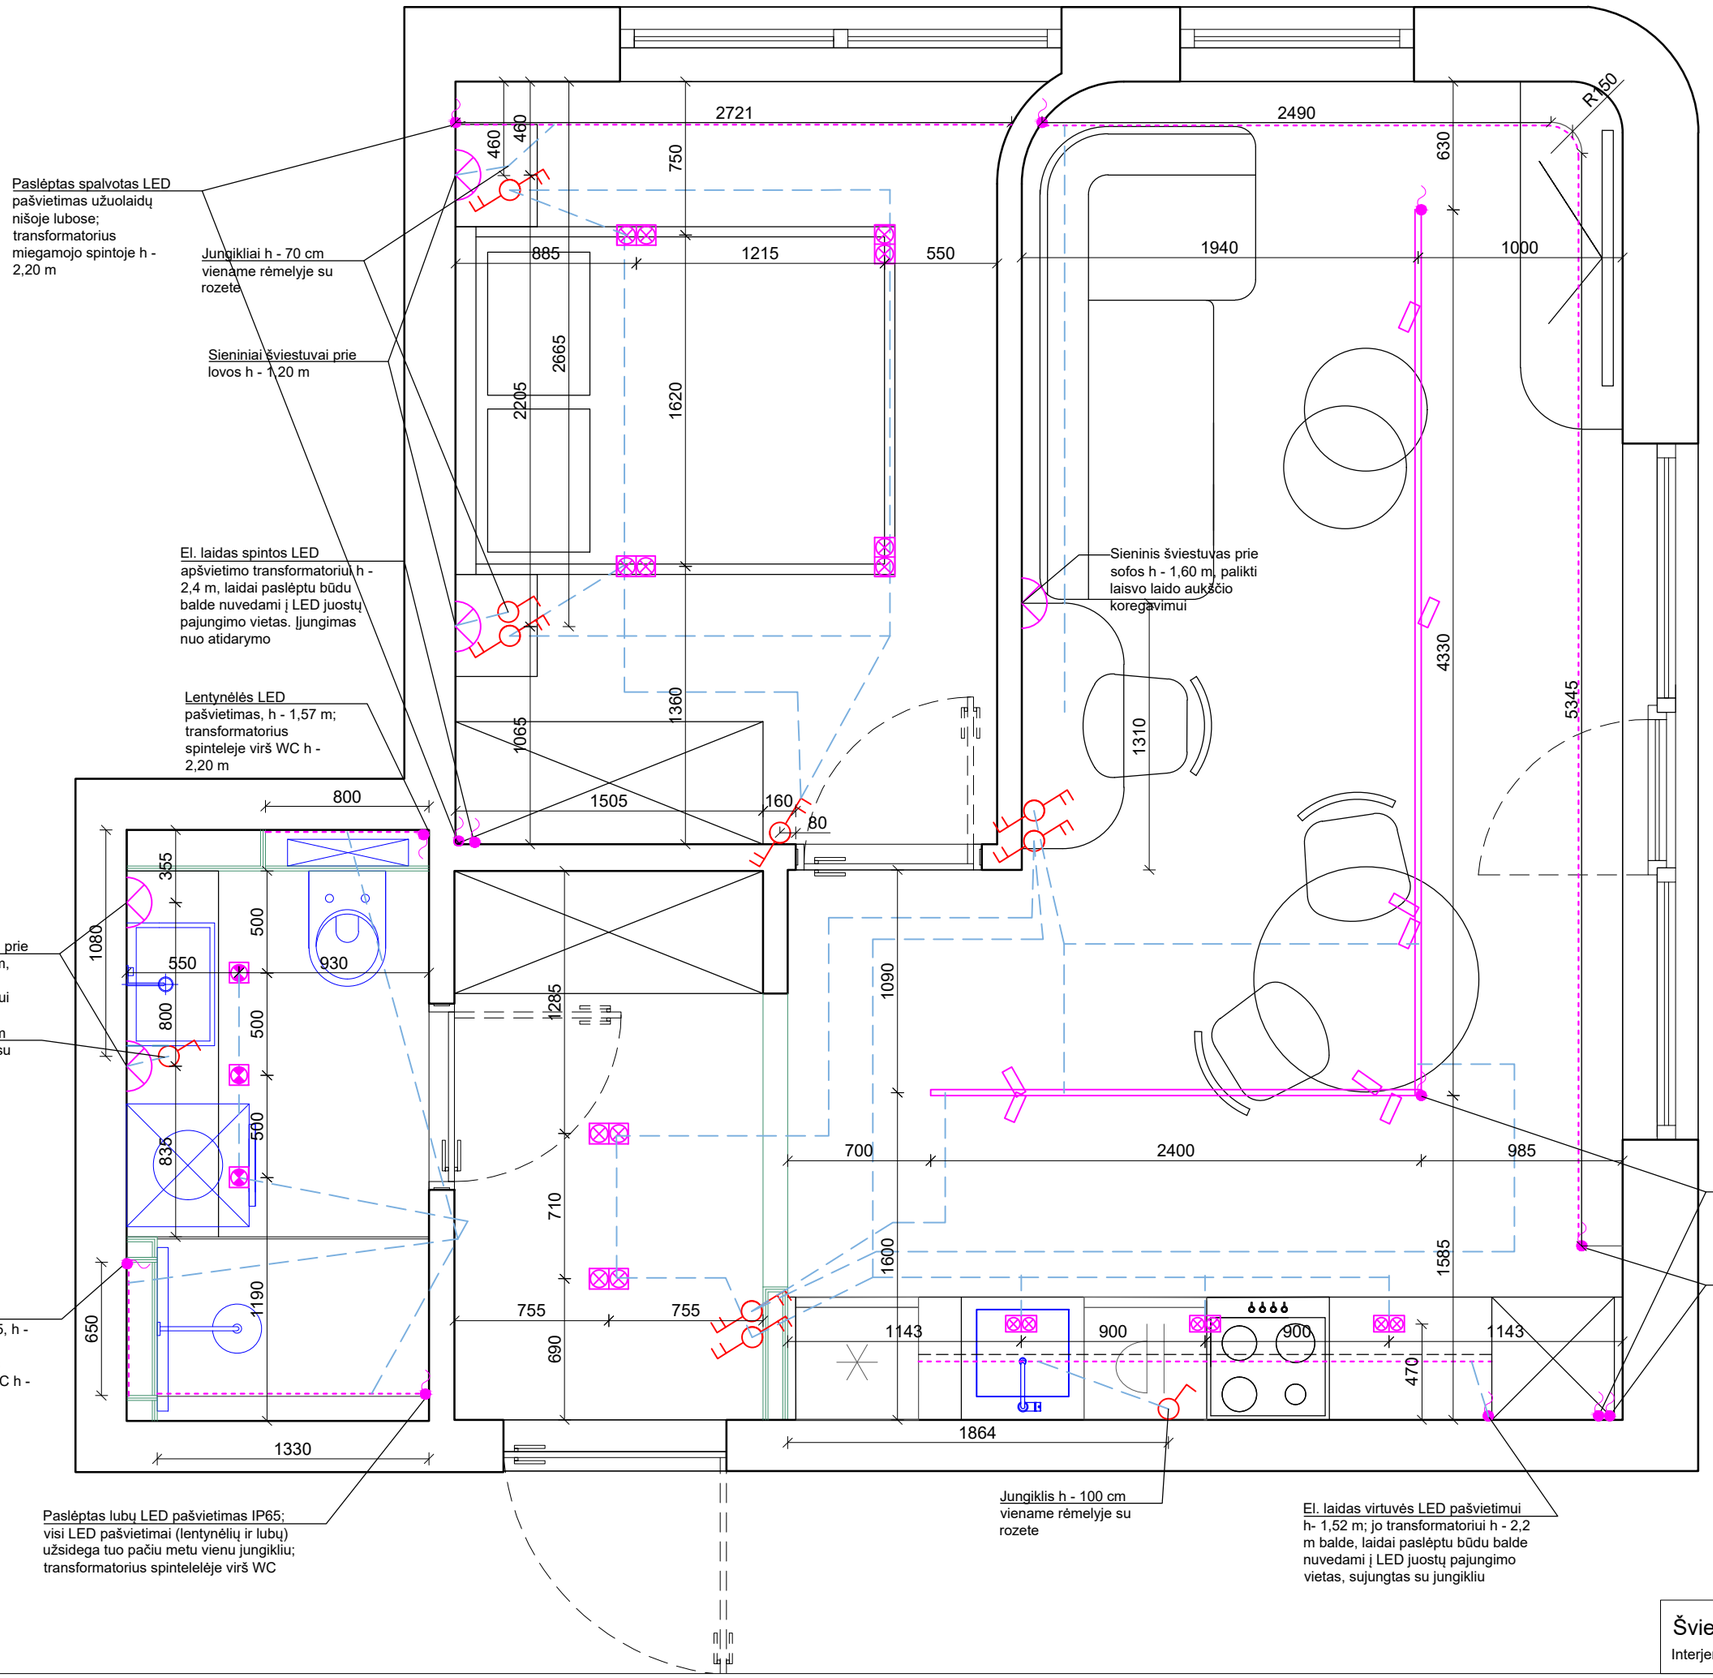

Šviestuvų išdėstymo planas. M 1:30

Interjero dizainerė Marija Orlovienė, +370 620 81230, marija@strix.studio