


INTERJERO PROJEKTAS

Gyvenamojo namo Beržų g. 24

mar group

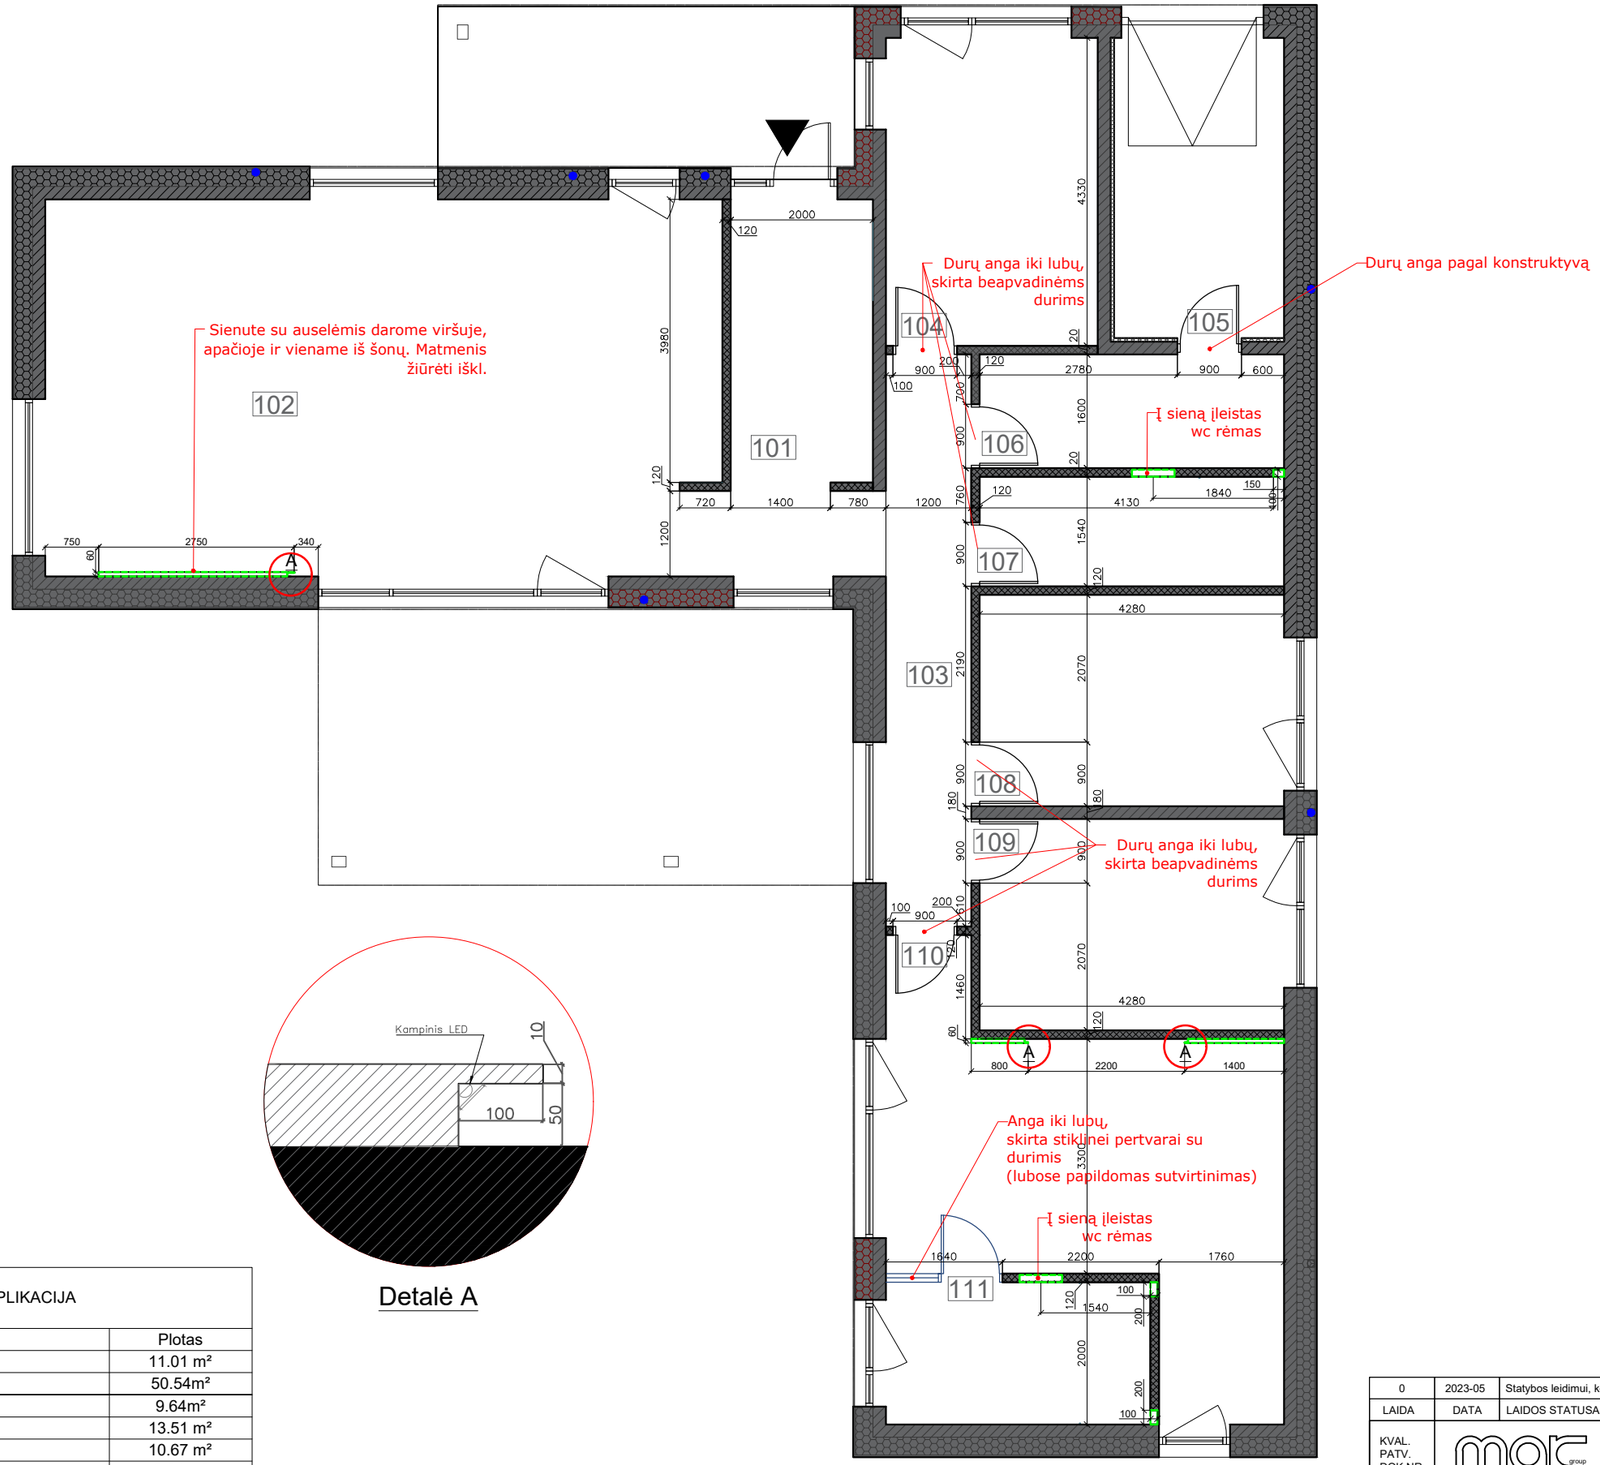

Detalė A


PATALPŲ EKSPLIKACIJA		
Nr.	Pavadinimas	Plotas
101	Tambūras	11.01 m²
102	Svetainė/virtuvė	50.54m²
103	Koridorius	9.64m²
104	Darbo kambarys	13.51 m²
105	Garažas	10.67 m²
106	Skalbykla	6.84 m²
107	Vaikų san.mazgas	6.59 m²
108	Berniuko kambarys	12.68 m²
109	Berniuko kambarys	12.71 m²
110	Miegamasis	23.97 m²
111	Tėvų vonia	7.45 m²
Bendrasis plotas		165.61 m²

0	2023-05	Statybos leidimui, konkursui ir statybai	
LAIDA	DATA	LAIDOS STATUSAS. KEITIMO PRIEŽASTIS (JEI TAIKOMA)	
KVAL. PATV. DOK.NR.	UAB MAK GROUP Įm.k. 302735585 Adr.: Parodos g. 20, Kaunas Tel.: +37068398769 El. paštas : info@makgroup.eu www.makgroup.eu	STATINIO PROJEKTO PAVADINIMAS Gyvenamosios paskirties (vieno buto) pastato , Beržų g. 24, statybos projektas	
A1675	PV	STATINIO NR. IR PAVADINIMAS **INTERJERO DALIS**	LAIDA
A1675	PDV SA	PERTVARŲ PLANAS	0
0027195	Arch.		
lt	STATYTOJAS IR (ARBA) UŽSAKOVAS	DOKUMENTO ŽYMUO MAK 01230523-01-TDP-SA. B-02	LAPAS 1 / LAPŲ 15



PATALPŲ EKSPLIKACIJA		
Nr.	Pavadinimas	Plotas
101	Tambūras	11.01 m²
102	Svetainė/virtuvė	50.54m²
103	Koridorius	9.64m²
104	Darbo kambarys	13.51 m²
105	Garažas	10.67 m²
106	Skalbykla	6.84 m²
107	Vaikų san.mazgas	6.59 m²
108	Berniuko kambarys	12.68 m²
109	Berniuko kambarys	12.71 m²
110	Miegamasis	23.97 m²
111	Tėvų vonia	7.45 m²
Bendrasis plotas		165.61 m²

0	2023-05	Statybos leidimui, konkursui ir statybai	
LAIDA	DATA	LAIDOS STATUSAS. KEITIMO PRIEŽASTIS (JEI TAIKOMA)	
KVAL. PATV. DOK.NR.	UAB MAK GROUP Įm.k. 302735585 Adr.: Parodos g. 20, Kaunas Tel.: +37068398769 El. paštas : info@makgroup.eu www.makgroup.eu	STATINIO PROJEKTO PAVADINIMAS Gyvenamosios paskirties (vieno buto) pastato , Beržų g. 24, statybos projektas	
A1675	PV	STATINIO NR. IR PAVADINIMAS **INTERJERO DALIS**	LAIDA
A1675	PDV SA	BALDŲ PLANAS	0
0027195	Arch.		
lt	STATYTOJAS IR (ARBA) UŽSAKOVAS	DOKUMENTO ŽYMUO MAK 01230523-01-TDP-SA. B-02	LAPAS 2 / LAPŲ 15

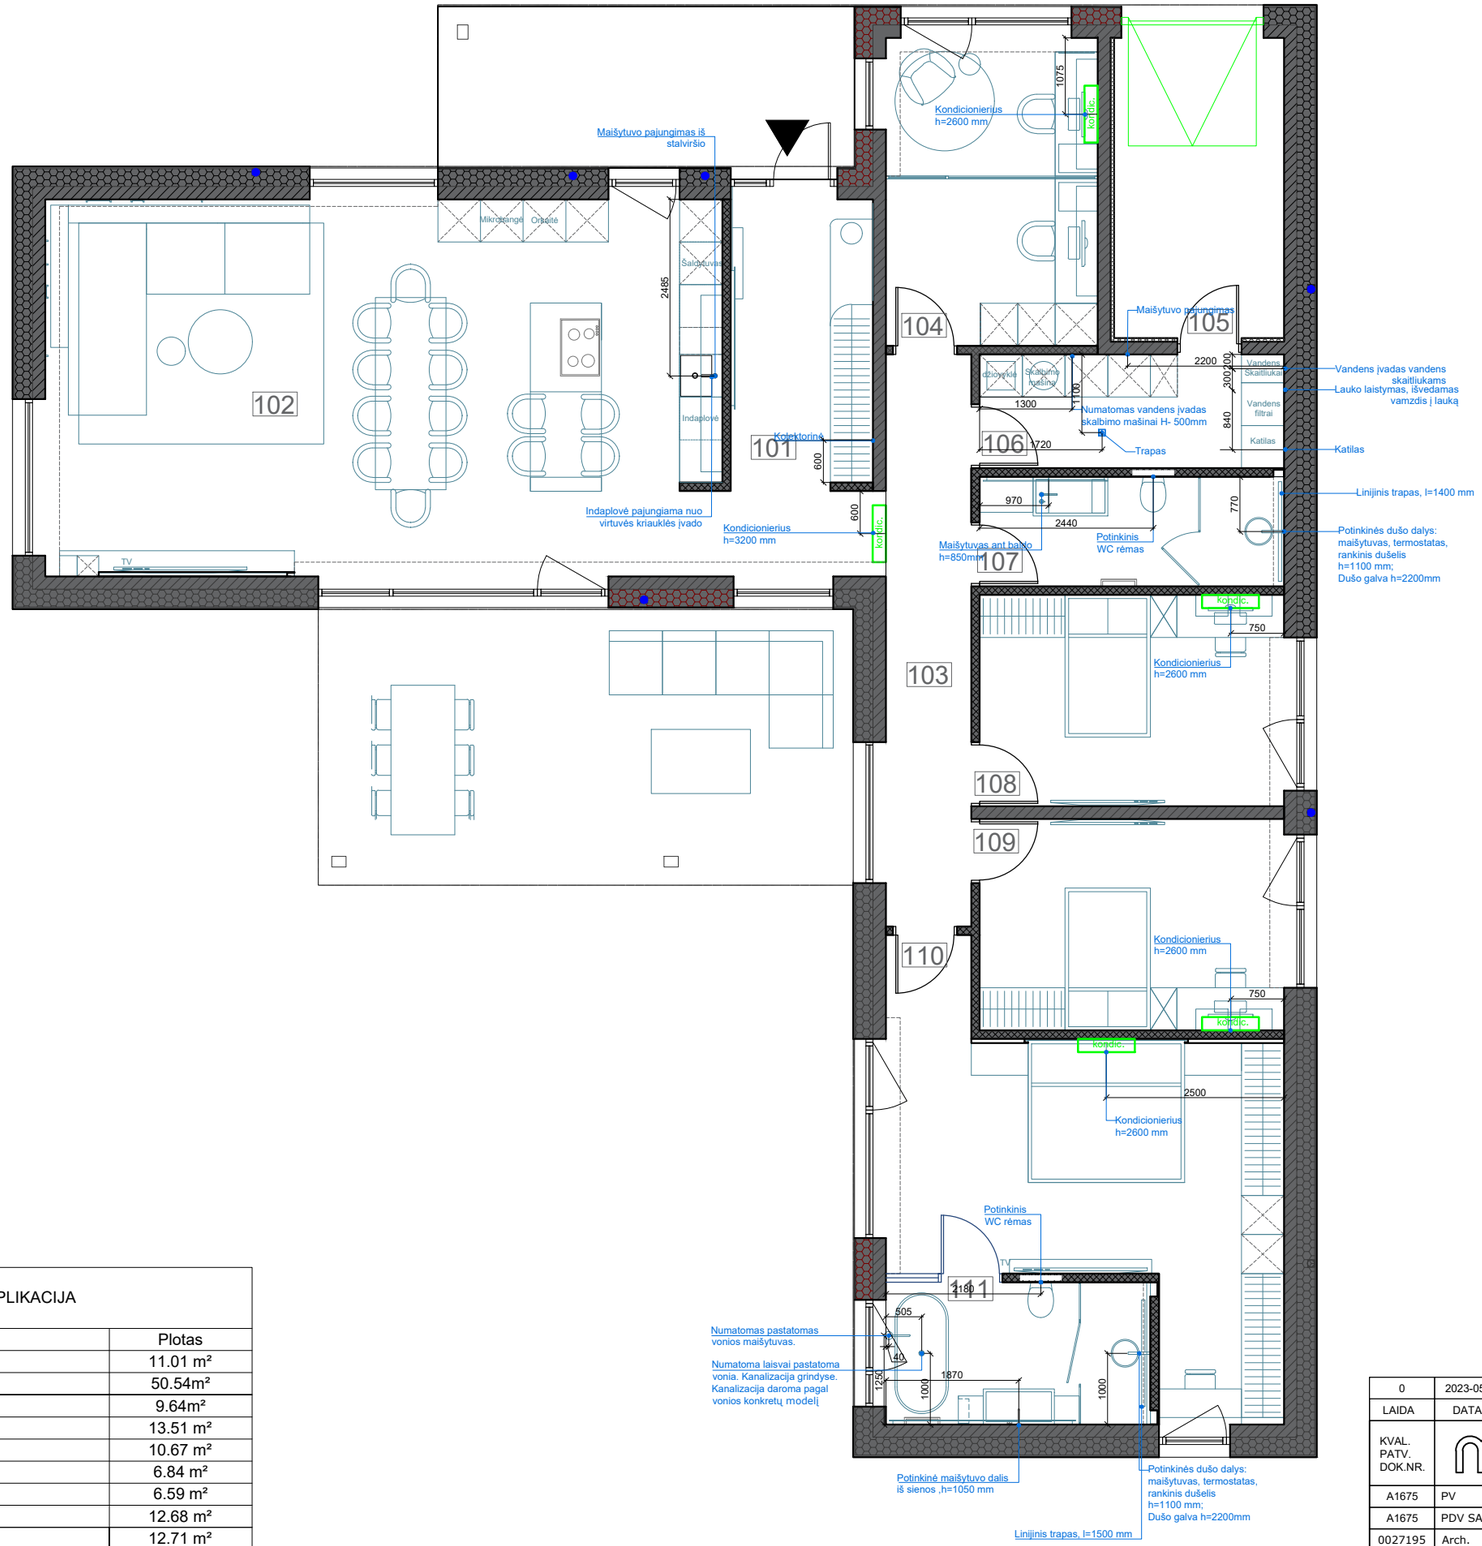

PATALPŲ EKSPLIKACIJA


Nr.	Pavadinimas	Plotas
101	Tambūras	11.01 m²
102	Svetainė/virtuvė	50.54m²
103	Koridorius	9.64m²
104	Darbo kambarys	13.51 m²
105	Garažas	10.67 m²
106	Skalbykla	6.84 m²
107	Vaikų san.mazgas	6.59 m²
108	Berniuko kambarys	12.68 m²
109	Berniuko kambarys	12.71 m²
110	Miegamasis	23.97 m²
111	Tėvų vonia	7.45 m²
Bendrasis plotas		165.61 m²

PASTABOS:

Pastabos:

1. Matmenys pateikti iki rozetės centro.
2. Rozetės įrengiamos 250 mm nuo projektuojamų grindų dangos, jei nenurodyta kitaip.
3. Rozečių pririšimus tikslinti išklotinėse.
4. Televizoriaus rozetes derinti su klientu, pagal tai ar pasilikti galimybę TV kabinti ant sienos.
5. Gyvatuko ir integruotos buitinės technikos pajungimus tikslinti pagal pasirinkto modelio specifikacijas.
6. Vonioje, garaže ir kitose drėgnose patalpose (ir lauke) rozetės turi būti hermetiškos.
7. Katilinės rozetes tikslinti pagal įrangos reikalavimus.
8. Lauko rozetes ir apšvietimą derinti atskiru projektu, aukščius tikslinti vietoje.
9. Termostatų vietas, jei tokie įrengiami, tikslinti su projektuotoju.
10. Elektros jungikliai įrengiami 90 cm aukštyje, jei nenurodyta kitaip.

0	2023-05	Statybos leidimui, konkursui ir statybai	
LAIDA	DATA	LAIDOS STATUSAS. KEITIMO PRIEŽASTIS (JEI TAIKOMA)	
KVAL. PATV. DOK.NR.	UAB MAK GROUP Įm.k. 302735585 Adr.: Parodos g. 20, Kaunas Tel.: +37068398769 El. paštas : info@makgroup.eu www.makgroup.eu	STATINIO PROJEKTO PAVADINIMAS Gyvenamosios paskirties (vieno buto) pastato , Beržų g. 24, statybos projektas	
A1675	PV	STATINIO NR. IR PAVADINIMAS **INTERJERO DALIS** SANTECHNIKOS PLANAS	LAIDA 0
A1675	PDV SA		
0027195	Arch.		
lt	STATYTOJAS IR (ARBA) UŽSAKOVAS	DOKUMENTO ŽYMUO MAK 01230523-01-TDP-SA.B-02	LAPAS 3 / LAPŲ 15

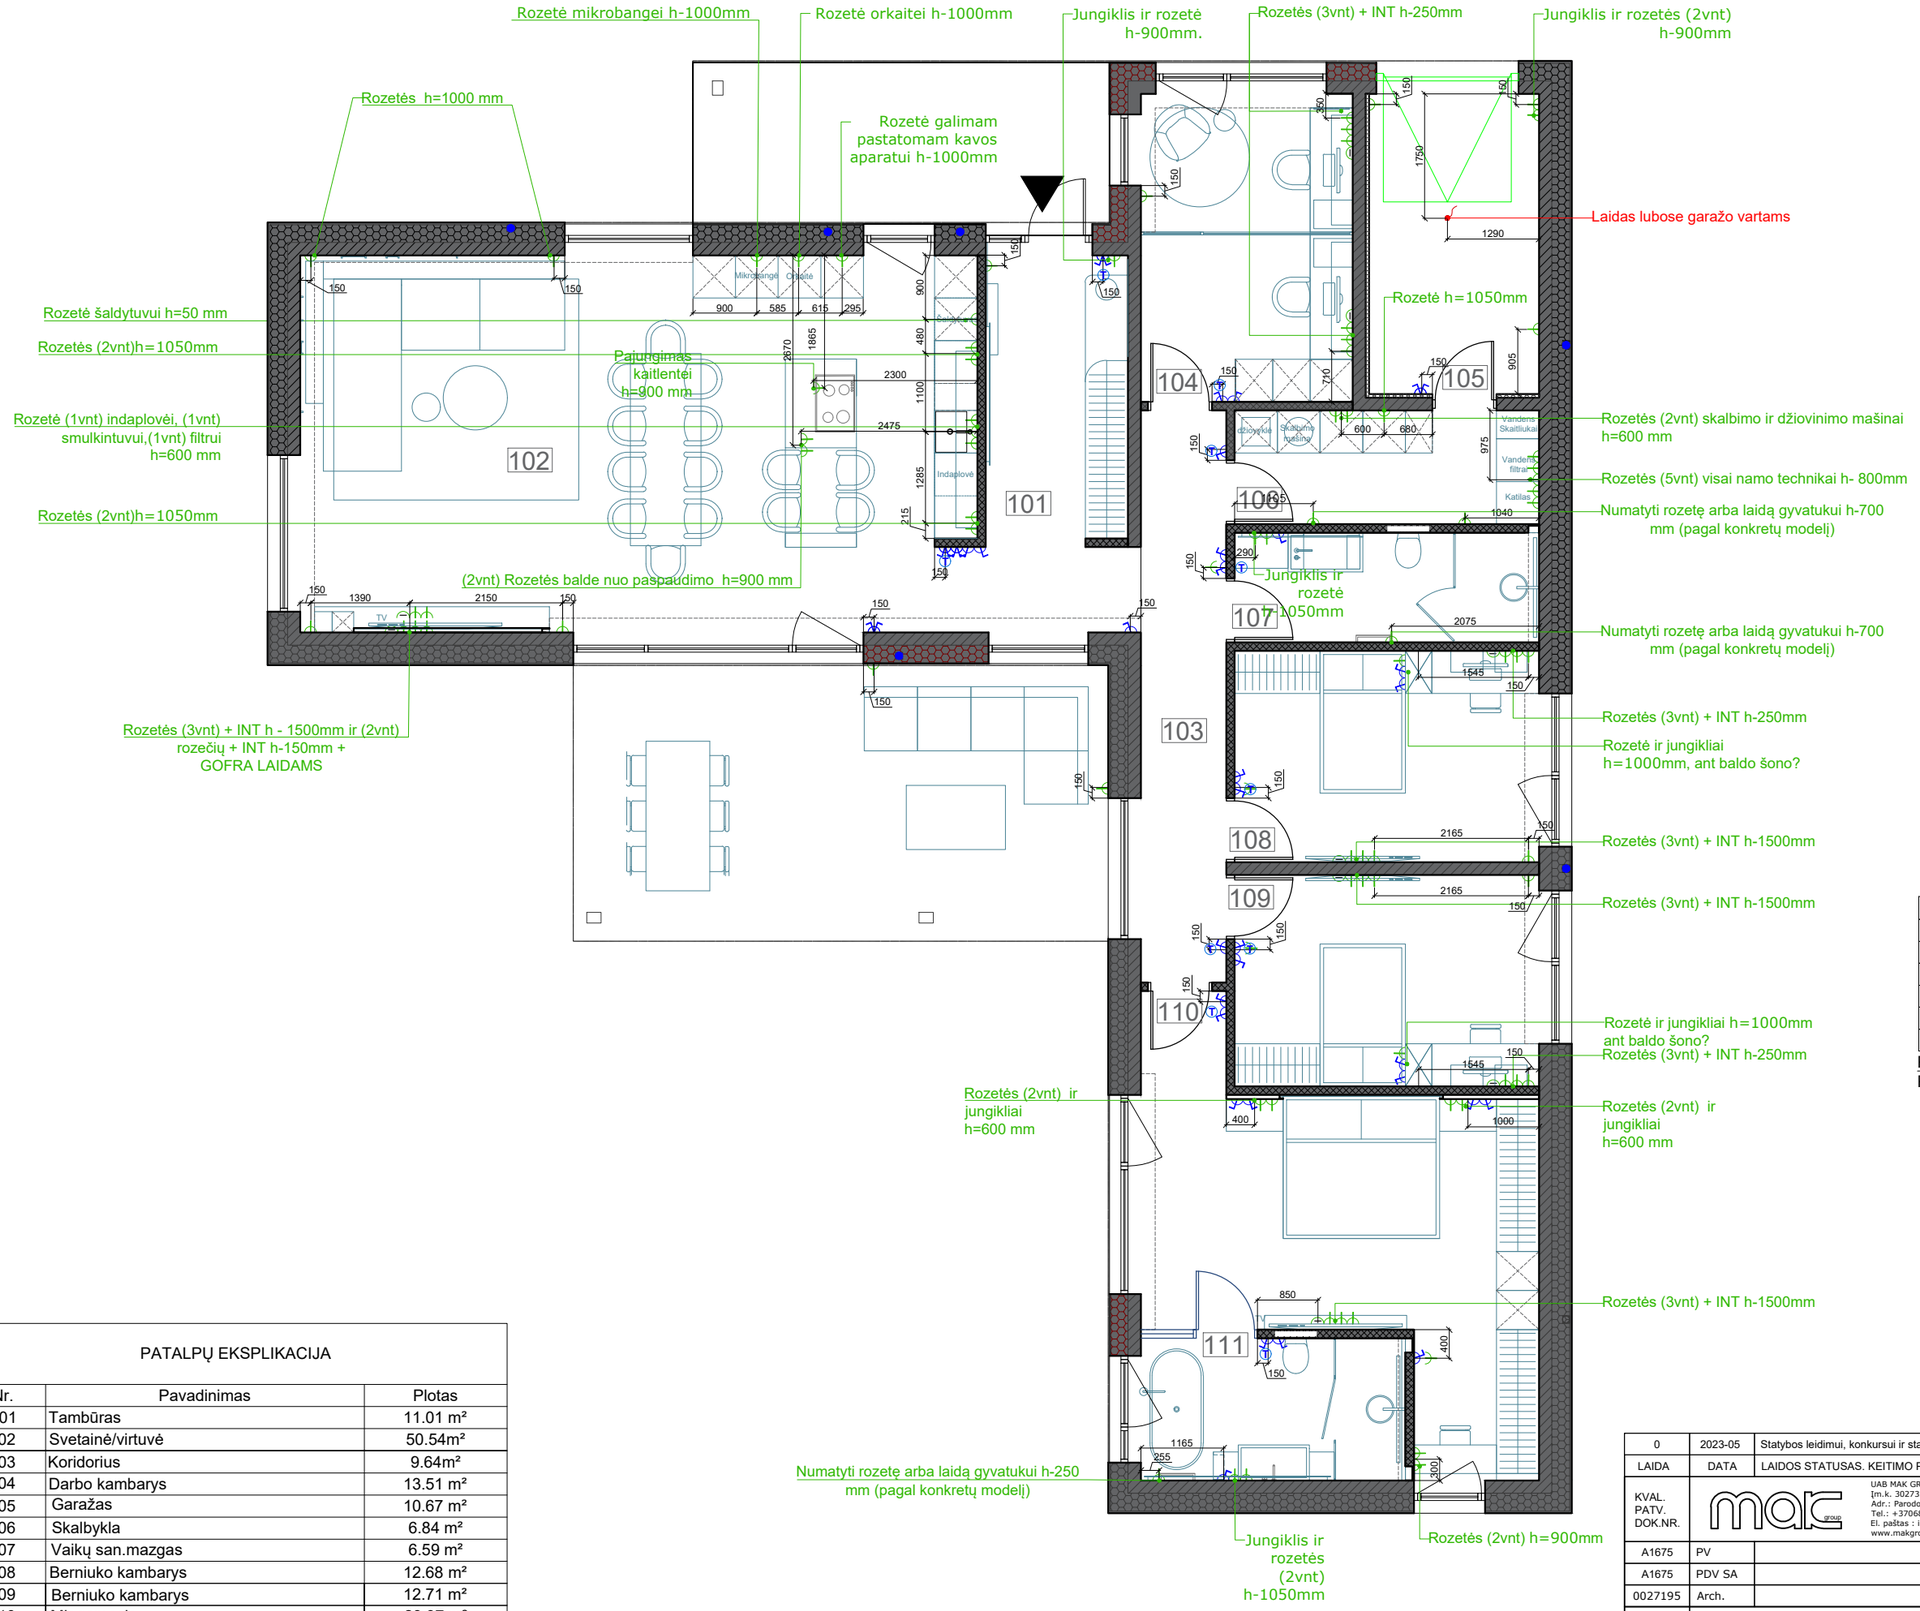

Sutartiniai žymėjimai	
	Rozetė
	Vartai
	Antena
	Interneto rozetė
	Pajungimas prietaisui (šalia parašyta kam)
	USB-C

PASTABOS:


Pastabos:


1. Matmenys pateikti iki rozetės centro.
2. Rozetės įrengiamos 250 mm nuo projektuojamų grindų dangos, jei nenurodyta kitaip.
3. Rozečių pririšimus tikslinti išklotinėse.
4. Televizoriaus rozetes derinti su klientu, pagal tai ar pasilikti galimybę TV kabinti ant sienos.
5. Gyvatuko ir integruotos buitinės technikos pajungimus tikslinti pagal pasirinkto modelio specifikacijas.
6. Vonioje, garaže ir kitose drėgnose patalpose (ir lauke) rozetės turi būti hermetiškos.
7. Katilinės rozetes tikslinti pagal įrangos reikalavimus.
8. Lauko rozetes ir apšvietimą derinti atskiru projektu, aukščius tikslinti vietoje.
9. Termostatų vietas, jei tokie įrengiami, tikslinti su projektuotoju.
10. Elektros jungikliai įrengiami 90 cm aukštyje, jei nenurodyta kitaip.


PATALPŲ EKSPLIKACIJA

Nr.	Pavadinimas	Plotas
101	Tambūras	11.01 m²
102	Svetainė/virtuvė	50.54m²
103	Koridorius	9.64m²
104	Darbo kambarys	13.51 m²
105	Garažas	10.67 m²
106	Skalbykla	6.84 m²
107	Vaikų san.mazgas	6.59 m²
108	Berniuko kambarys	12.68 m²
109	Berniuko kambarys	12.71 m²
110	Miegamasis	23.97 m²
111	Tėvų vonia	7.45 m²
Bendrasis plotas		165.61 m²

0	2023-05	Statybos leidimui, konkursui ir statybai	
LAIDA	DATA	LAIDOS STATUSAS. KEITIMO PRIEŽASTIS (JEI TAIKOMA)	
KVAL. PATV. DOK.NR.	UAB MAK GROUP Įm.k. 302735585 Adr.: Parodos g. 20, Kaunas Tel.: +37068398769 El. paštas : info@makgroup.eu www.makgroup.eu	STATINIO PROJEKTO PAVADINIMAS Gyvenamosios paskirties (vieno buto) pastato , Beržų g. 24, statybos projektas	
A1675	PV	STATINIO NR. IR PAVADINIMAS **INTERJERO DALIS** ROZEČIŲ PLANAS	LAIDA 0
A1675	PDV SA		
0027195	Arch.		
lt	STATYTOJAS IR (ARBA) UŽSAKOVAS	DOKUMENTO ŽYMUO MAK 01230523-01-TDP-SA. B-02	LAPAS 4 / LAPŲ 15

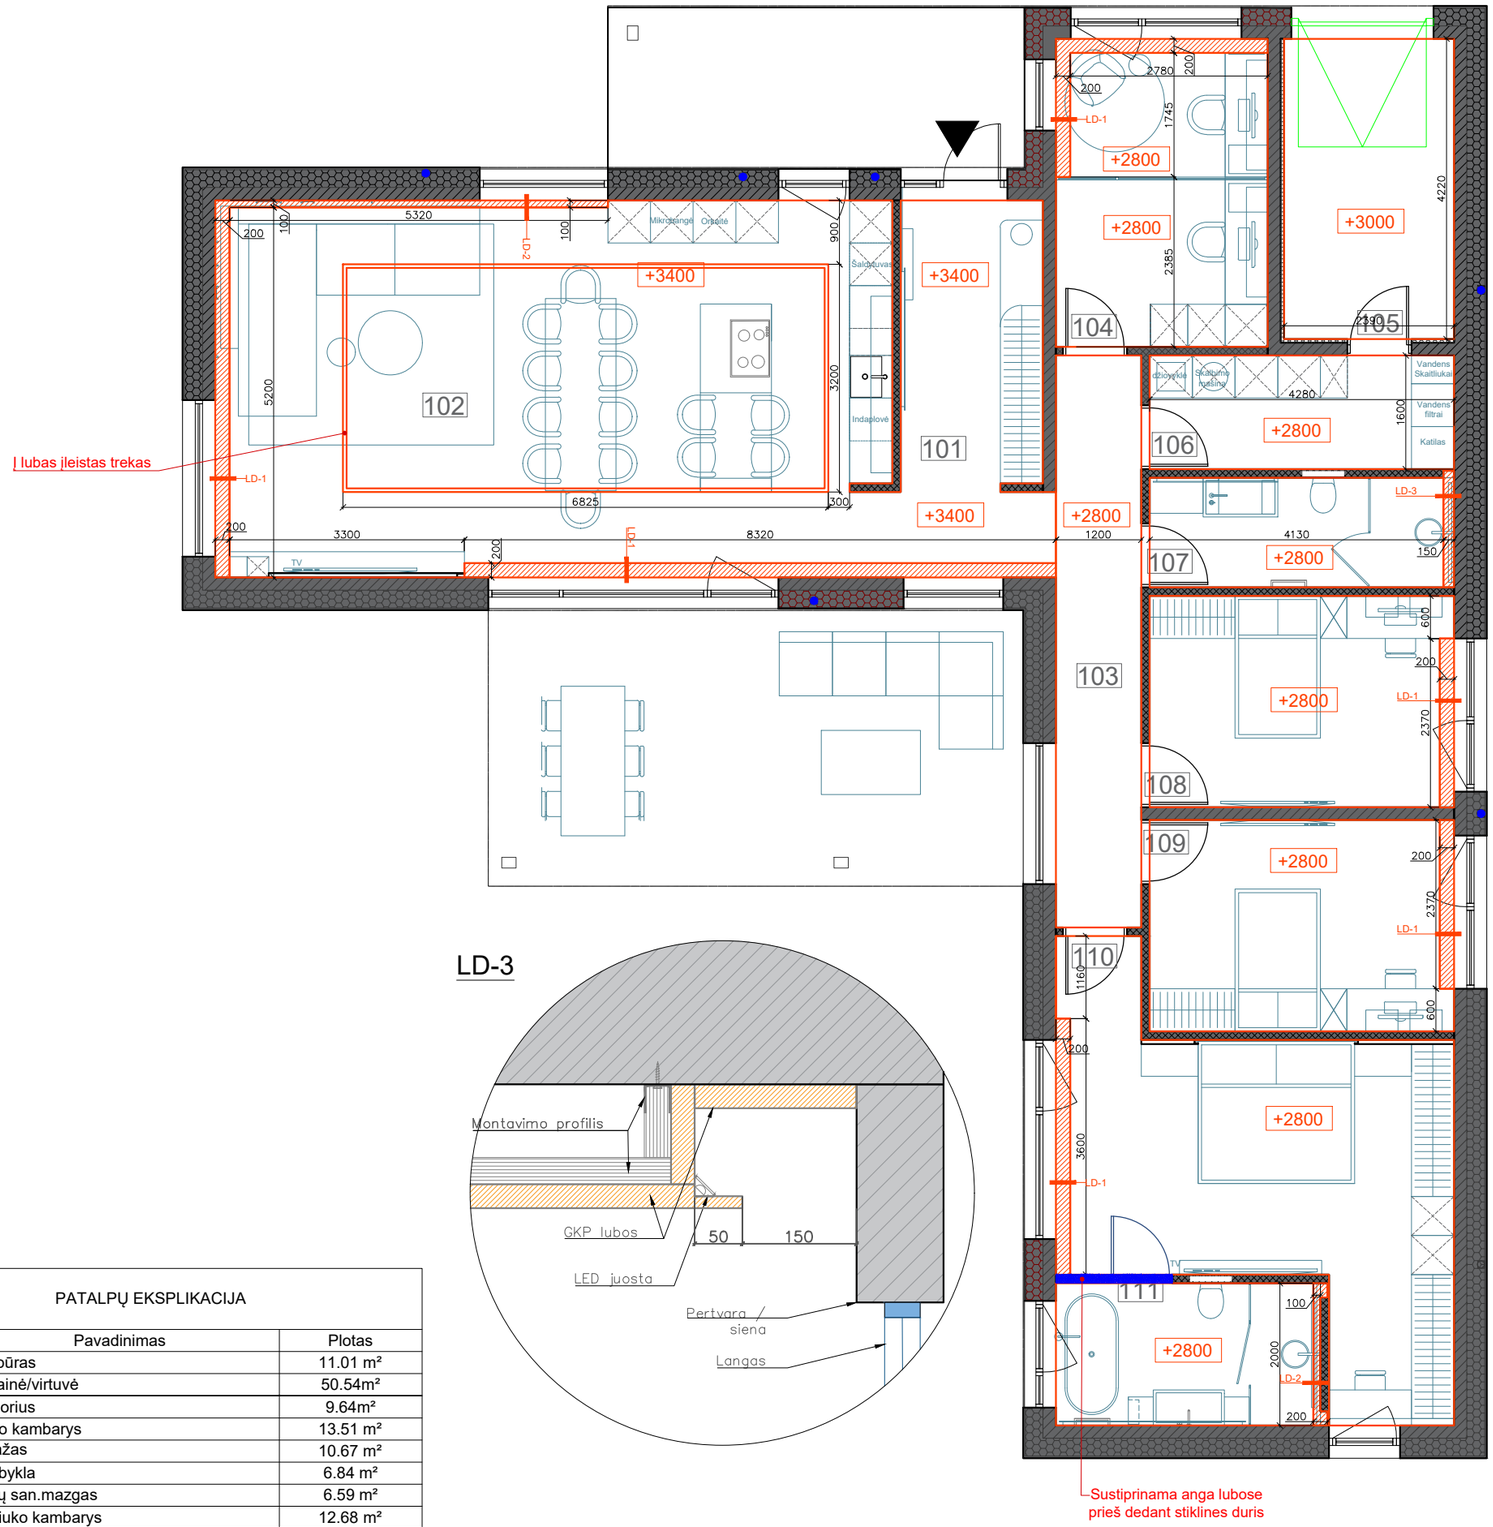

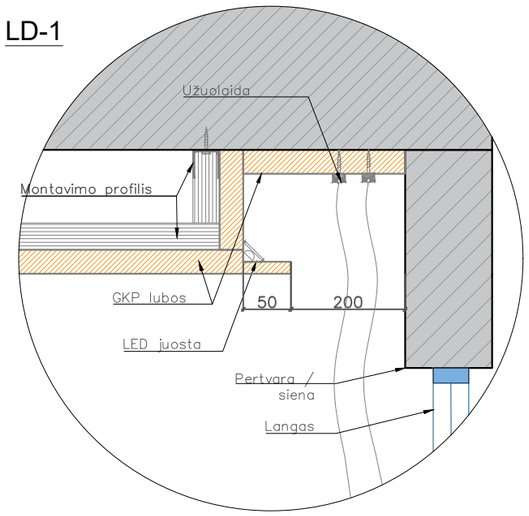

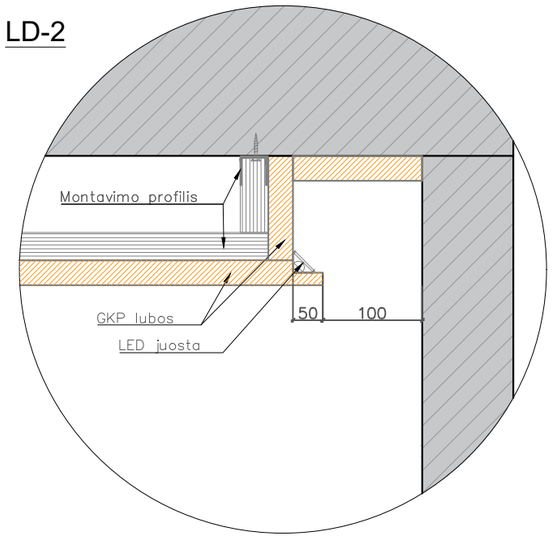

Sustiprinama anga lubose prieš dedant stiklines duris

PATALPŲ EKSPLIKACIJA

Nr.	Pavadinimas	Plotas
101	Tambūras	11.01 m²
102	Svetainė/virtuvė	50.54m²
103	Koridorius	9.64m²
104	Darbo kambarys	13.51 m²
105	Garažas	10.67 m²
106	Skalbykla	6.84 m²
107	Vaikų san.mazgas	6.59 m²
108	Berniuko kambarys	12.68 m²
109	Berniuko kambarys	12.71 m²
110	Miegamasis	23.97 m²
111	Tėvų vonia	7.45 m²
Bendrasis plotas		165.61 m²

Sutartiniai žymėjimai


Formuojamos nišos užuolaidoms, plotis 10-25 cm, gylis - maksimalus iki perdangos, ne daugiau 15cm. Voniose 8 cm gylio.

Įtempiamos šviečiančios lubos

+3100 Lubų apačios altitudė, aukštis nuo grindų, mm

0	2023-05	Statybos leidimui, konkursui ir statybai
LAIDA	DATA	LAIDOS STATUSAS. KEITIMO PRIEŽASTIS (JEI TAIKOMA)

KVAL. PATV. DOK.NR.	UAB MAK GROUP Įm.k. 302735585 Adr.: Parodos g. 20, Kaunas Tel.: +37068398769 El. paštas : info@makgroup.eu www.makgroup.eu	STATINIO PROJEKTO PAVADINIMAS Gyvenamosios paskirties (vieno buto) pastato , Beržų g. 24, statybos projektas	
A1675	PV	STATINIO NR. IR PAVADINIMAS **INTERJERO DALIS**	LAIDA
A1675	PDV SA	LUBŲ PLANAS	0
0027195	Arch.		
lt	STATYTOJAS IR (ARBA) UŽSAKOVAS	DOKUMENTO ŽYMUO MAK 01230523-01-TDP-SA. B-02	LAPAS 5 / LAPŲ 15

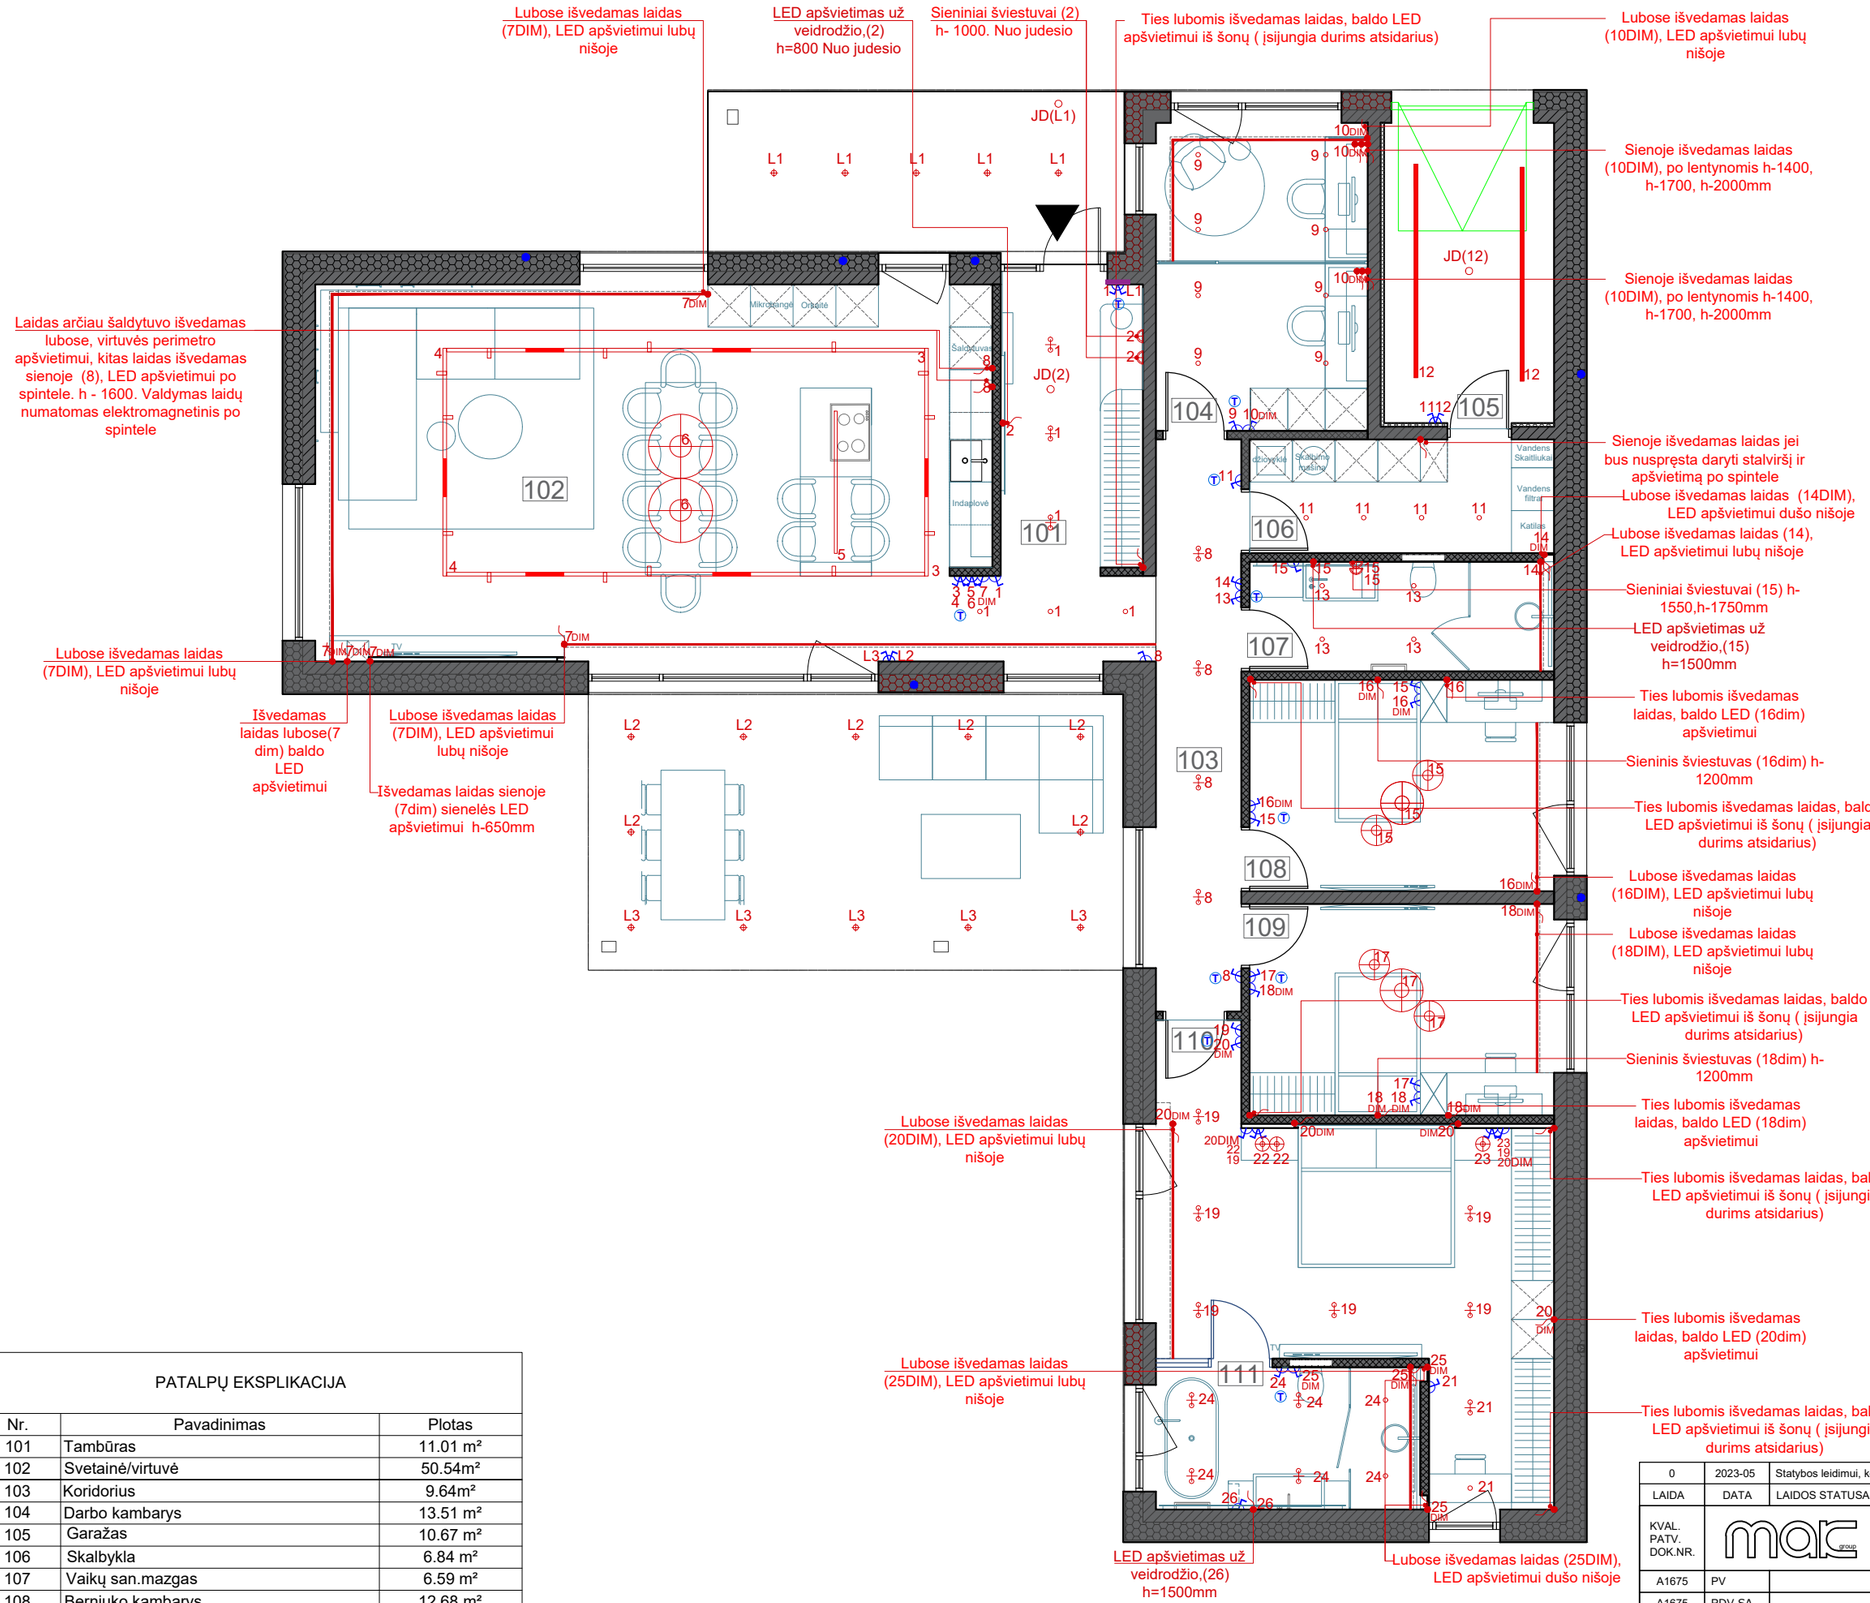

PASTABOS:


1. Sieninių šviestuvų pririšimo matmenys pateikti nuo korpuso centro.
2. Šlaitinių lubų šviestuvų atstumai pateikti planinėse projekcijose.
3. Rekuperacijos sistemos, kondicionavimo sistemos ir garso sistemos projektus derinti kartu su interjero projektuotojais, dėl difuzorių vietos ir formos parinkimo, kolonėlių dydžio ir vietos bei estetinio vaizdo.
4. Elektros jungikliai įrengiami 90 cm aukštyje, jei nenurodyta kitaip.
5. Judesio davikliai iš lubinių gali keistis į sieninius, "rozetės" tipo.
6. Jungiklių pririšimus tikslinti išklotinėse.

Sutartiniai žymėjimai	
	Paviršinis šviestuvas
	El. laido išvedimo vieta
U	Elektrinės užuolaidos
	Garso kolonėlės
	Įleistos LED juostos
	Pakabinamas lubinis šviestuvas
	Įleidžiamas halogeninis šviestuvas
	Sieninis šviestuvas
JD	Judesio daviklis
LR	Laiko relė
	Gaisro daviklis
	Vieno klavišo jungiklis
	Dviejų klavišų jungiklis (gali keistis į viengubus dėl perjungėjų)
T	Termostato vieta (per jungiklių grupės centrą), h=1400 mm
	Signalizacijos pulto vieta, h=1600 mm
	AC-POINT WiFi (signalo stiprintuvas; montuojamas ant lubų)
	Numatomos transformatorių vietos lubose, su priėjimu iš spintų

PATALPŲ EKSPLIKACIJA

Nr.	Pavadinimas	Plotas
101	Tambūras	11.01 m²
102	Svetainė/virtuvė	50.54m²
103	Koridorius	9.64m²
104	Darbo kambarys	13.51 m²
105	Garažas	10.67 m²
106	Skalbykla	6.84 m²
107	Vaikų san.mazgas	6.59 m²
108	Berniuko kambarys	12.68 m²
109	Berniuko kambarys	12.71 m²
110	Miegamasis	23.97 m²
111	Tėvų vonia	7.45 m²
Bendrasis plotas		165.61 m²

0	2023-05	Statybos leidimui, konkursui ir statybai	
LAIDA	DATA	LAIDOS STATUSAS. KEITIMO PRIEŽASTIS (JEI TAIKOMA)	
KVAL. PATV. DOK.NR.	UAB MAK GROUP Įm.k. 302735585 Adr.: Parodos g. 20, Kaunas Tel.: +37068398769 El. paštas : info@makgroup.eu www.makgroup.eu	STATINIO PROJEKTO PAVADINIMAS Gyvenamosios paskirties (vieno buto) pastato , Beržų g. 24, statybos projektas	
A1675	PV	STATINIO NR. IR PAVADINIMAS **INTERJERO DALIS** ELEKTROS APŠVIETIMO PLANAS	LAIDA 0
A1675	PDV SA		
0027195	Arch.		
lt	STATYTOJAS IR (ARBA) UŽSAKOVAS	DOKUMENTO ŽYMUO MAK 01230523-01-TDP-SA. B-02	LAPAS 6 / LAPŲ 15

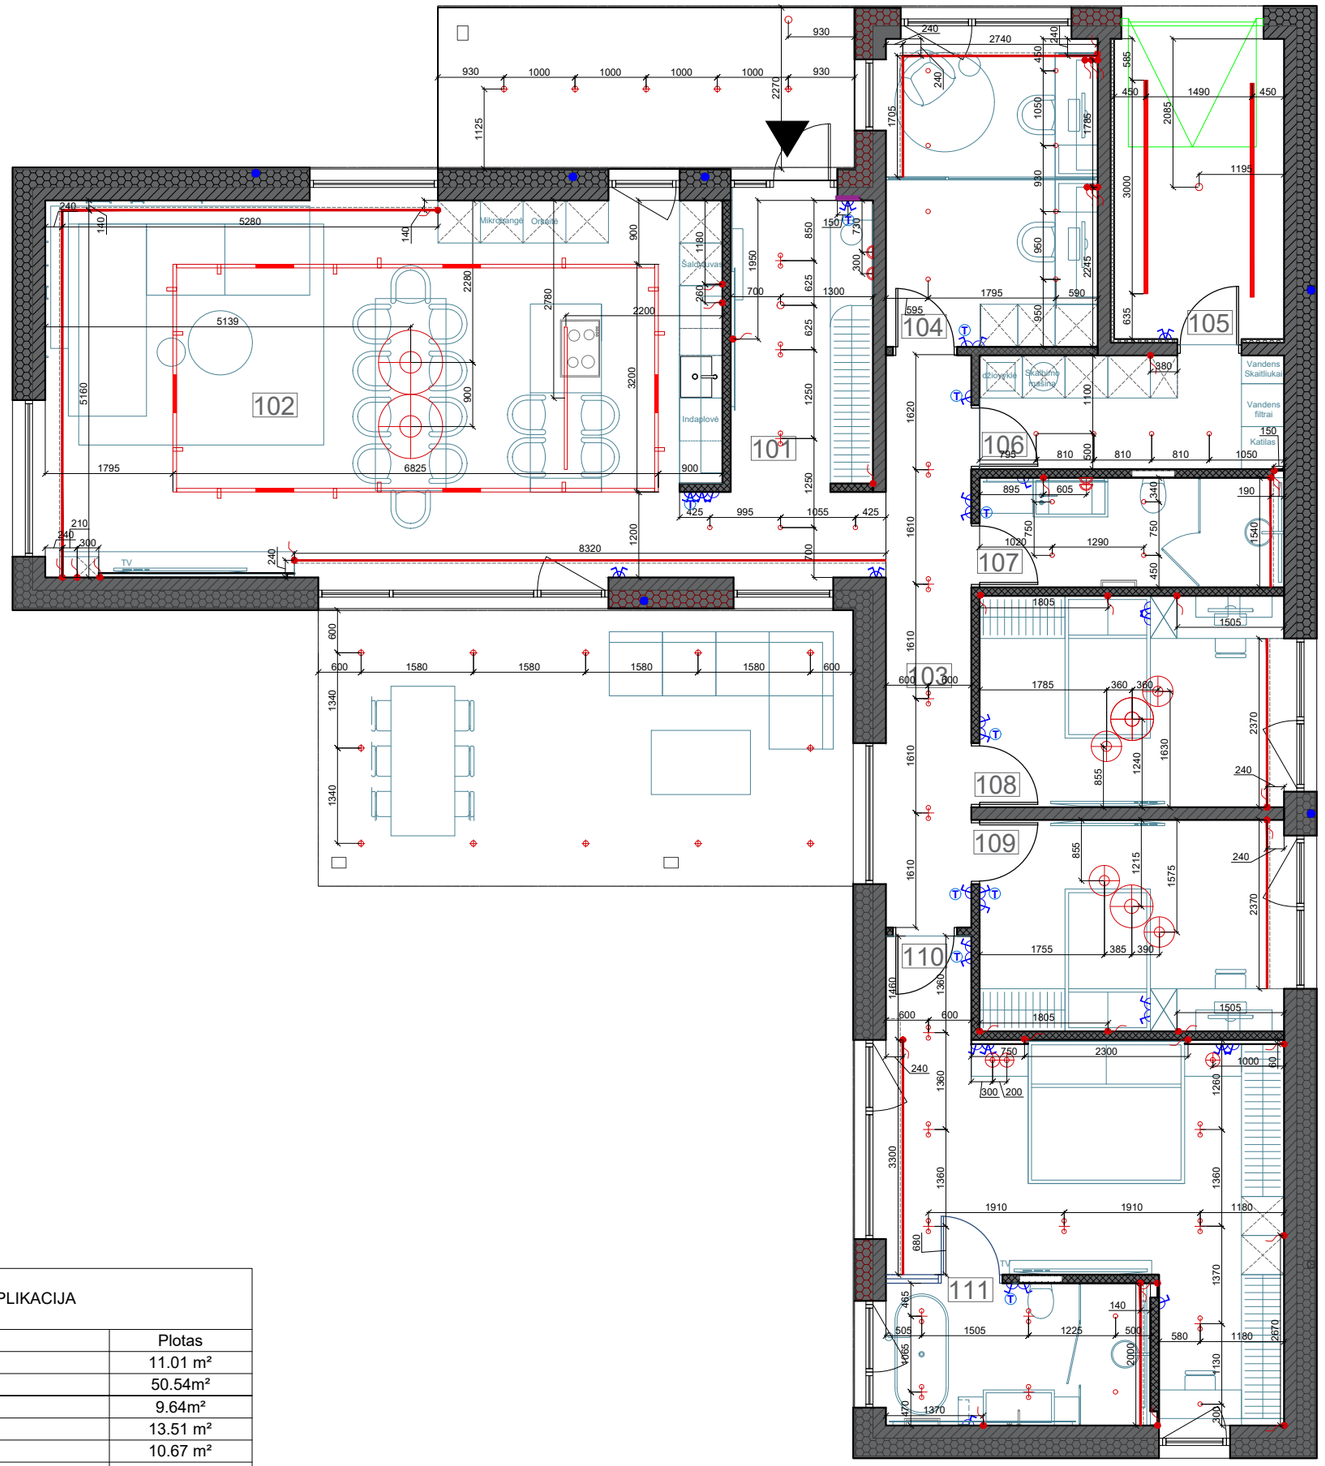

PATALPŲ EKSPLIKACIJA


Nr.	Pavadinimas	Plotas
101	Tambūras	11.01 m²
102	Svetainė/virtuvė	50.54m²
103	Koridorius	9.64m²
104	Darbo kambarys	13.51 m²
105	Garažas	10.67 m²
106	Skalbykla	6.84 m²
107	Vaikų san.mazgas	6.59 m²
108	Berniuko kambarys	12.68 m²
109	Berniuko kambarys	12.71 m²
110	Miegamasis	23.97 m²
111	Tėvų vonia	7.45 m²
Bendrasis plotas		165.61 m²

PASTABOS:

1. Sieninių šviestuvų pririšimo matmenys pateikti nuo korpuso centro.
2. Šlaitinių lubų šviestuvų atstumai pateikti planinėse projekcijose.
3. Rekuperacijos sistemos, kondicionavimo sistemos ir garso sistemos projektus derinti kartu su interjero projektuotojais, dėl difuzorių vietos ir formos parinkimo, kolonėlių dydžio ir vietos bei estetinio vaizdo.
4. Elektros jungikliai įrengiami 90 cm aukštyje, jei nenurodyta kitaip.
5. Judesio davikliai iš lubinių gali keistis į sieninius, "rozetės" tipo.
6. Jungiklių pririšimus tikslinti išklotinėse.

Sutartiniai žymėjimai	
	Paviršinis šviestuvas
	El. laido išvedimo vieta
U	Elektrinės užuolaidos
	Garso kolonėlės
	Įleistos LED juostos
	Pakabinamas lubinis šviestuvas
	Įleidžiamas halogeninis šviestuvas
	Sieninis šviestuvas
JD	Judesio daviklis
LR	Laiko relė
	Gaisro daviklis
	Vieno klavišo jungiklis
	Dviejų klavišų jungiklis (gali keistis į viengubus dėl perjungėjų)
T	Termostato vieta (per jungiklių grupės centrą), h=1400 mm
	Signalizacijos pulto vieta, h=1600 mm
	AC-POINT WiFi (signalo stiprintuvas; montuojamas ant lubų)
	Numatomos transformatorių vietos lubose, su priėjimu iš spintų

0	2023-05	Statybos leidimui, konkursui ir statybai	
LAIDA	DATA	LAIDOS STATUSAS. KEITIMO PRIEŽASTIS (JEI TAIKOMA)	
KVAL. PATV. DOK.NR.	UAB MAK GROUP Įm.k. 302735585 Adr.: Parodos g. 20, Kaunas Tel.: +37068398769 El. paštas : info@makgroup.eu www.makgroup.eu	STATINIO PROJEKTO PAVADINIMAS Gyvenamosios paskirties (vieno buto) pastato , Beržų g. 24, statybos projektas	
A1675	PV	STATINIO NR. IR PAVADINIMAS **INTERJERO DALIS** ELEKTROS APŠVIETIMO PRIRIŠIMO PLANAS	LAIDA 0
A1675	PDV SA		
0027195	Arch.		
It	STATYTOJAS IR (ARBA) UŽSAKOVAS	DOKUMENTO ŽYMUO MAK 01230523-01-TDP-SA. B-02	LAPAS 7 / LAPŲ 15

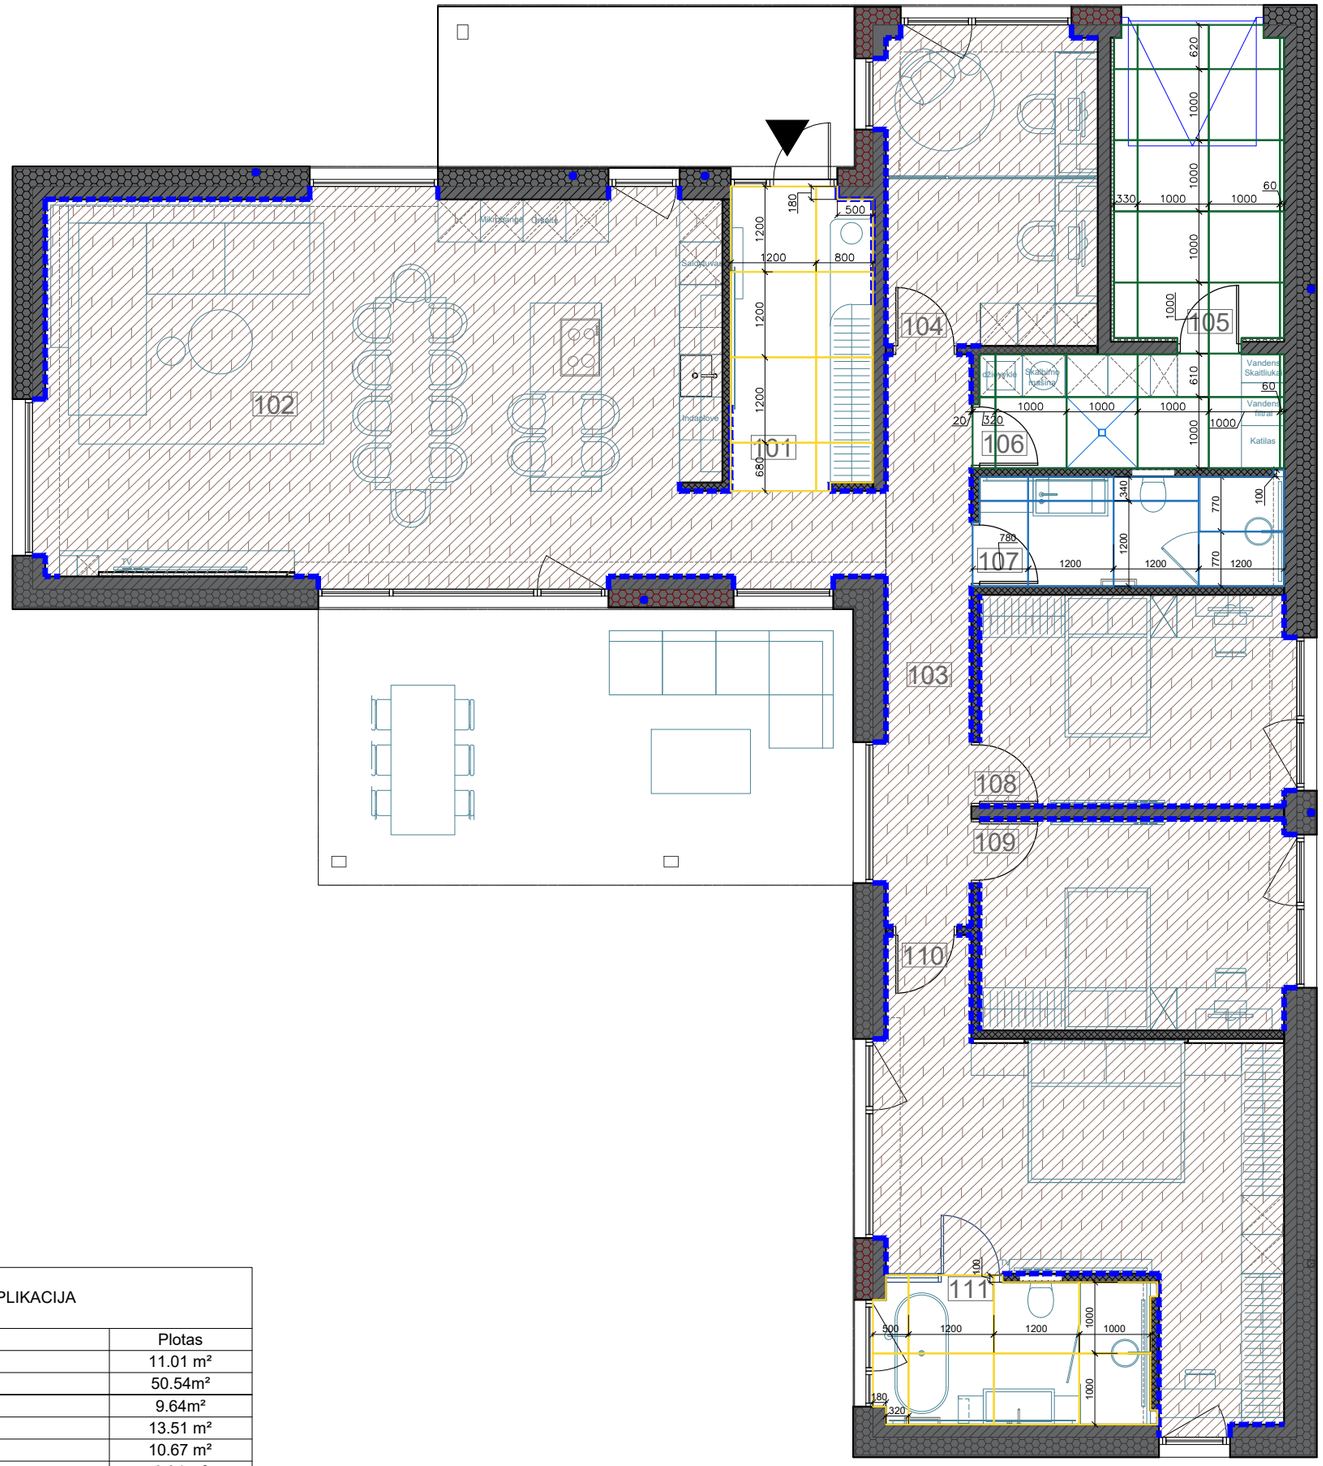

PATALPŲ EKSPLIKACIJA		
Nr.	Pavadinimas	Plotas
101	Tambūras	11.01 m²
102	Svetainė/virtuvė	50.54m²
103	Koridorius	9.64m²
104	Darbo kambarys	13.51 m²
105	Garažas	10.67 m²
106	Skalbykla	6.84 m²
107	Vaikų san.mazgas	6.59 m²
108	Berniuko kambarys	12.68 m²
109	Berniuko kambarys	12.71 m²
110	Miegamasis	23.97 m²
111	Tėvų vonia	7.45 m²
Bendrasis plotas		165.61 m²

Sutartiniai žymėjimai

- Parketlentės (~135 m²)
- Plytelės Living ceramics Vonn Light 120x120cm 14 vnt
- Plytelės Stoneplay cliff bianco 100x100cm 20 vnt.Grindjuostės h-50mm iš plytelės
- Plytelės kronosceramiche Lux falda 120x120cm 5 vnt
- Grindjuostės, h=60 mm (~56 m)

0	2023-05	Statybos leidimui, konkursui ir statybai
LAIDA	DATA	LAIDOS STATUSAS. KEITIMO PRIEŽASTIS (JEI TAIKOMA)

UAB MAK GROUP
Įm.k. 302735585
Adr.: Parodos g. 20, Kaunas
Tel.: +37068398769
El. paštas : info@makgroup.eu
www.makgroup.eu

KVAL. PATV. DOK.NR.			
A1675	PV		
A1675	PDV SA		
0027195	Arch.		
lt	STATYTOJAS IR (ARBA) UŽSAKOVAS		

STATINIO PROJEKTO PAVADINIMAS
Gyvenamosios paskirties (vieno buto) pastato , Beržų g. 24, statybos projektas

STATINIO NR. IR PAVADINIMAS
INTERJERO DALIS
GRINDŲ PLANAS

LAIDA: 0

DOKUMENTO ŽYMUO
MAK 01230523-01-TDP-SA. B-02

LAPAS: 8
LAPŲ: 15



PATALPŲ EKSPLIKACIJA

Nr.	Pavadinimas	Plotas
101	Tambūras	11.01 m²
102	Svetainė/virtuvė	50.54m²
103	Koridorius	9.64m²
104	Darbo kambarys	13.51 m²
105	Garažas	10.67 m²
106	Skalbykla	6.84 m²
107	Vaikų san.mazgas	6.59 m²
108	Berniuko kambarys	12.68 m²
109	Berniuko kambarys	12.71 m²
110	Miegamasis	23.97 m²
111	Tėvų vonia	7.45 m²
Bendrasis plotas		165.61 m²

Sutartiniai žymėjimai

- Plytelės kronosceramiche lux falda 1200x1200mm
- Plytelės kronosceramiche lux venna 2800x1200mm
- Plytelės Living ceramics vonn loom 600x1200mm
- Vaikiški tapetai
- Siena dengiama plokšte
- Dažymas balta spalva
- Veidrodis

0	2023-05	Statybos leidimui, konkursui ir statybai
LAIDA	DATA	LAIDOS STATUSAS. KEITIMO PRIEŽASTIS (JEI TAIKOMA)

KVAL. PATV. DOK.NR.

UAB MAK GROUP
Įm.k. 302735585
Adr.: Parodos g. 20, Kaunas
Tel.: +37068398769
El. paštas : info@makgroup.eu
www.makgroup.eu

STATINIO PROJEKTO PAVADINIMAS
Gyvenamosios paskirties (vieno buto) pastato , Beržų g. 24, statybos projektas

A1675	PV		
A1675	PDV SA		
0027195	Arch.		

STATINIO NR. IR PAVADINIMAS
INTERJERO DALIS
IŠKLOTINIŲ IR APDAILŲ PLANAS


LAIDA: 0


It

STATYTOJAS IR (ARBA) UŽSAKOVAS


DOKUMENTO ŽYMUO
MAK 01230523-01-TDP-SA. B-02


LAPAS: 9
LAPŲ: 15

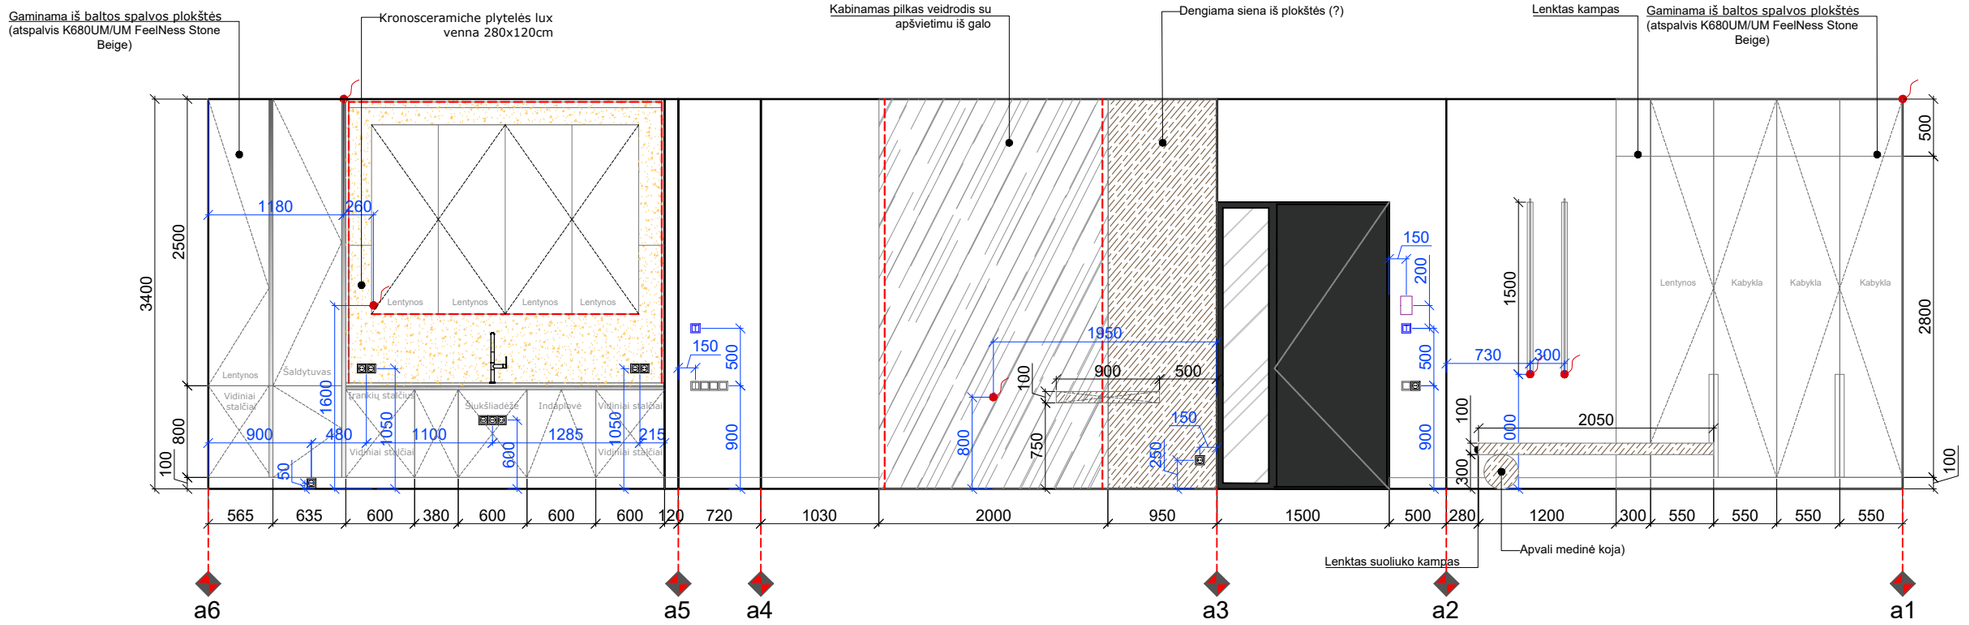

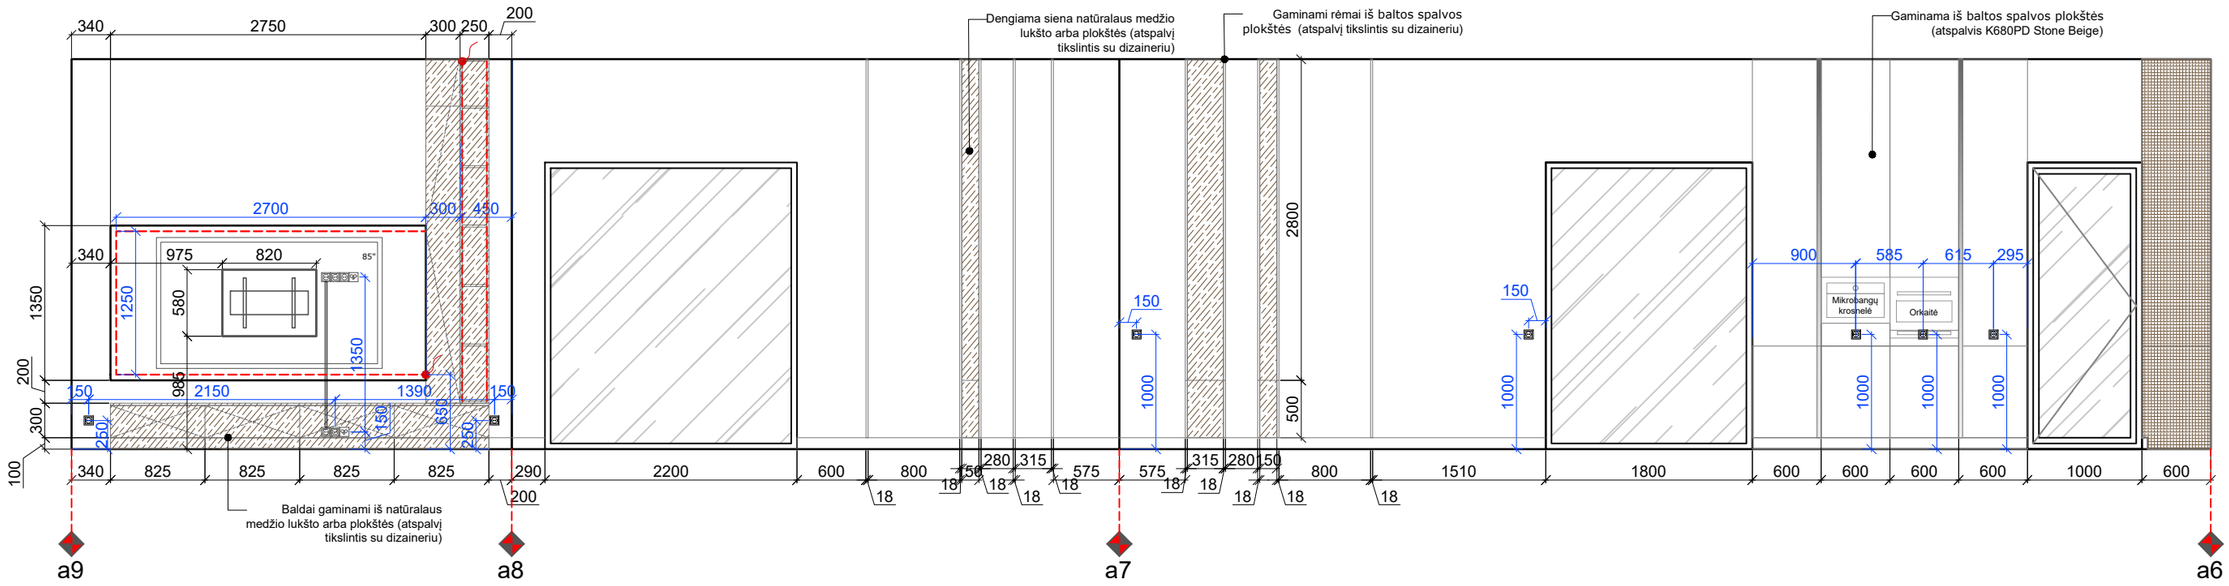



0		
LAIDA	DATA	LAIDOS STATUSAS. KEITIMO PRIEŽASTIS (JEI TAIKOMA)
KVAL. DOK. NR.	UAB MAK GROUP Įm.k. 302735585 Adr.:Parodos g. 20, Kaunas Tel.: +37068398769 El. paštas : info@makgroup.eu www.makgroup.eu	STATINIO PROJEKTO PAVADINIMAS Gyvenamosios paskirties (vieno buto) pastato , Beržų g. 24, statybos projektas
	DIZ G.Umbraitė	STATINIO NR. IR PAVADINIMAS INTERJERO DALIS IŠKLOTINĖS — LAIDA 0
lt	STATYTOJAS IR (ARBA) UŽSAKOVAS S.B., R.B.	DOKUMENTO ŽYMUO SA.B-02 — LAPAS 10 — LAPŲ 16

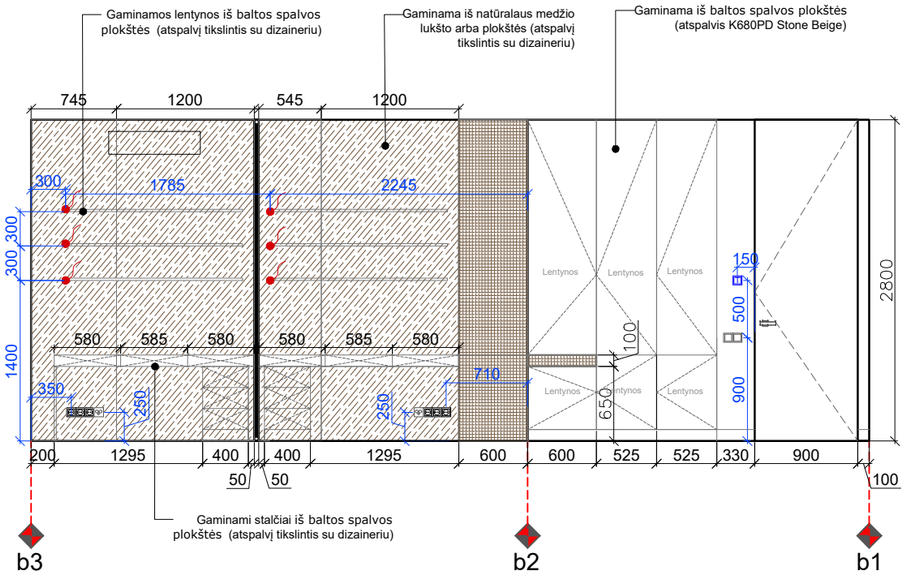

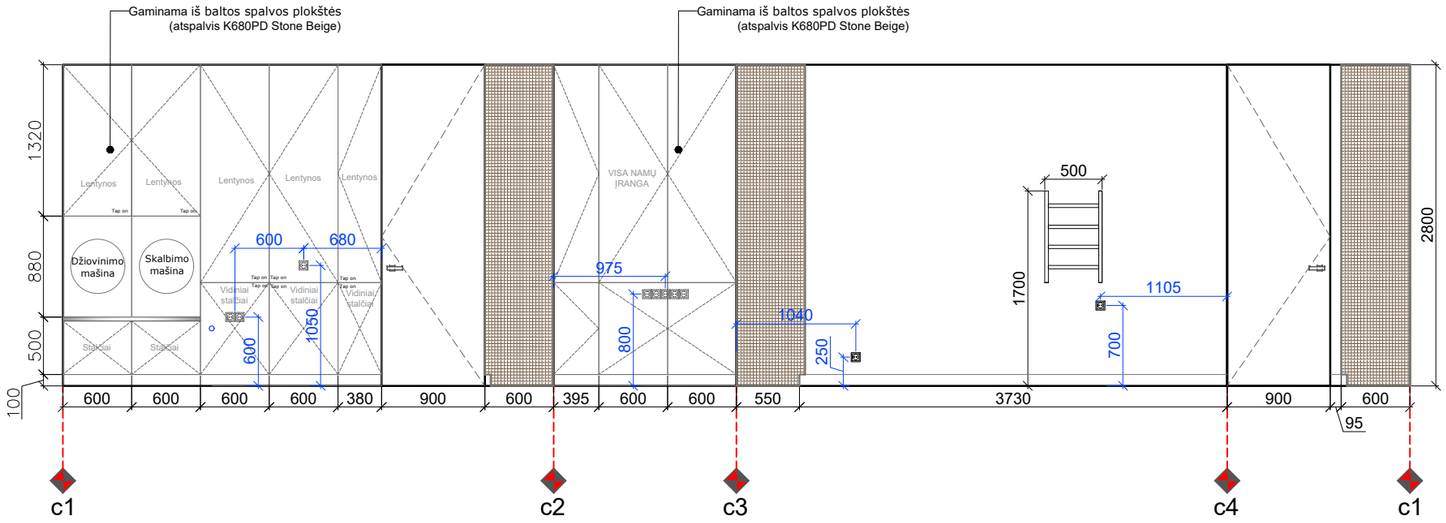



0				
LAIDA	DATA	LAIDOS STATUSAS. KEITIMO PRIEŽASTIS (JEI TAIKOMA)		
KVAL. DOK. NR.	UAB MAK GROUP Įm.k. 302735585 Adr.:Parodos g. 20, Kaunas Tel.: +37068398769 El. paštas : info@makgroup.eu www.makgroup.eu		STATINIO PROJEKTO PAVADINIMAS Gyvenamosios paskirties (vieno buto) pastato , Beržų g. 24, statybos projektas	
	DIZ	G.Umbraitė	STATINIO NR. IR PAVADINIMAS INTERJERO DALIS IŠKLOTINĖS	LAIDA 0
lt	STATYTOJAS IR (ARBA) UŽSAKOVAS S.B., R.B.		DOKUMENTO ŽYMUO SA.B-02	LAPAS 11 / LAPŲ 16

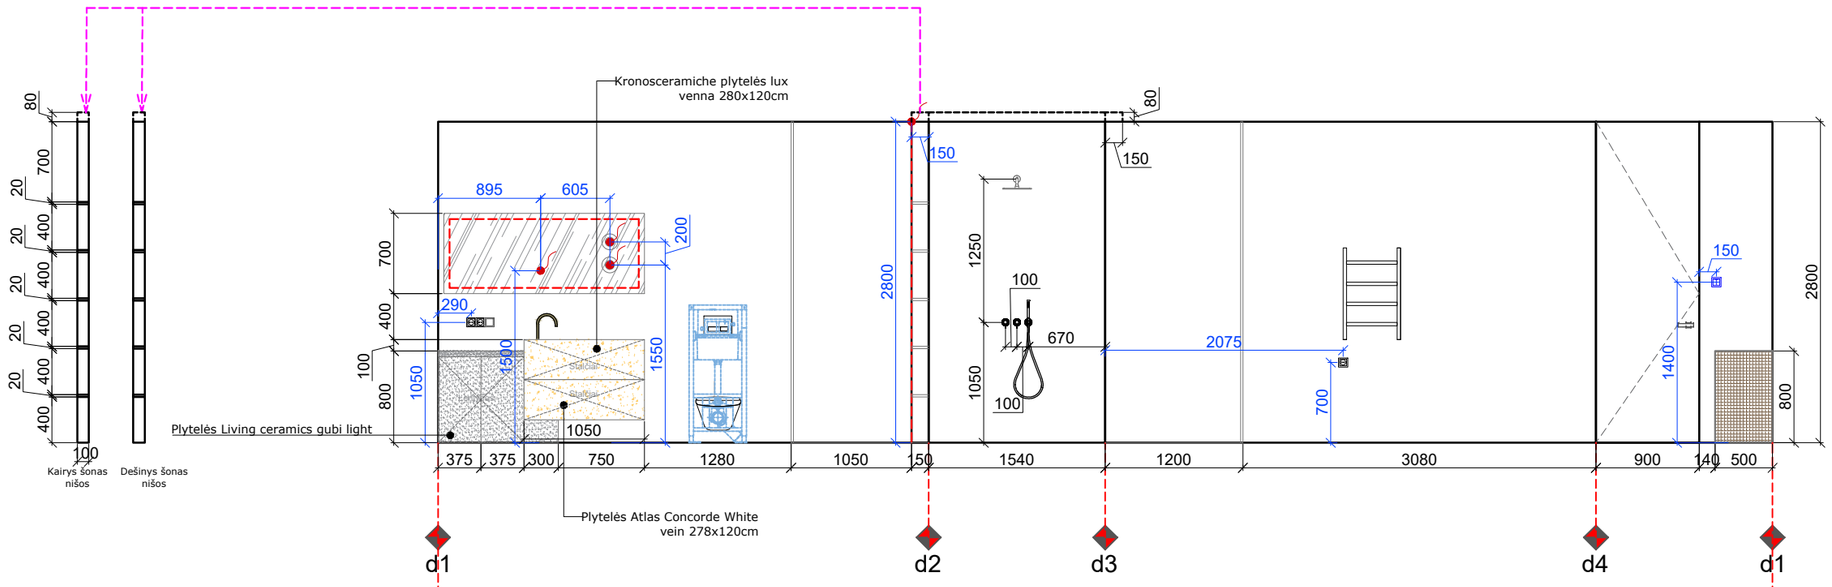

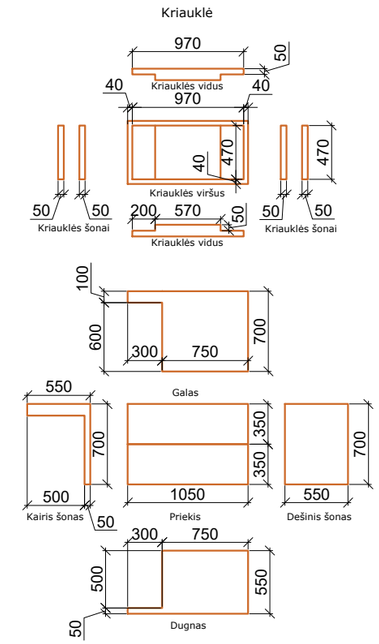


Plytelių išklotinės

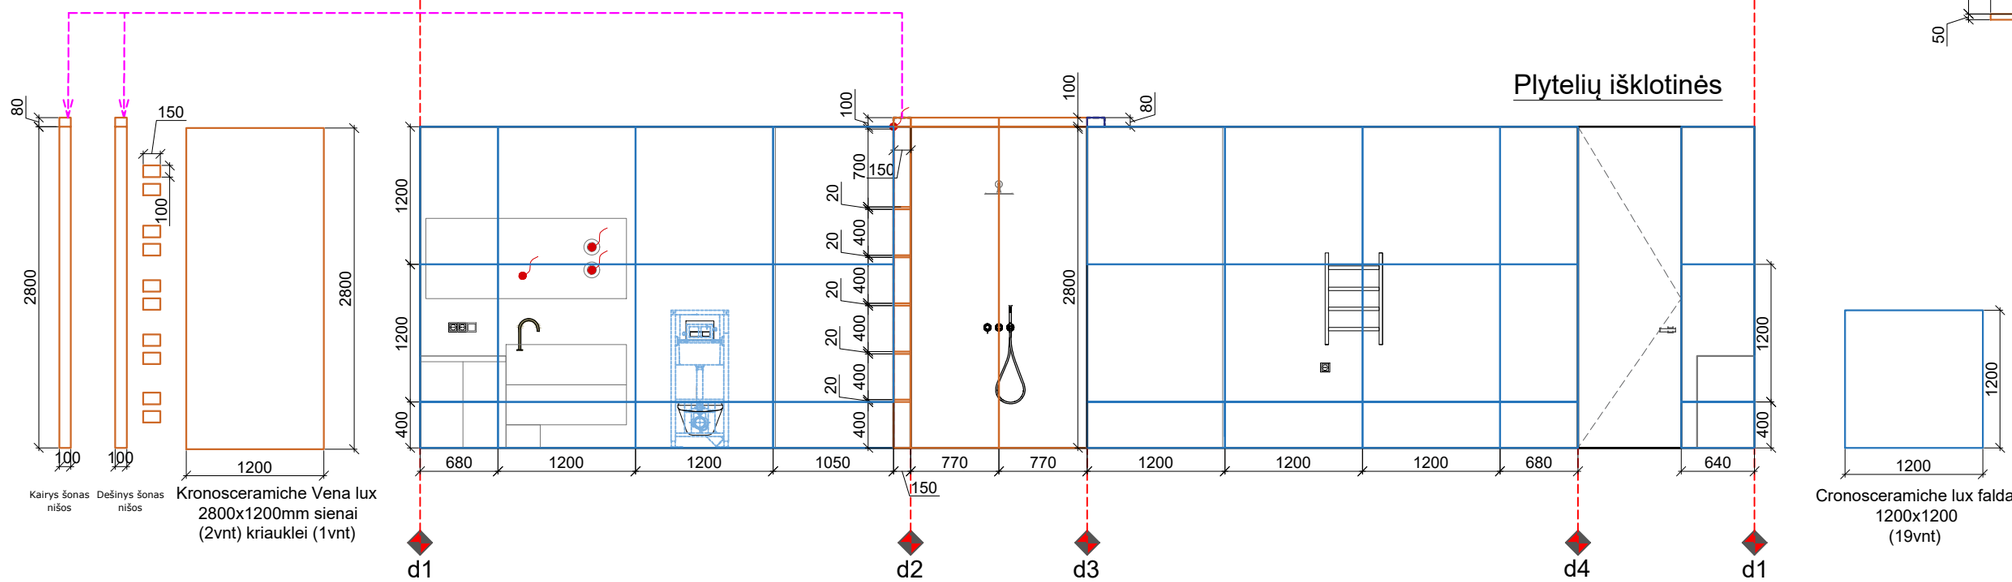


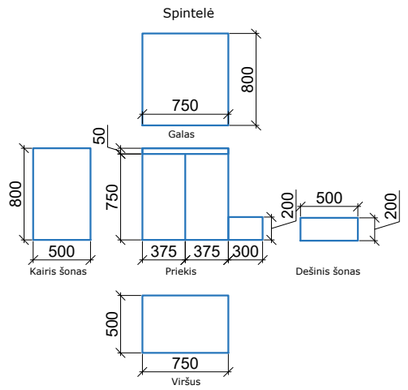




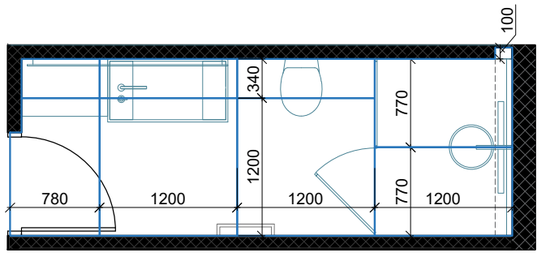



0				
LAIDA	DATA	LAIDOS STATUSAS. KEITIMO PRIEŽASTIS (JEI TAIKOMA)		
KVAL. DOK. NR.	UAB MAK GROUP Įm.k. 302735585 Adr.:Parodos g. 20, Kaunas Tel.: +37068398769 El. paštas : info@makgroup.eu www.makgroup.eu	STATINIO PROJEKTO PAVADINIMAS Gyvenamosios paskirties (vieno buto) pastato , Beržų g. 24, statybos projektas		
	DIZ	G.Umbraitė	STATINIO NR. IR PAVADINIMAS INTERJERO DALIS IŠKLOTINĖS	LAIDA 0
lt	STATYTOJAS IR (ARBA) UŽSAKOVAS S.B., R.B.		DOKUMENTO ŽYMUO SA.B-02	LAPAS 12 / LAPŲ 16

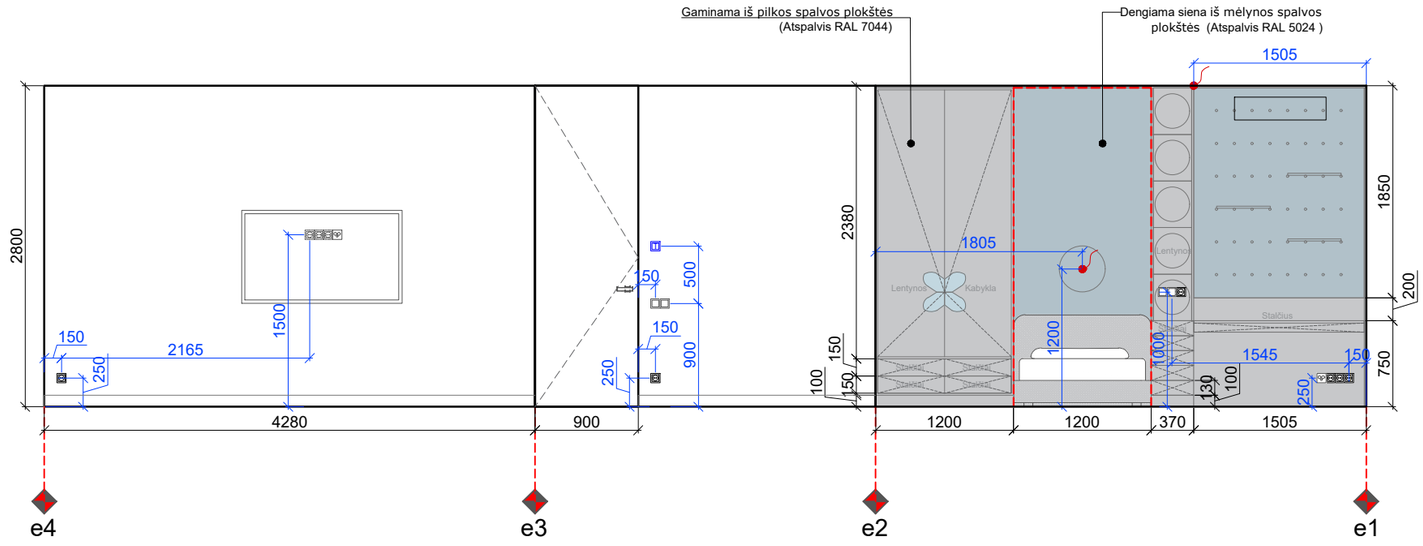

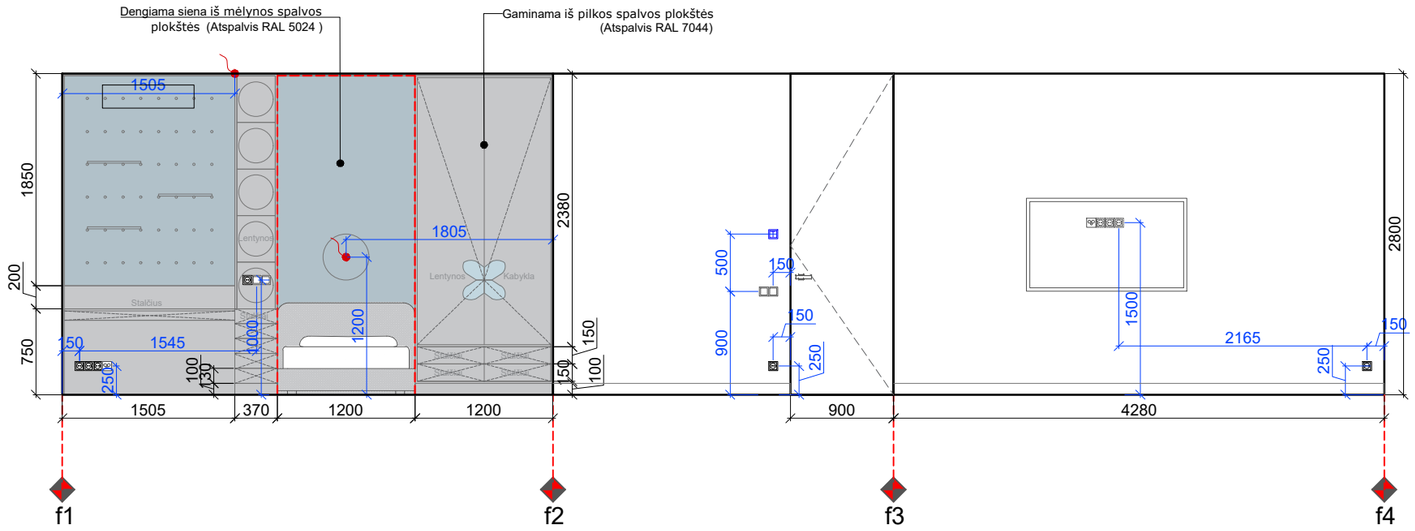



0				
LAIDA	DATA	LAIDOS STATUSAS. KEITIMO PRIEŽASTIS (JEI TAIKOMA)		
KVAL. DOK. NR.		UAB MAK GROUP Įm.k. 302735585 Adr.:Parodos g. 20, Kaunas Tel.: +37068398769 El. paštas : info@makgroup.eu www.makgroup.eu	STATINIO PROJEKTO PAVADINIMAS Gyvenamosios paskirties (vieno buto) pastato , Beržų g. 24, statybos projektas	
	DIZ	G.Umbraitė	STATINIO NR. IR PAVADINIMAS INTERJERO DALIS IŠKLOTINĖS	LAIDA 0
lt	STATYTOJAS IR (ARBA) UŽSAKOVAS S.B., R.B.		DOKUMENTO ŽYMUO SA.B-02	LAPAS 13 / LAPŲ 16

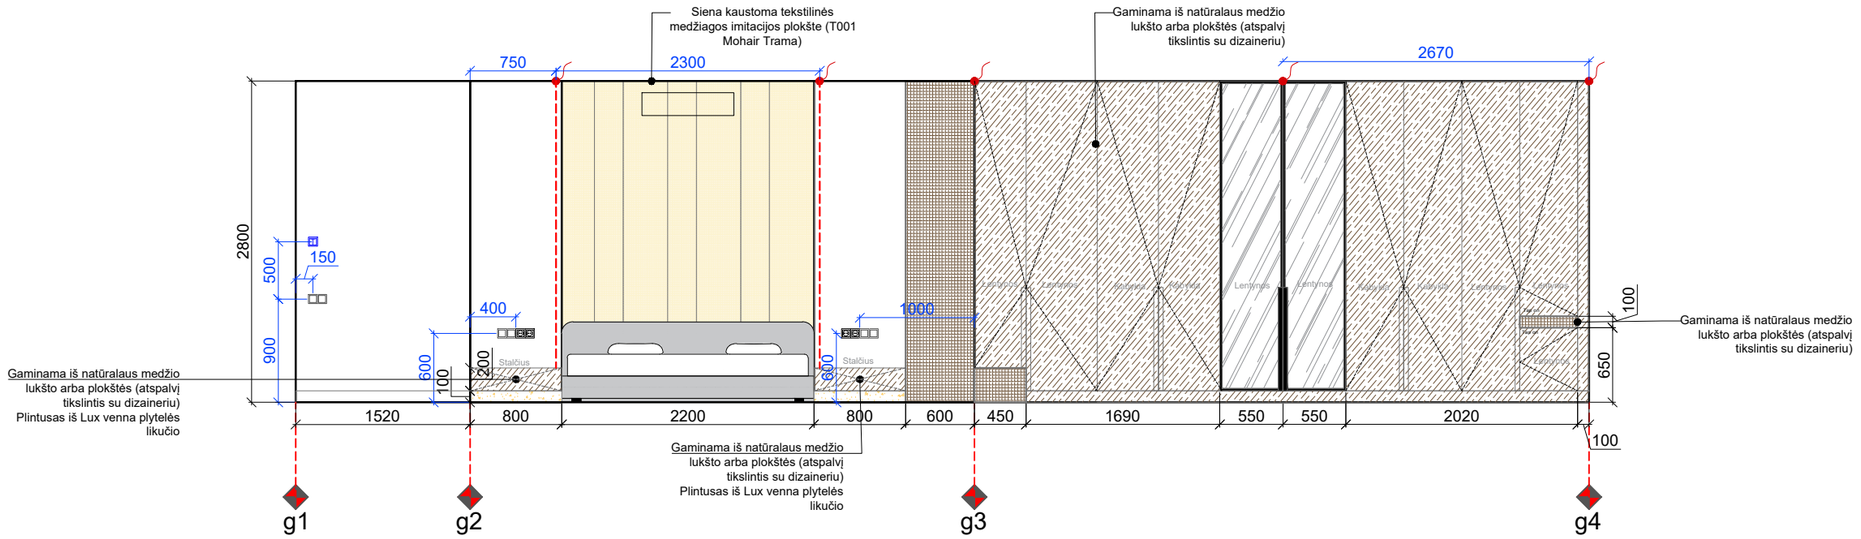

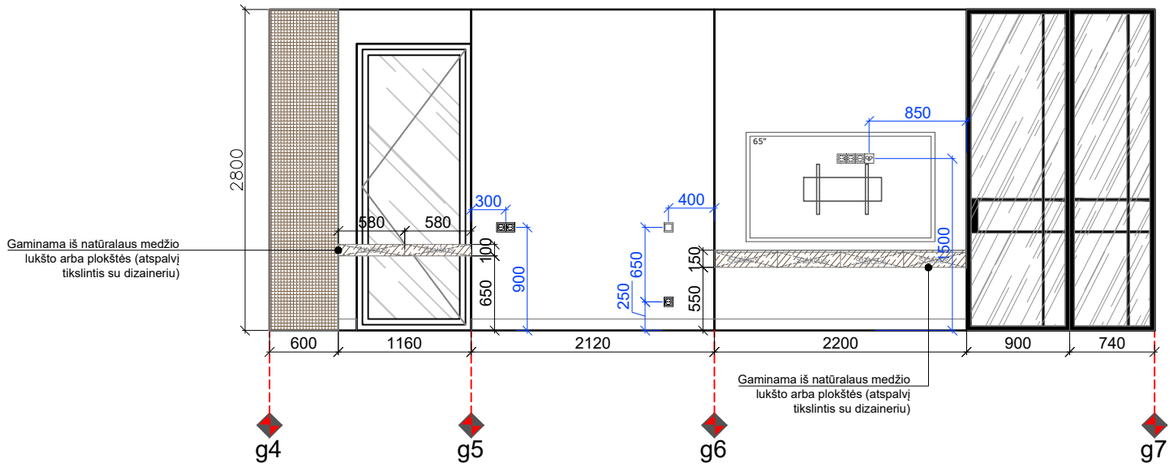



0				
LAIDA	DATA	LAIDOS STATUSAS. KEITIMO PRIEŽASTIS (JEI TAIKOMA)		
KVAL. DOK. NR.	UAB MAK GROUP Įm.k. 302735585 Adr.:Parodos g. 20, Kaunas Tel.: +37068398769 El. paštas : info@makgroup.eu www.makgroup.eu		STATINIO PROJEKTO PAVADINIMAS Gyvenamosios paskirties (vieno buto) pastato , Beržų g. 24, statybos projektas	
	DIZ	G.Umbraitė	STATINIO NR. IR PAVADINIMAS INTERJERO DALIS IŠKLOTINĖS	LAIDA 0
lt	STATYTOJAS IR (ARBA) UŽSAKOVAS S.B., R.B.		DOKUMENTO ŽYMUO SA.B-02	LAPAS 14 / LAPŲ 16

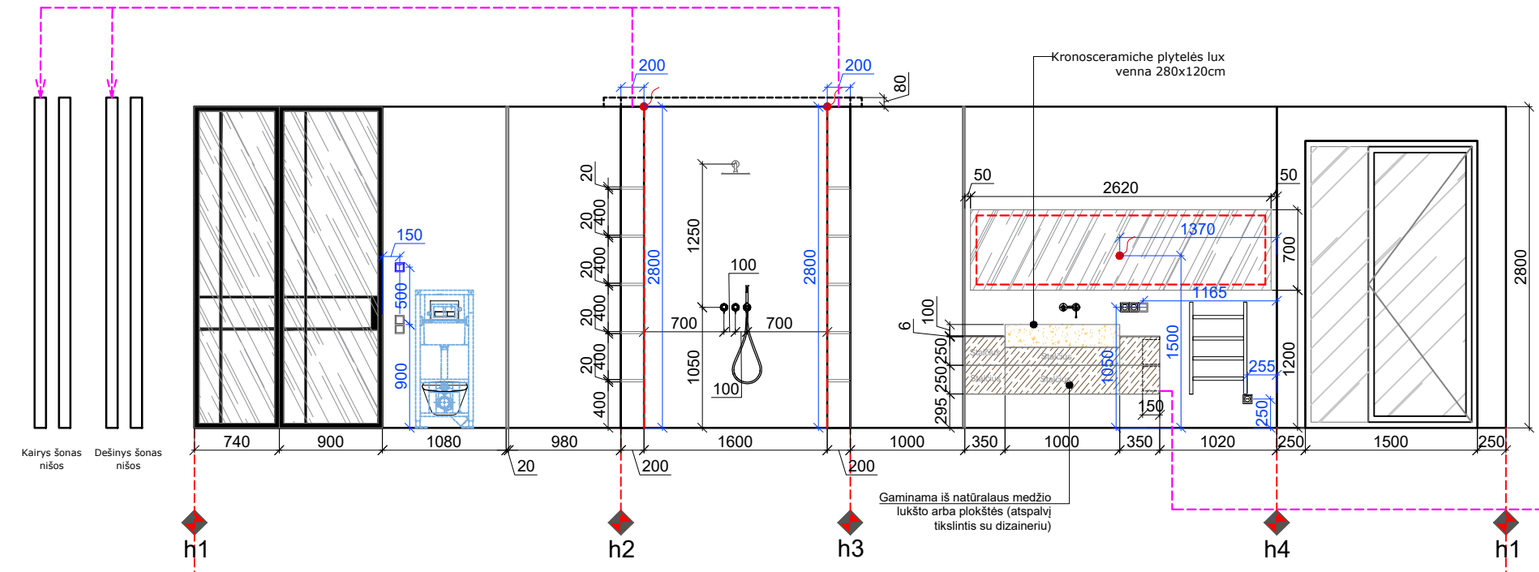


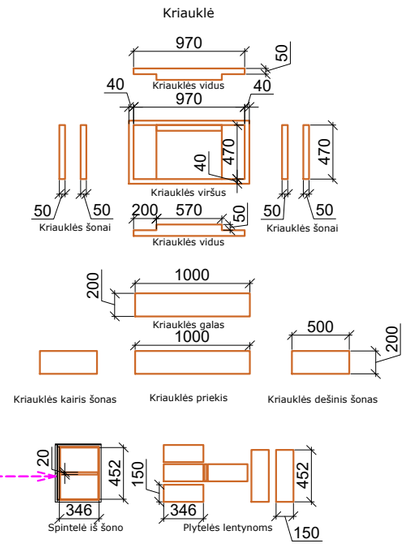


Plytelių išklotinės

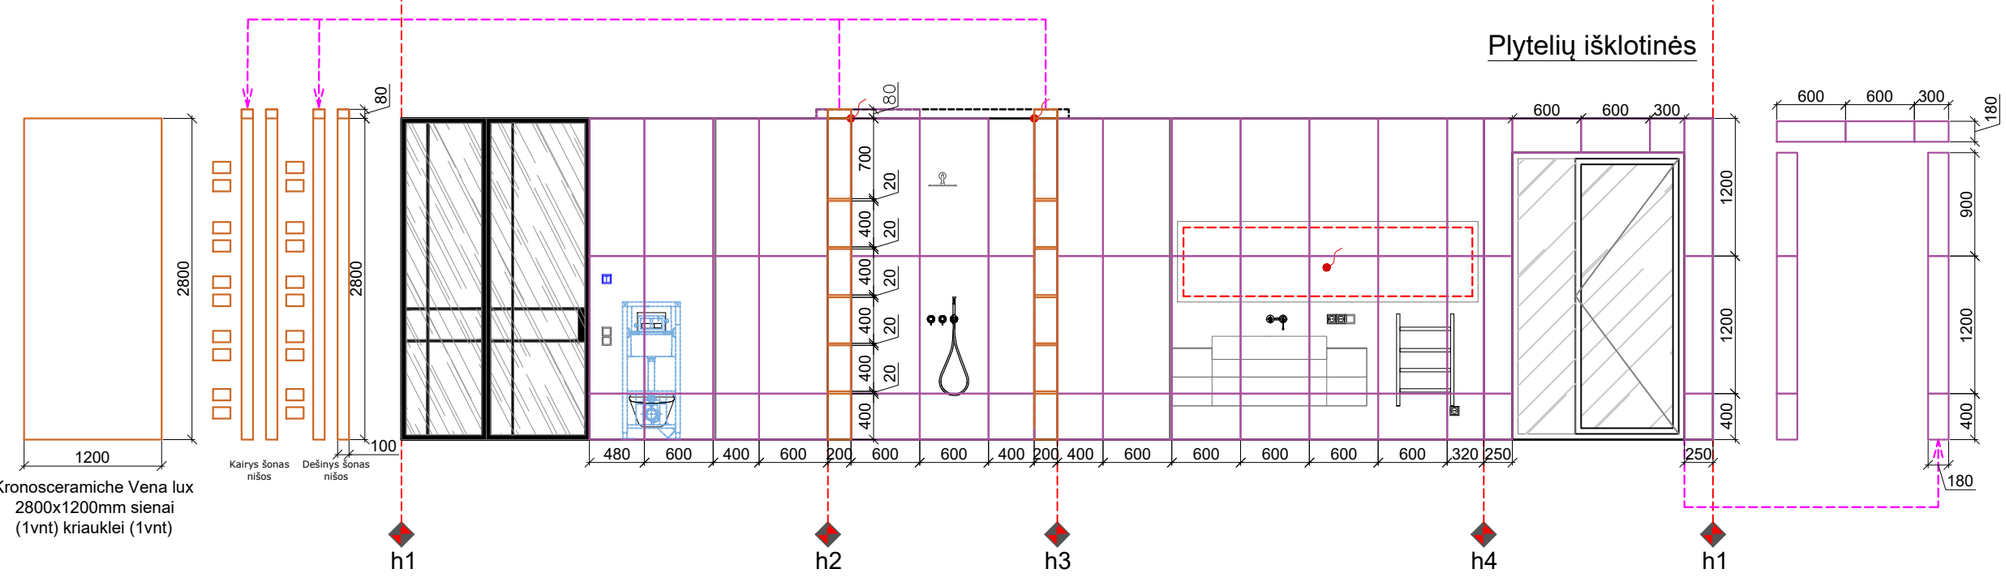

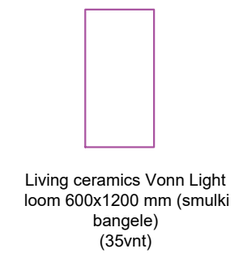


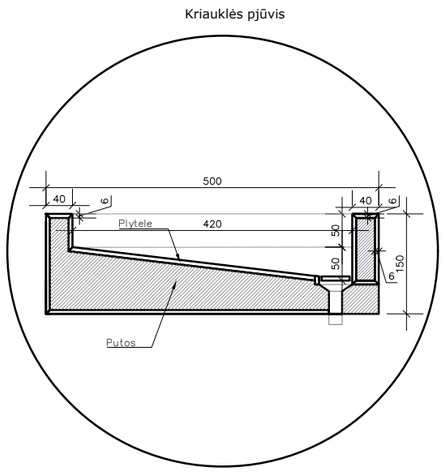


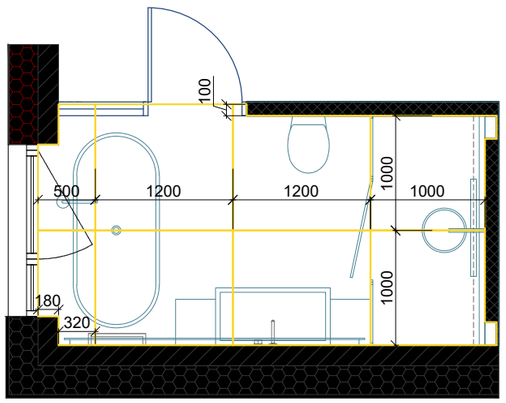


Living ceramics Vonn Light 1200x1200 (7vnt)

0				
LAIDA	DATA	LAIDOS STATUSAS. KEITIMO PRIEŽASTIS (JEI TAIKOMA)		
KVAL. DOK. NR.	UAB MAK GROUP Įm.k. 302735585 Adr.:Parodos g. 20, Kaunas Tel.: +37068398769 El. paštas : info@makgroup.eu www.makgroup.eu		STATINIO PROJEKTO PAVADINIMAS	
			Gyvenamosios paskirties (vieno buto) pastato , Beržų g. 24, statybos projektas	
	DIZ	G.Umbraitė	STATINIO NR. IR PAVADINIMAS	LAIDA
			INTERJERO DALIS IŠKLOTINĖS	0
lt	STATYTOJAS IR (ARBA) UŽSAKOVAS		DOKUMENTO ŽYMUO	LAPAS / LAPŲ
	S.B., R.B.		SA.B-02	15 / 16

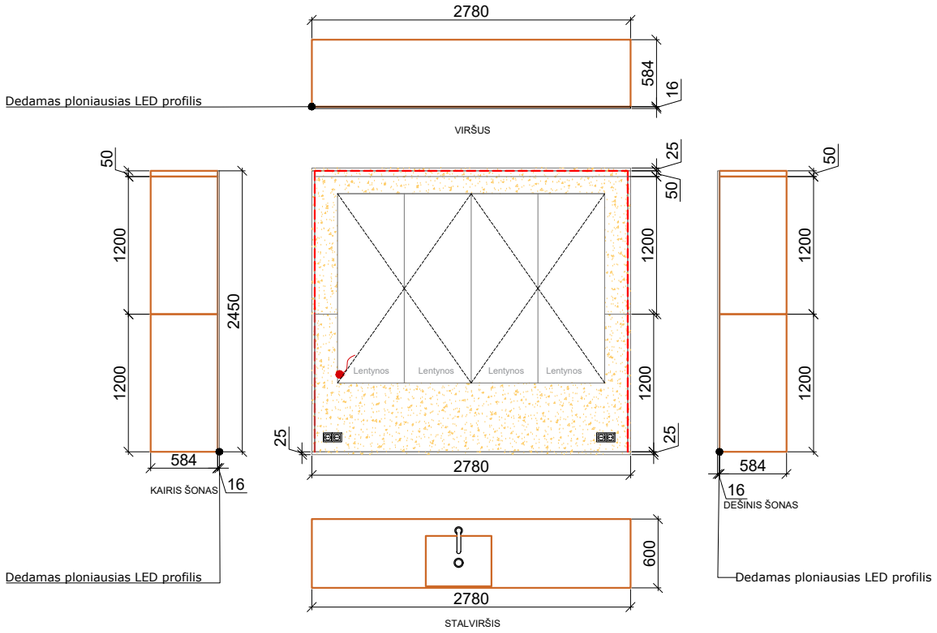

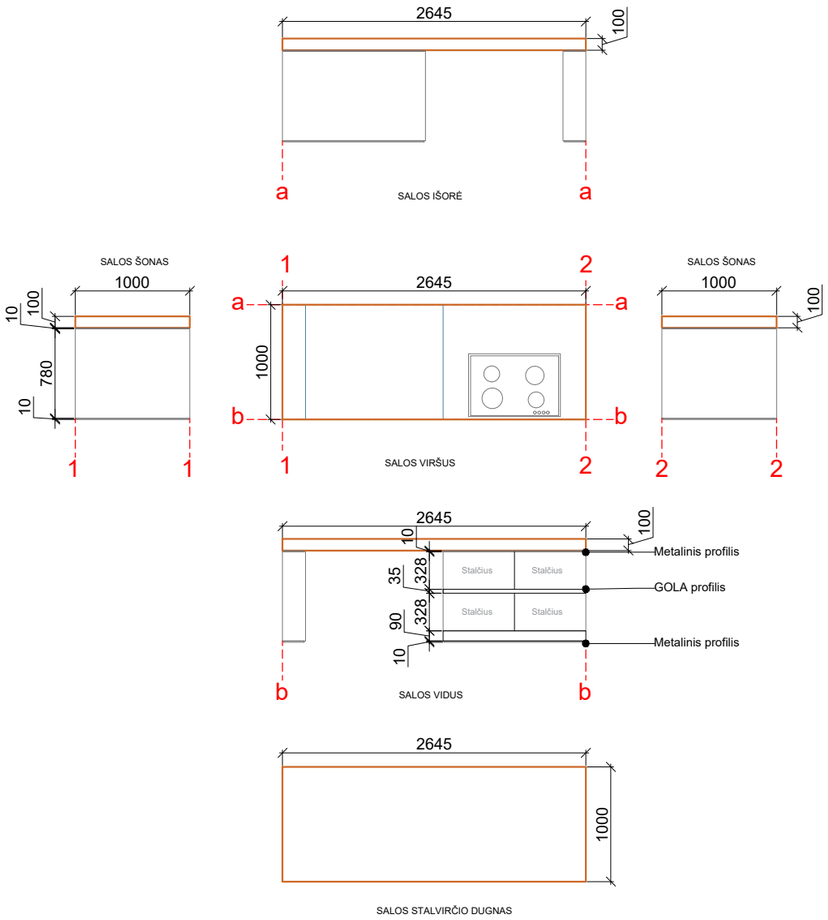

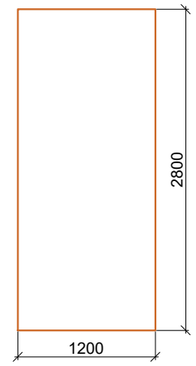

Kronosceramiche Lux venna 2800x1200mm (6vnt)

0				
LAIDA	DATA	LAIDOS STATUSAS. KEITIMO PRIEŽASTIS (JEI TAIKOMA)		
KVAL. DOK. NR.	UAB MAK GROUP Įm.k. 302735585 Adr.:Parodos g. 20, Kaunas Tel.: +37068398769 El. paštas : info@makgroup.eu www.makgroup.eu		STATINIO PROJEKTO PAVADINIMAS Gyvenamosios paskirties (vieno buto) pastato , Beržų g. 24, statybos projektas	
	DIZ	G.Umbraitė	STATINIO NR. IR PAVADINIMAS INTERJERO DALIS IŠKLOTINĖS	LAIDA 0
lt	STATYTOJAS IR (ARBA) UŽSAKOVAS S.B., R.B.		DOKUMENTO ŽYMUO SA.B-02	LAPAS 16 / LAPŲ 16