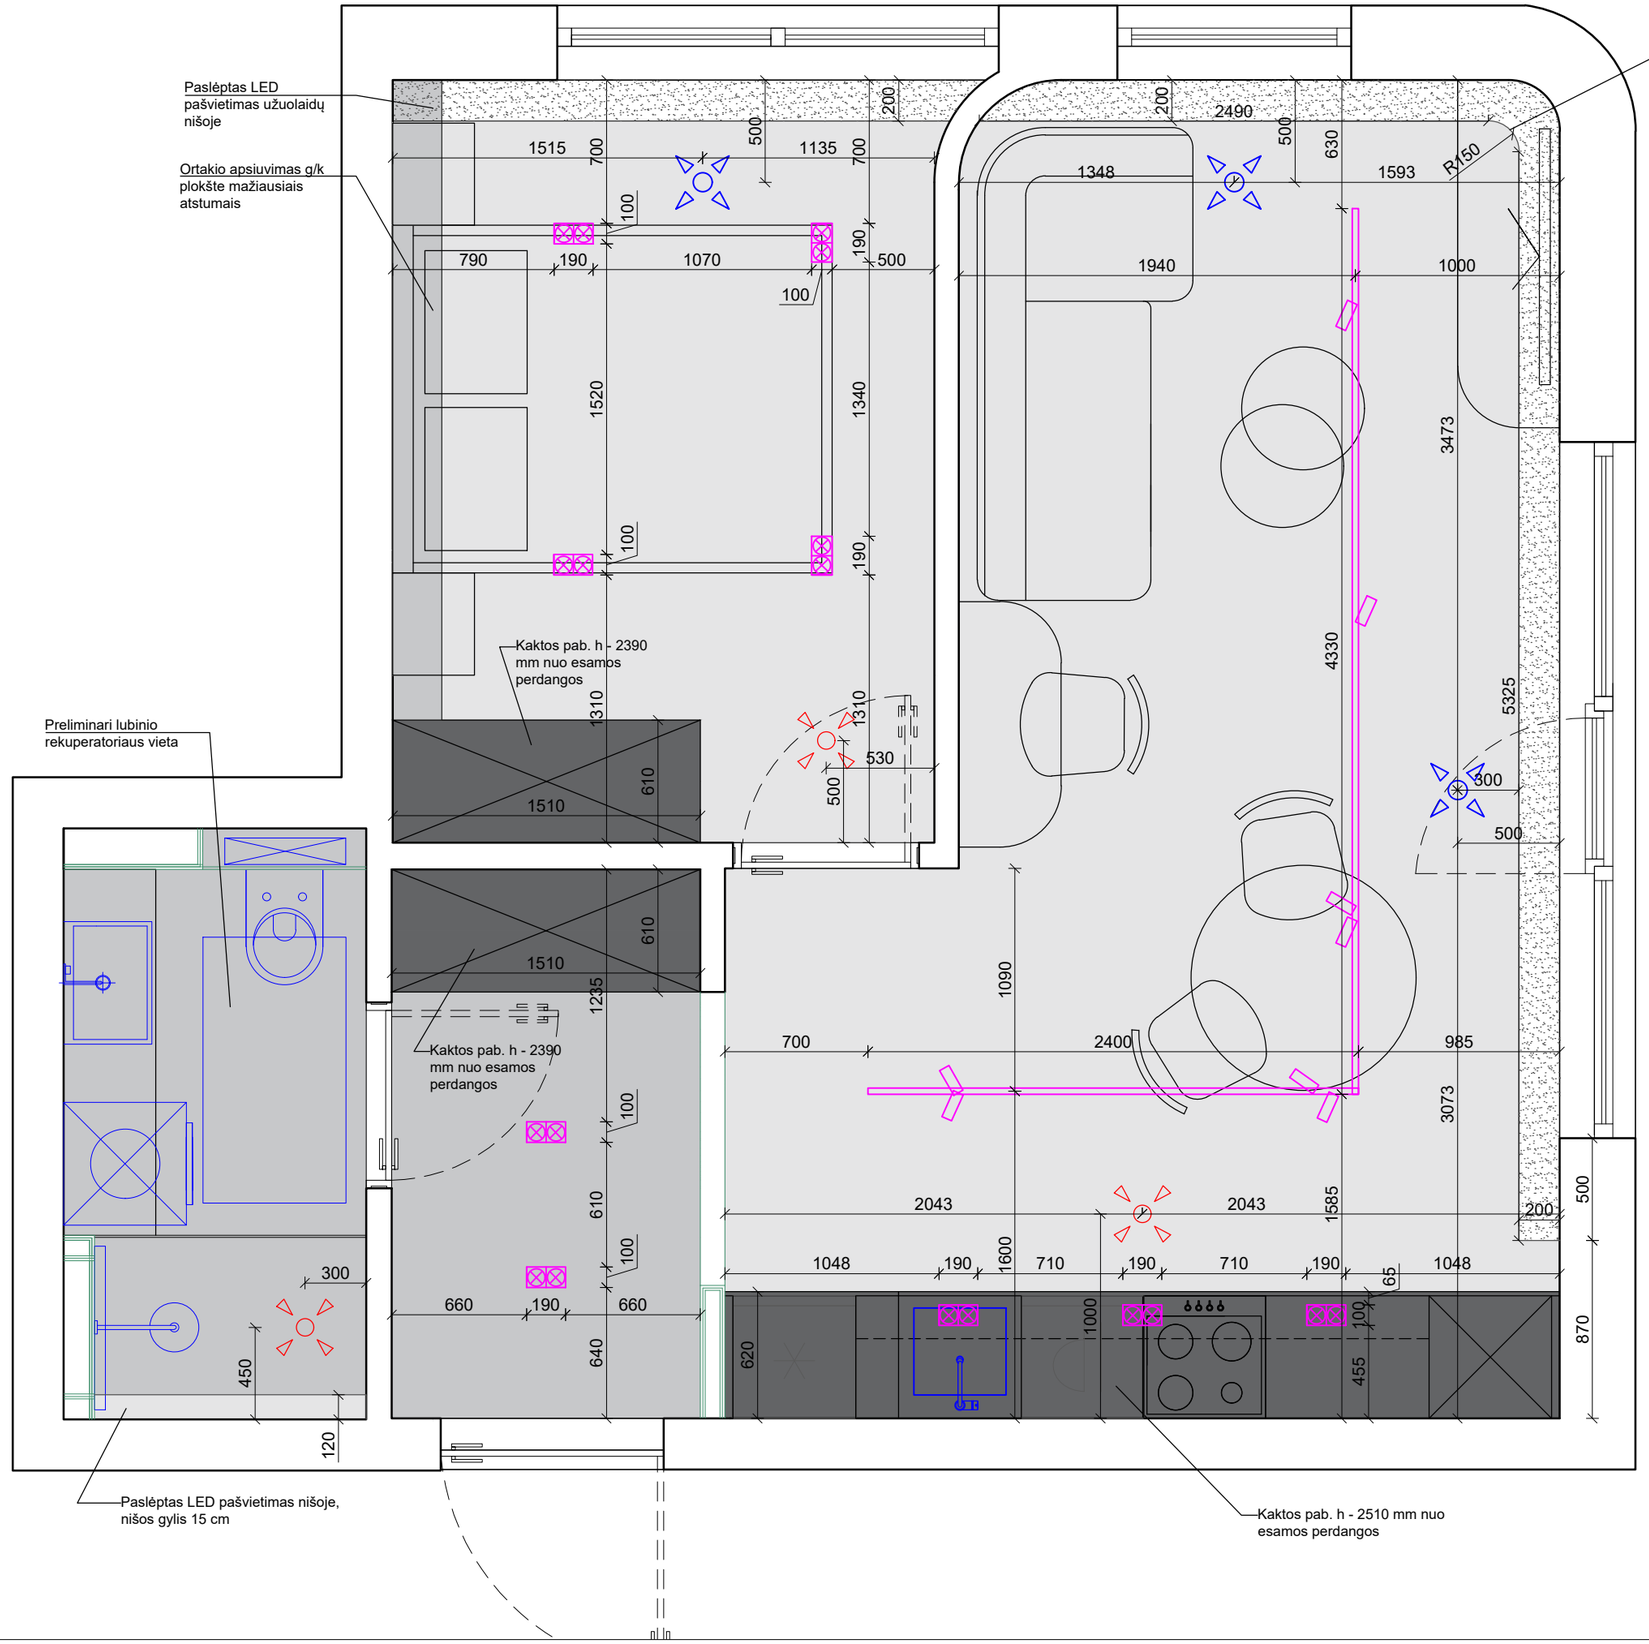


SUTARTINIS ŽYMĖJIMAS:

- Pakabinamos gipso kartono lubos, -160 mm
- Pakabinamos gipso kartono lubos, leisti kiek įmanoma mažiau
- Gipso kartono "kaktos" baldams, pagal nurodytą aukštį
- Niša užuolaidoms, klijuojamas gipso kartonas arba glaistoma esama perdanga
- Priglaistomi apvalūs difuzoriai gipso kartono lubose
- Priglaistomi dvigubi gipsiniai šviestuvai su LED lempute G10
- Priglaistomas magnetinis bėgellis, 54 mm gylio

PASTABOS:

1. Lubos dažomos bazine balta spalva.
2. Lubos montuojamos su šešėline siūle prie sienos 1-2 mm.

Pakabinamų g/k lubų planas. M 1:30

Interjero dizainerė Marija Orlovienė, +370 620 81230, marija@strix.studio